



20
25

PORTFOLIO

JISHNU KALLINGAL



JISHNU KALLINGAL

INTERIOR DESIGNER & DRAFT MAN

CONTACT

📍 Kallingal [H] Vengad [P.O] Karuparamb
Malappuram District , kerala
📞 8073100366
✉️ jishnukallingal449@gmail.com

EXPERIENCE

D.U.N.E [BENGALURU]

Draft man [2022 - 2025]

Prepared detailed 2D drawings and technical plans using AutoCAD, including layouts, elevations, and sections for construction projects. Collaborated with architects and designers to translate concepts into precise technical drawings, ensuring design intent and accuracy.

SKILLS

Collaboration



Detailed working drawing



Space planning



Furniture and flooring



SOFTWARS



Auto cad



Sketch up



Photoshop



D5 render

TABLE OF CONTENT

1. ARCHITECTURAL PLAN	03
2. SECTIONS	07
3. WORKING DRAWING	12
4. ELECTRICAL DRAWING	16
5. DOOR AND WINDOW DETAILS	21
6. PLUMBING DRAWING	34
7. FLOORING DETAIL	39
8. DETAILS	41
9. ISOMETRIC VIEWS	51
10. 3D MODELS	56
11. PRESENTATION SHEET	60

ARCHITECTURAL PLANS

D. U. N. E

design unfiltered, a process never ending
54/2, 4th cross, Link road, Malleshwaram, Bangalore 560-003
designadune@gmail.com +91 23469351

PROJ

PROPOSED RESIDENCE FOR SATHYA & ABHILASH

BBM

ARCHITECTURAL
DRAWING

1

GROUND AND FIRST
FLOOR PLAN

DATE 16 - 11 - 2022

SCALE $\frac{1}{8}$ " = 1'0"

PRINT C

DRAWN BY JISHNU.K

CHECKED BY THEERTHAK

NOTE

GROUND FLOOR AREA
=1366 SQFT

FIRST FLOOR AREA
=1791 SQFT

—


SAR@S

DRAW


AR-001

REV

SECTION NUMBER

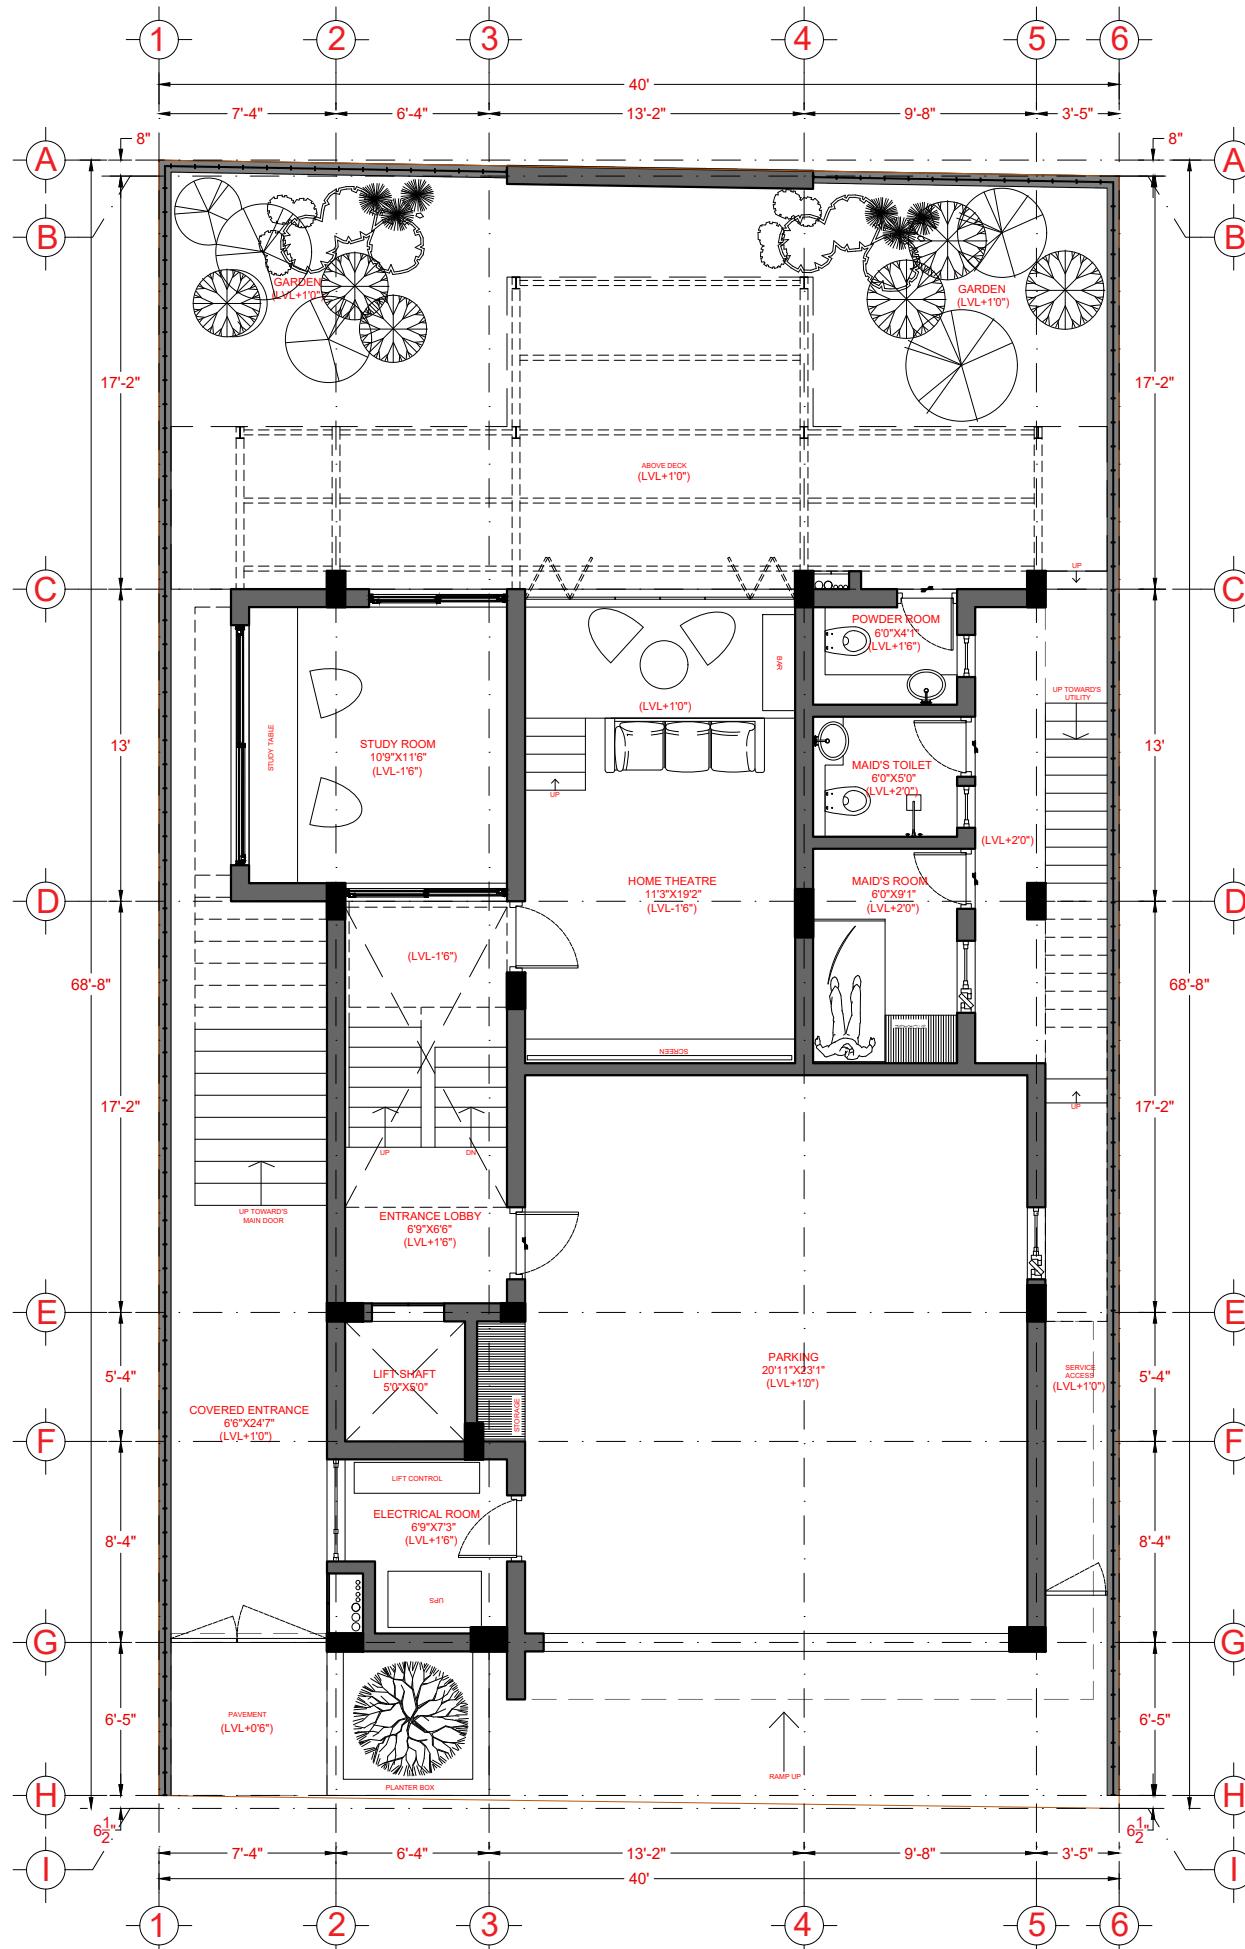

GROUND FLOOR PLAN

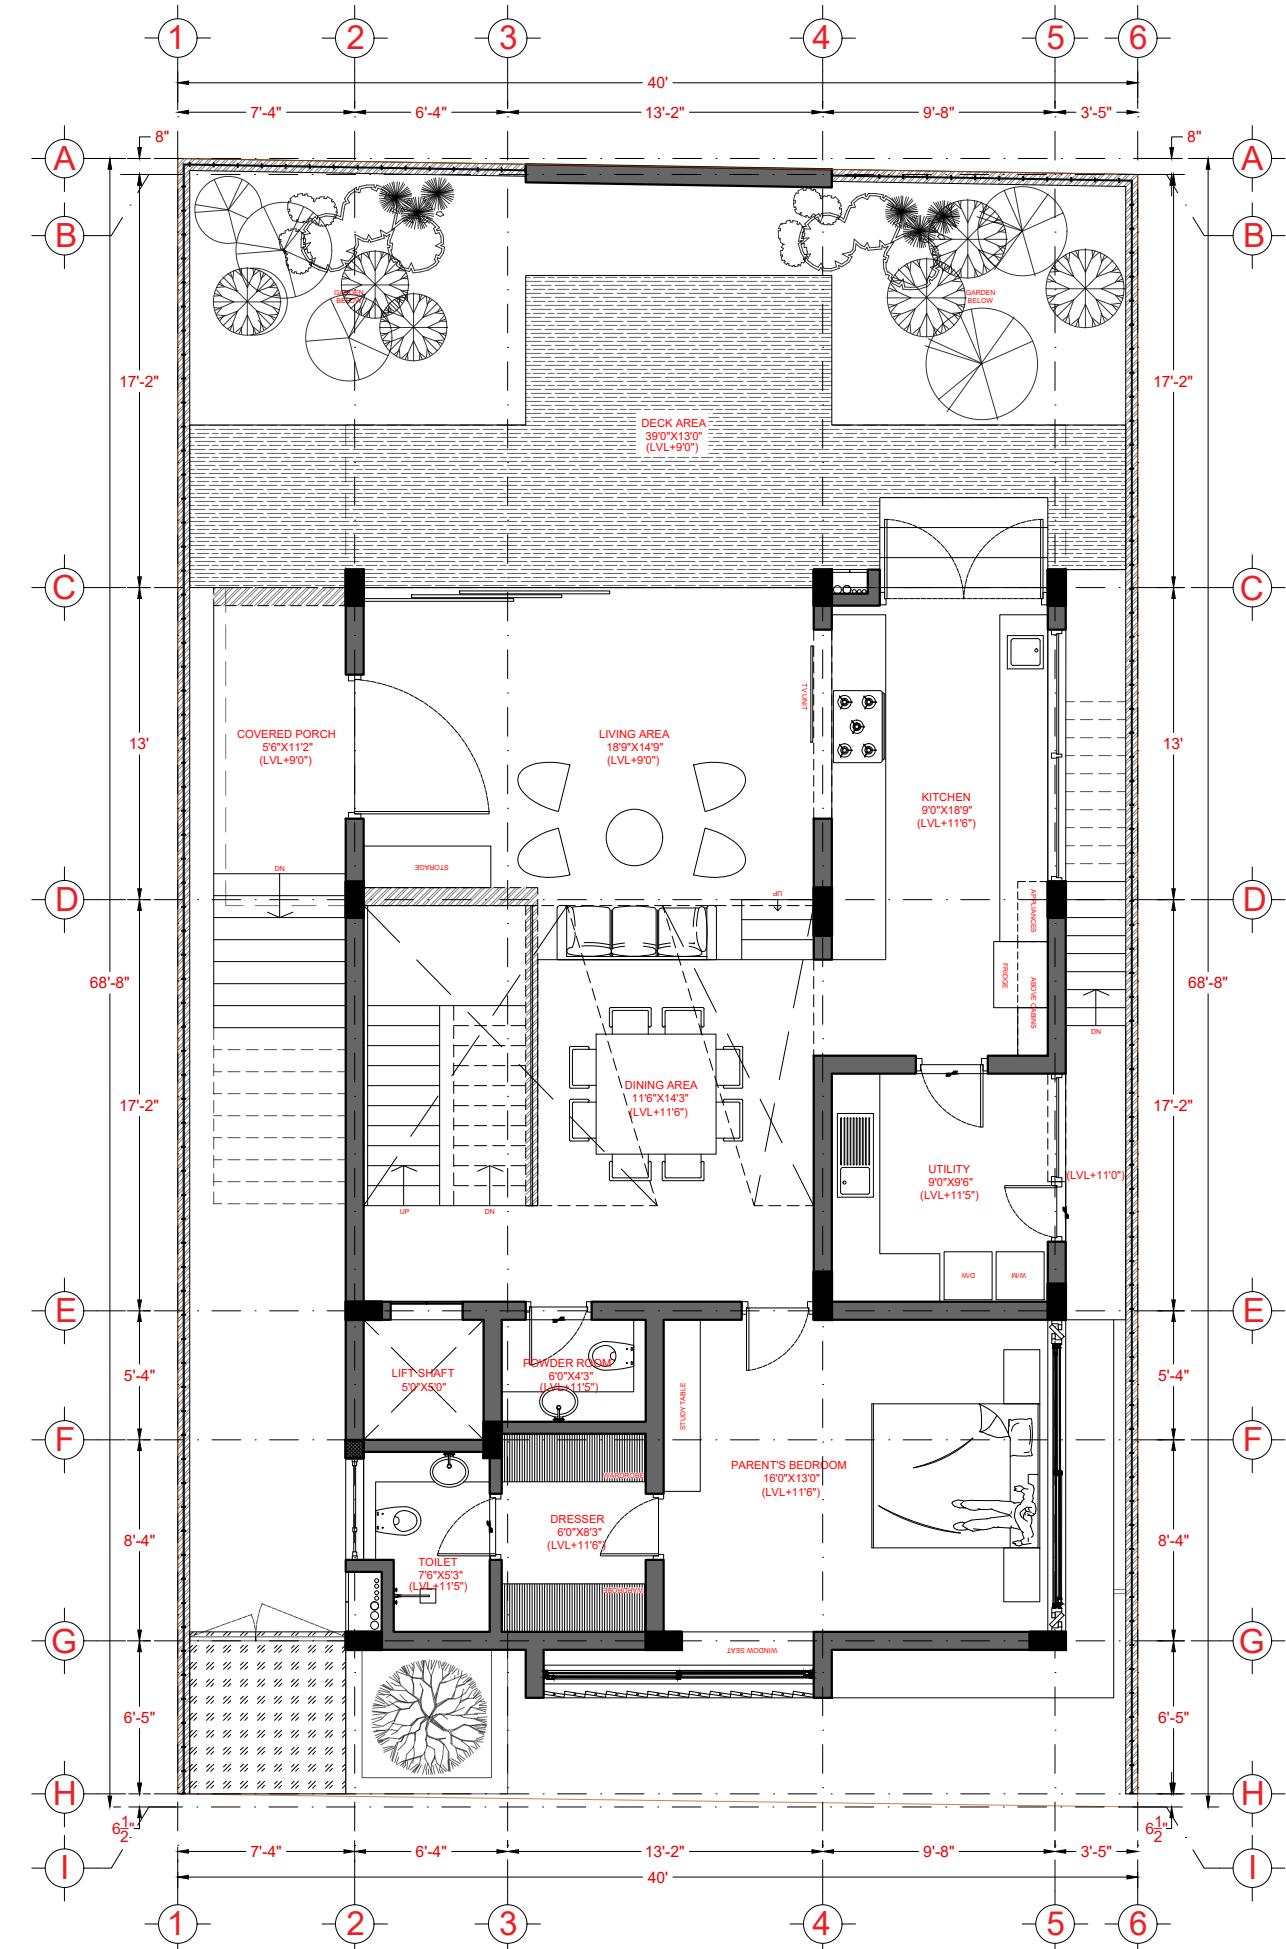

FIRST FLOOR PLAN



D. U. N. E

design unfiltered, a process never ending
54/2, 4th cross, Link road, Malleshwaram, Bangalore 560-003
designadune@gmail.com +91 23469351

PROJECT

PROPOSED RESIDENCE
FOR SATHYA & ABHILASH

DRAWING TITLE

ARCHITECTURAL
DRAWING

DRAWING TITLE

SECOND AND TERRACE
FLOOR PLAN

DATE 16 - 11 - 2022

SCALE 1" = 1'0"

PRINT ON A3

DRAWN BY JISHNU.K

CHECKED BY THEERTHAK

NOTE



SECOND FLOOR AREA
=1420 SQFT

TERRACE FLOOR AREA
=1216 SQFT

PROJECT CODE SAR@S

DRAWING NUMBER AR-002

REVISION NUMBER 0

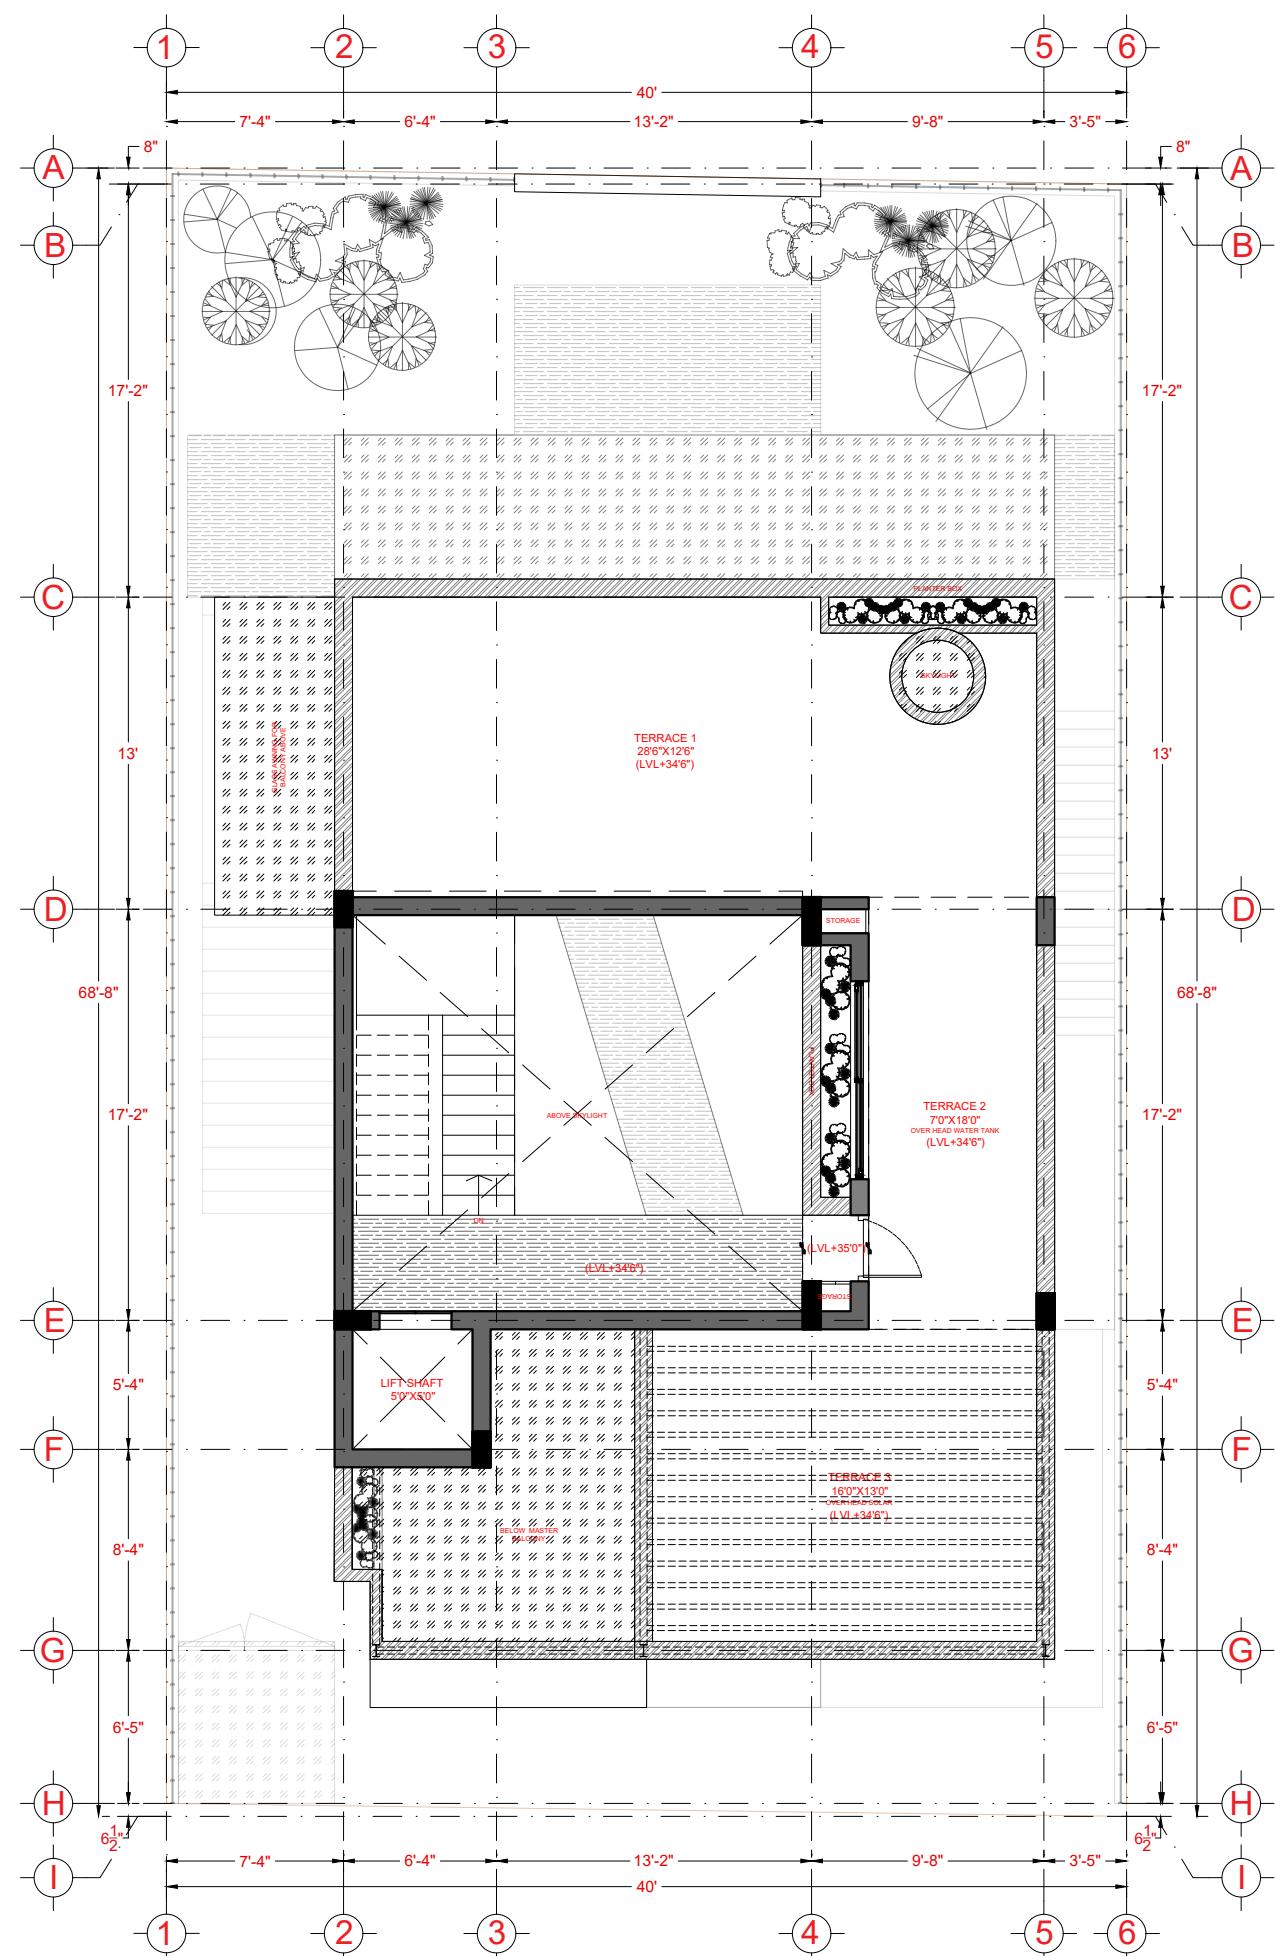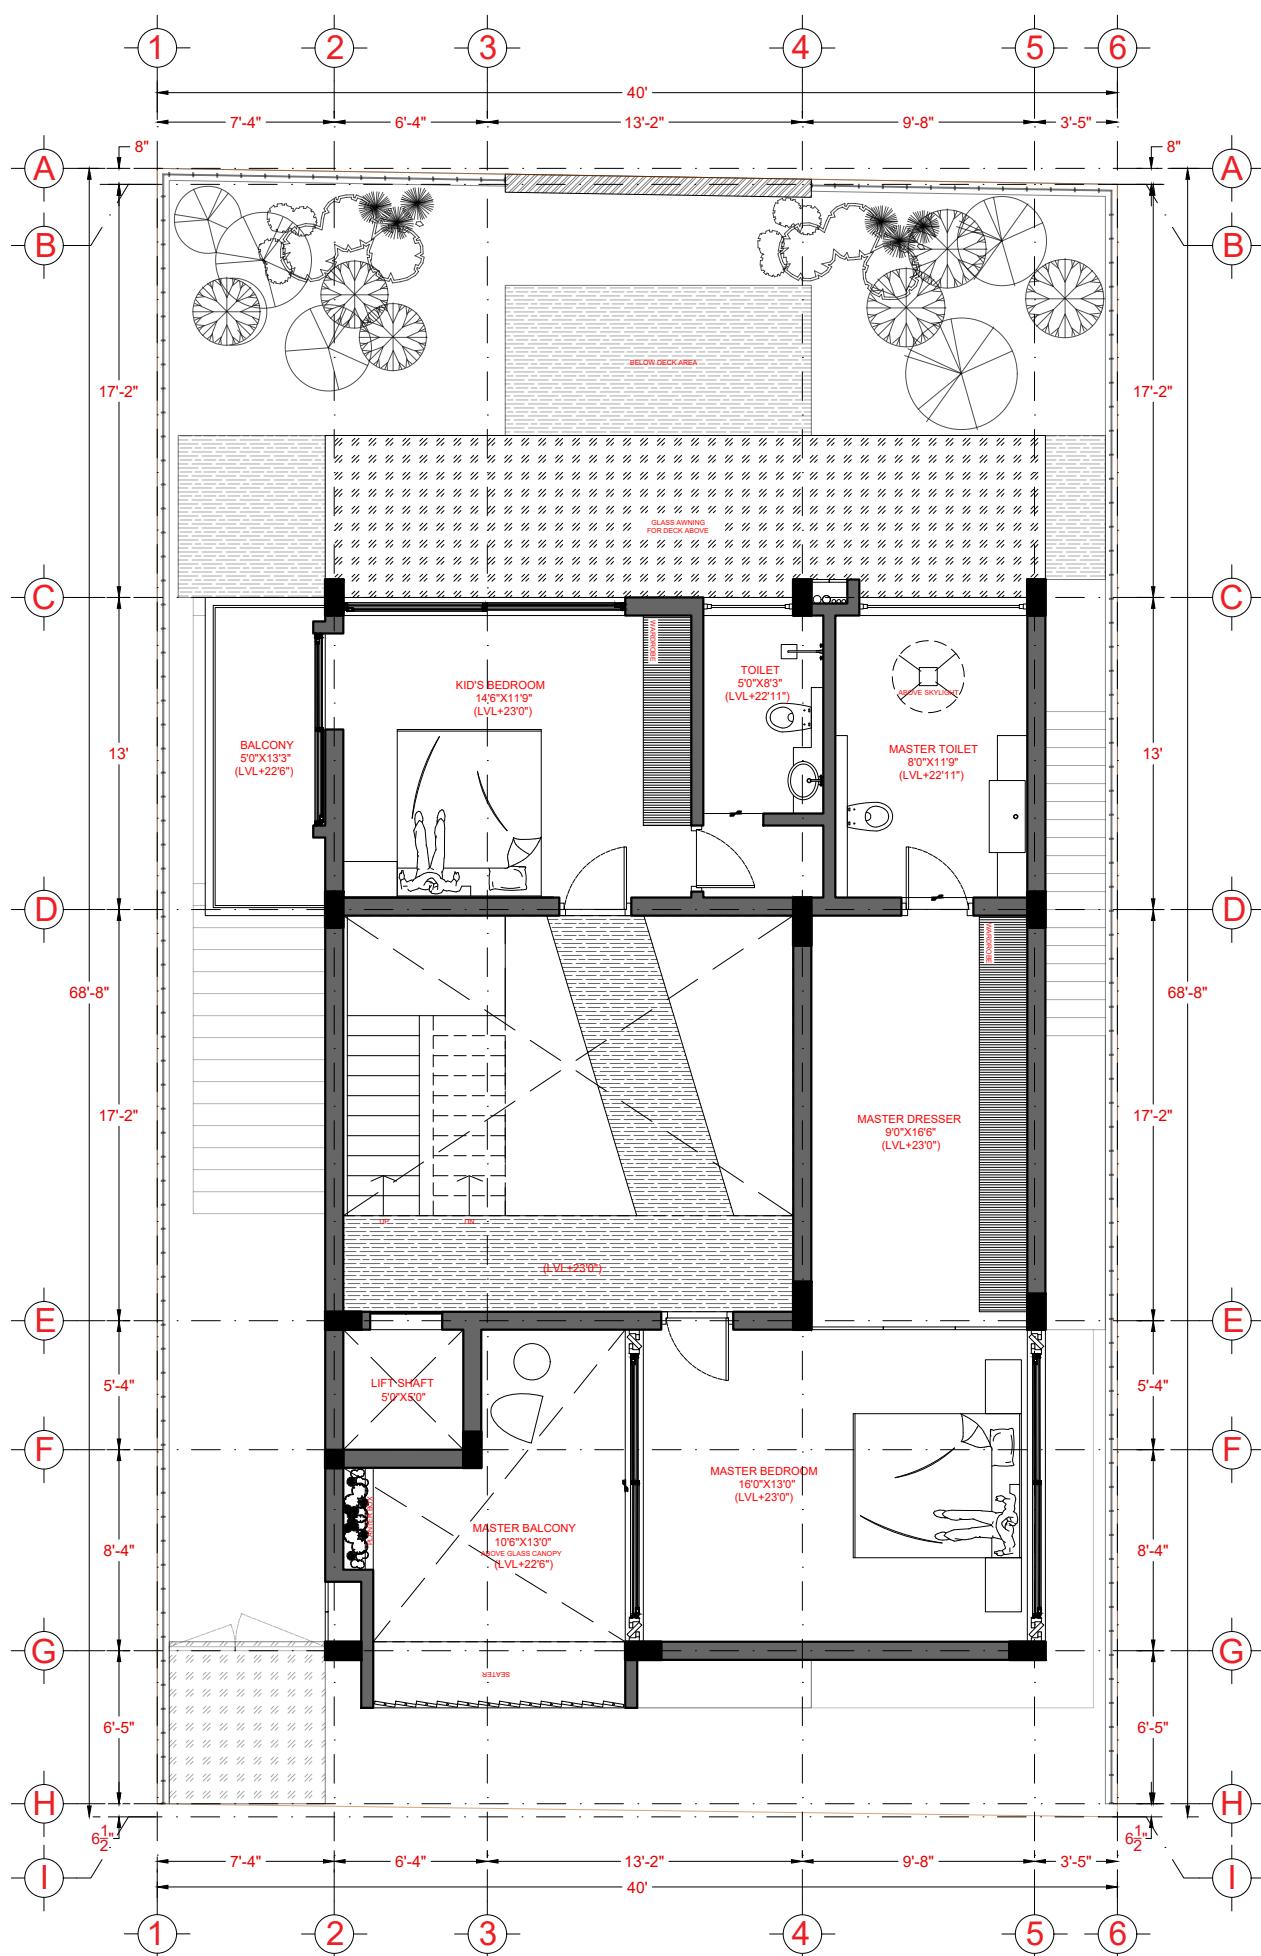

D. U. N. E

design unfiltered, a process never ending
54/2, 4th cross, Link road, Malleshwaram, Bangalore 560-003
designadune@gmail.com +91 23469351

PROJECT

PROPOSED RESIDENCE
FOR SATHYA & ABHILASH

DRAWING TITLE

ARCHITECTURAL
DRAWING

DRAWING TITLE

ROOF PLAN & FRONT
ELEVATION

DATE 16 - 11 - 2022

SCALE 1" = 1'0"
8

PRINT ON A3

DRAWN BY JISHNU.K

CHECKED BY THEERTHAK

NOTE


ROOF AREA
=255 SQFT

PROJECT CODE SAR@S

DRAWING NUMBER AR-003

REVISION NUMBER 0

N

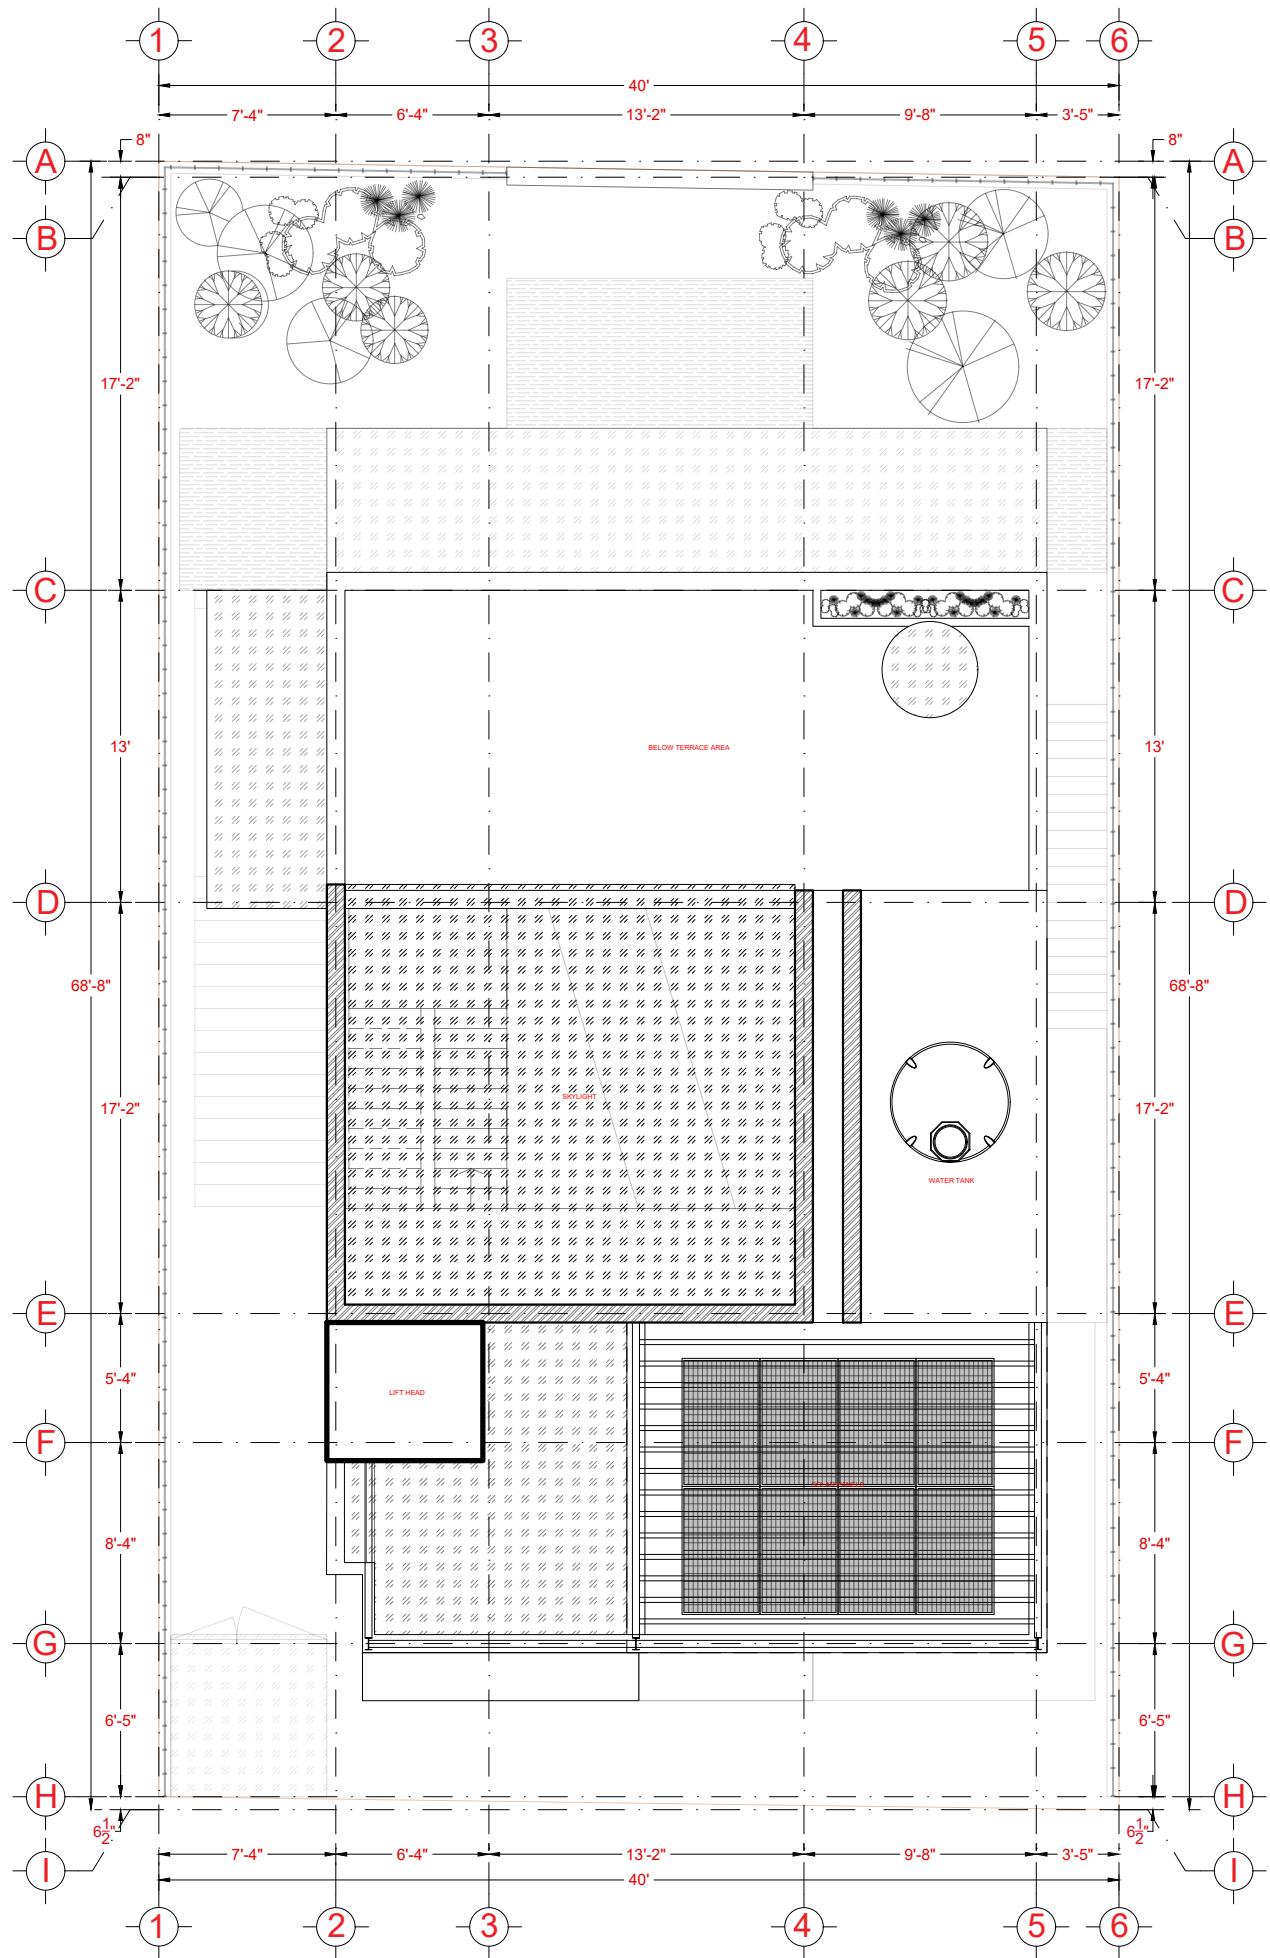

ROOF FLOOR PLAN




FRONT ELEVATION


SECTIONS

D. U. N. E


design unfiltered; a process never ending
54/2, 4th cross, Link road, Malleshwaram, Bangalore 560-003
designadune@gmail.com +91 23469351

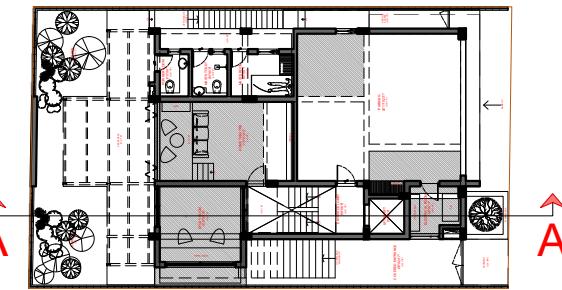


GROUND FLOOR PLAN

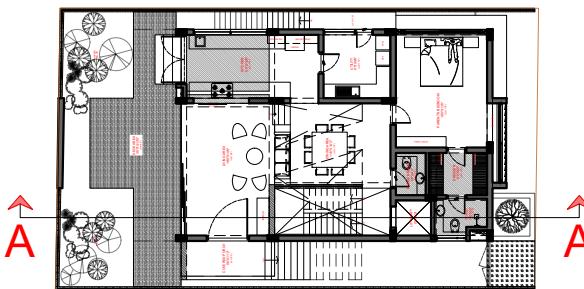


FIRST FLOOR PLAN

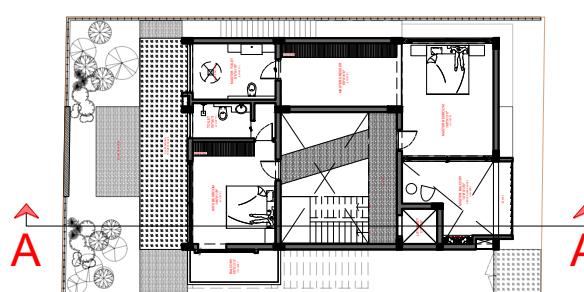


SECOND FLOOR PLAN

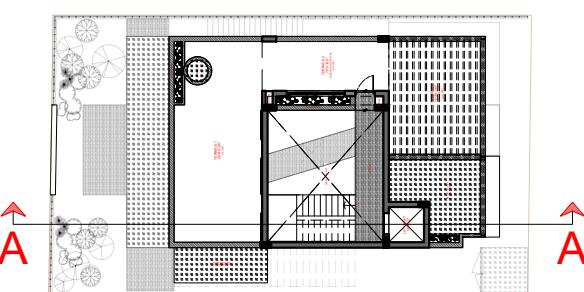

TERRACE FLOOR PLAN

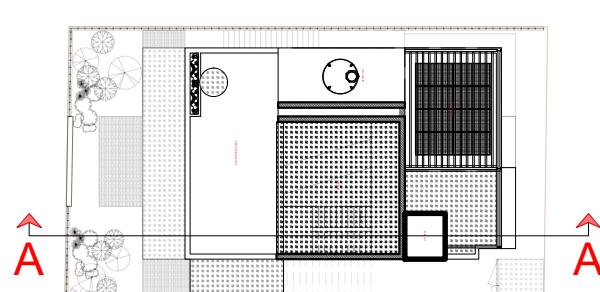

ROOF PLAN

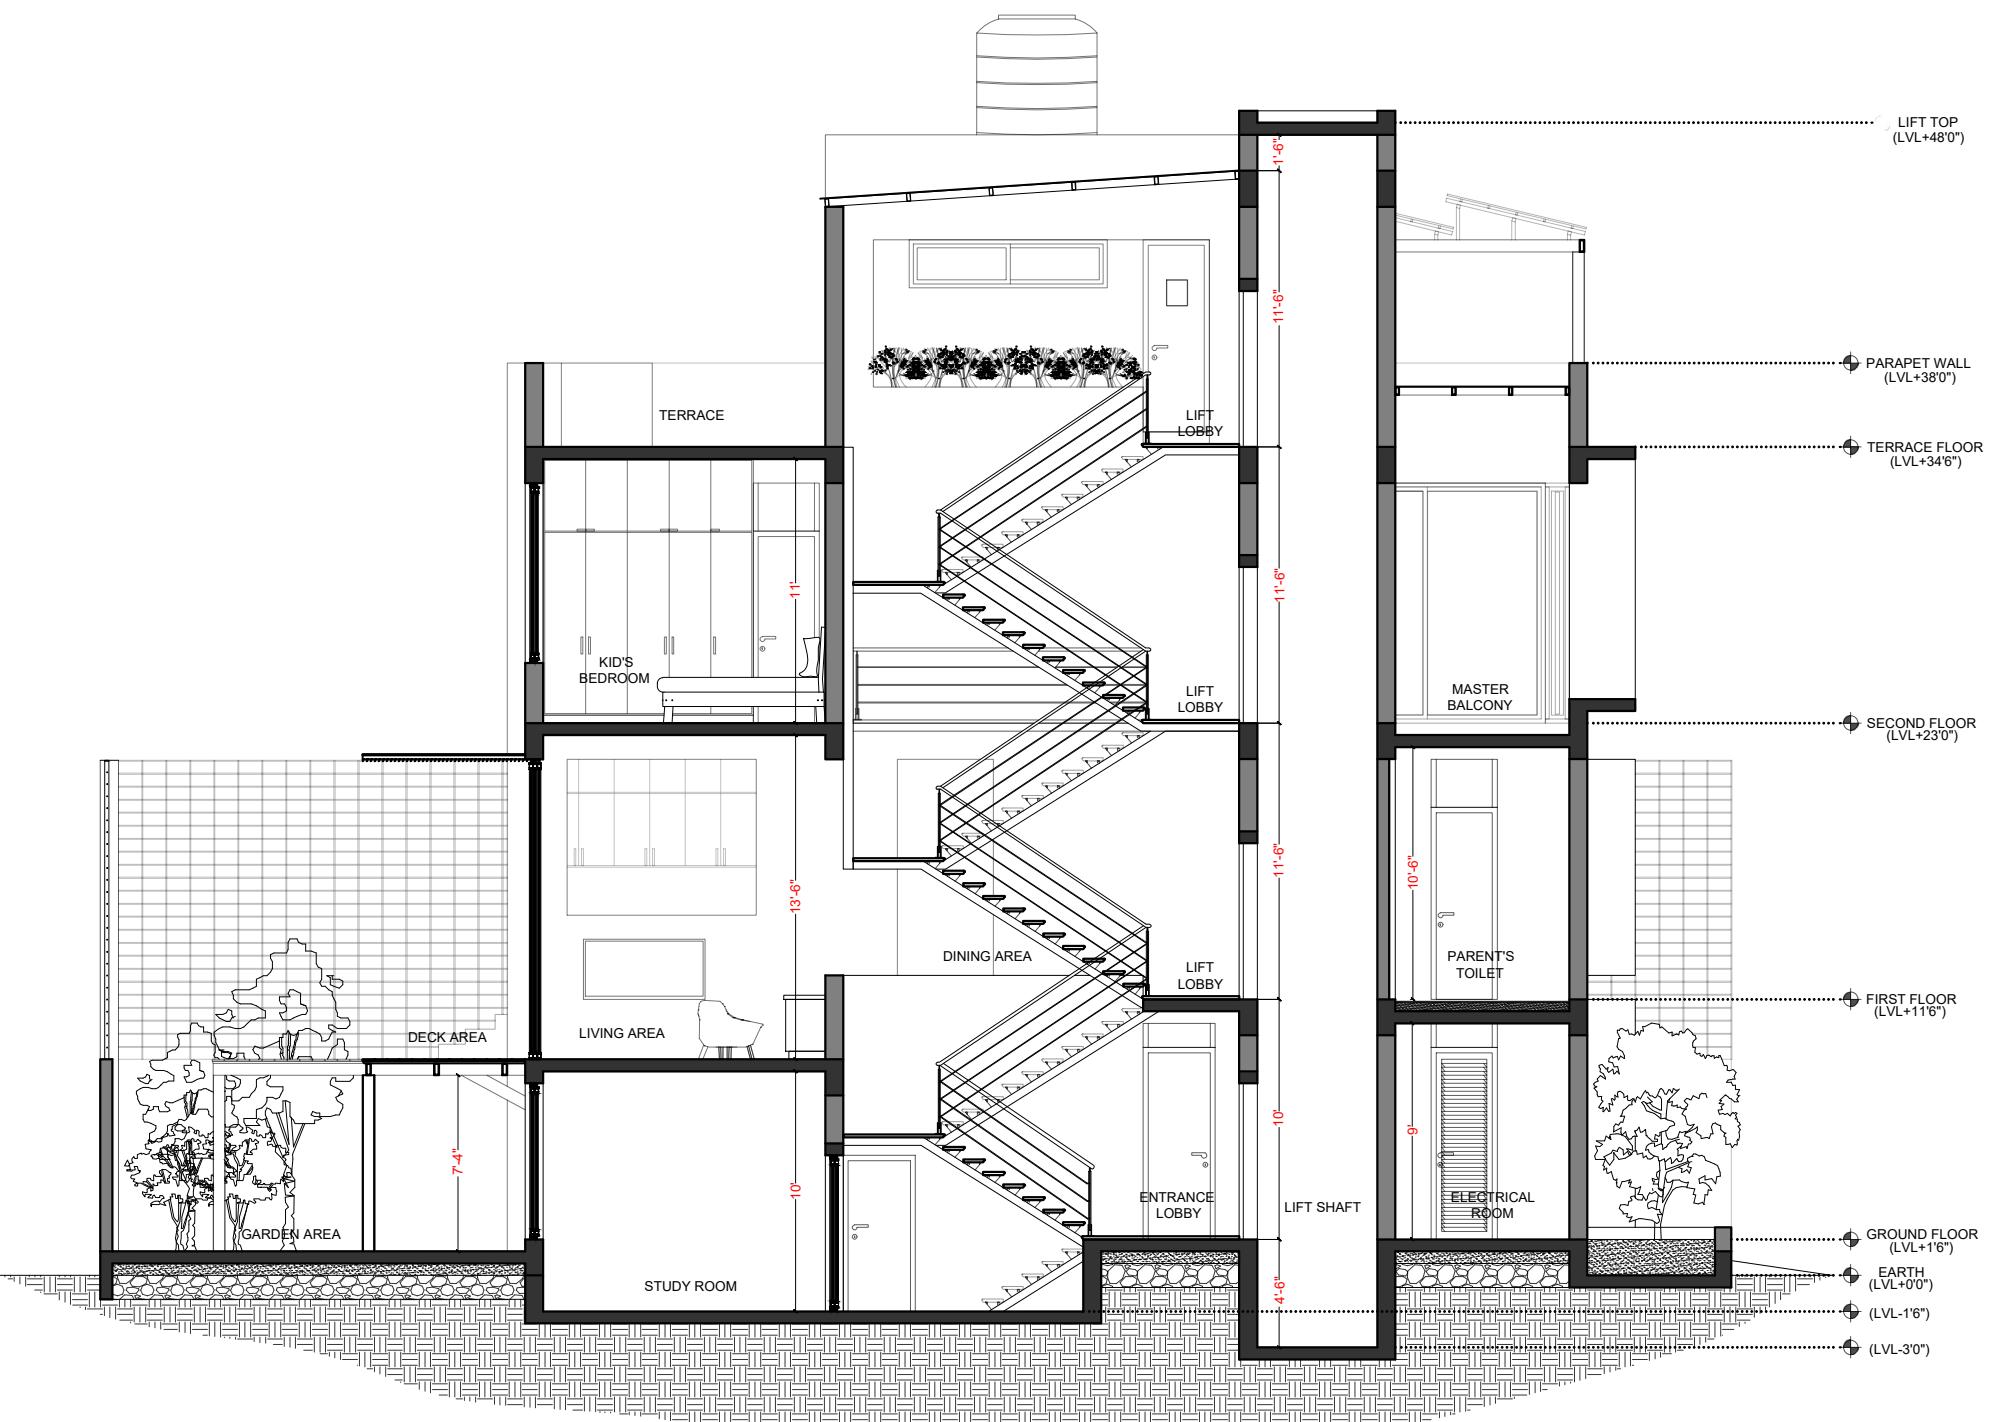

SECTION-AA

DATE 16 - 11 - 2022

SCALE $\frac{1}{8}$ " = 1'0"

PRINT ON A3

DRAWN BY JISHNU.K

CHECKED BY THEERTHAK

NOTE

PROJECT CODE SAR@S


DRAWING NUMBER WD-001

REVISION NUMBER 0




D. U. N. E


design unfiltered, a process never ending
54/2, 4th cross, Link road, Malleshwaram, Bangalore 560-003
designadune@gmail.com +91 23469351

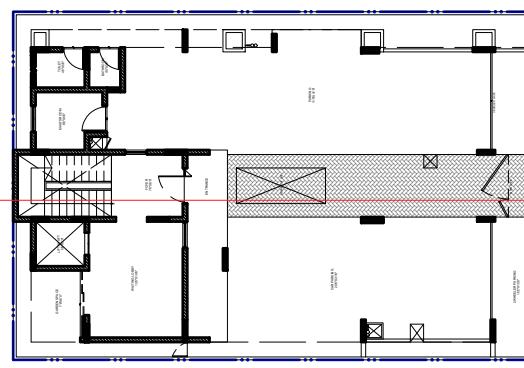


GROUND FLOOR PLAN

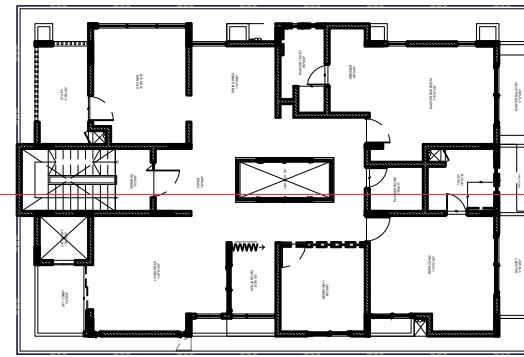


FIRST FLOOR PLAN

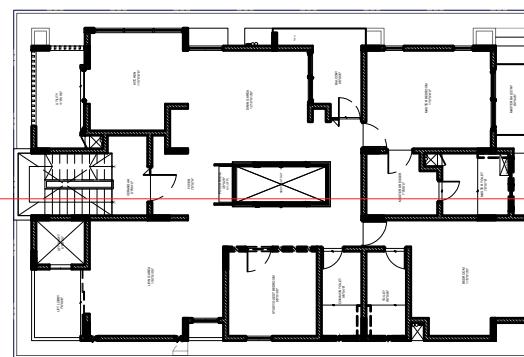


SECOND FLOOR PLAN

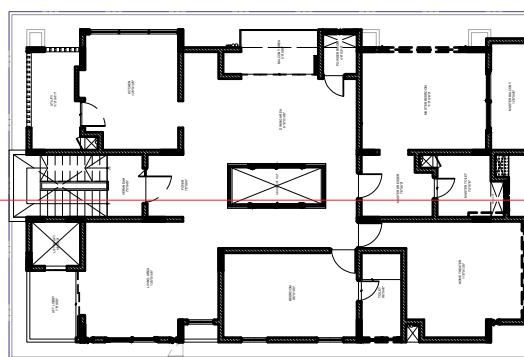

THIRD FLOOR PLAN

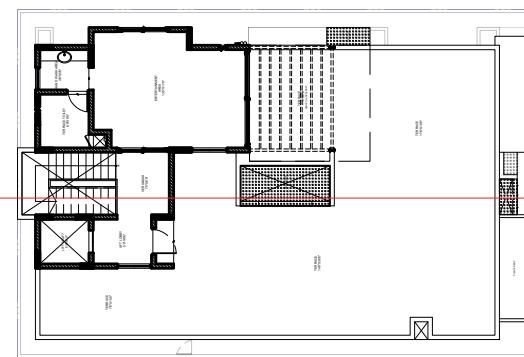

TERRACE FLOOR PLAN

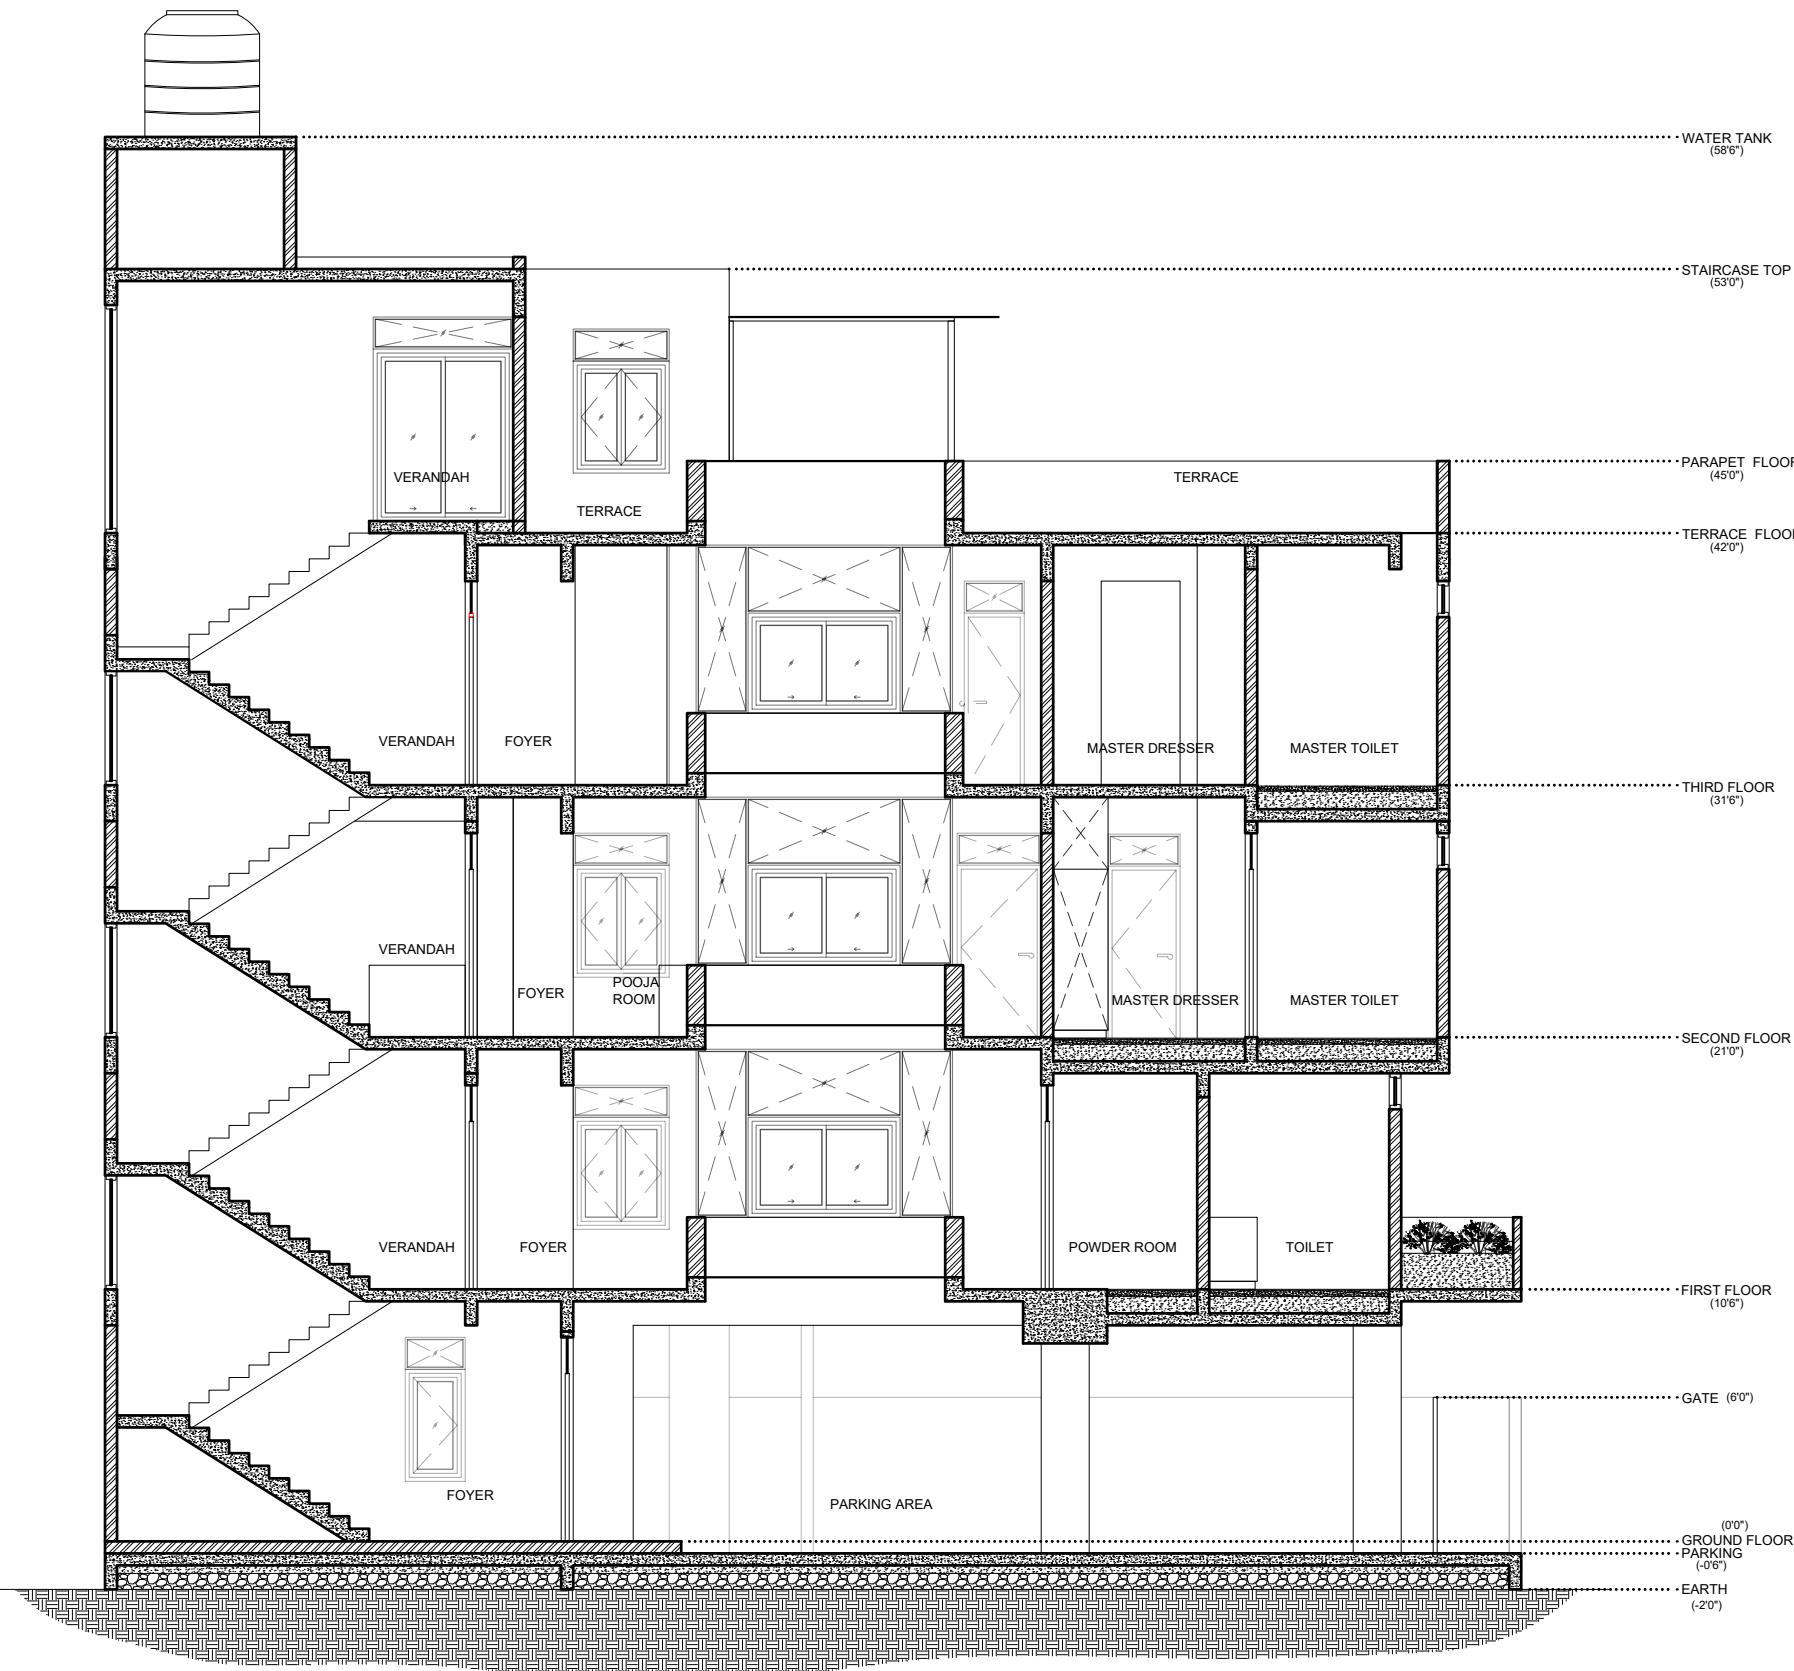

SECTION-AA

PROJECT

PROPOSED RESIDENCE
FOR AADHYA ATG

DRAWING TITLE

WORKING DRAWING

DRAWING TITLE

SECTION-AA

DATE 16 - 11 - 2022

SCALE 1" = 1'0"

PRINT ON A3

DRAWN BY JISHNU.K

CHECKED BY THEERTHAK

NOTE

GROUND FLOOR AREA
=1776 SQFT

FIRST FLOOR AREA
=1929 SQFT

PROJECT CODE

AATG

DRAWING NUMBER

WD-004


REVISION NUMBER

0




D. U. N. E


design unfiltered, a process never ending
54/2, 4th cross, Link road, Malleshwaram, Bangalore 560-003
designadune@gmail.com +91 23469351

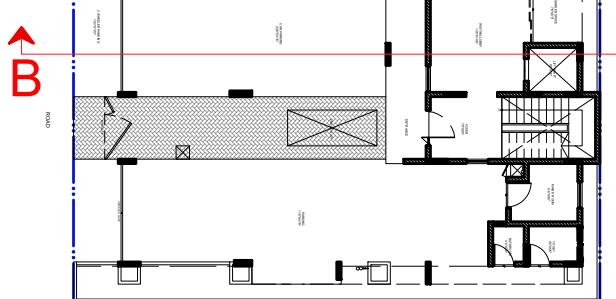


GROUND FLOOR PLAN

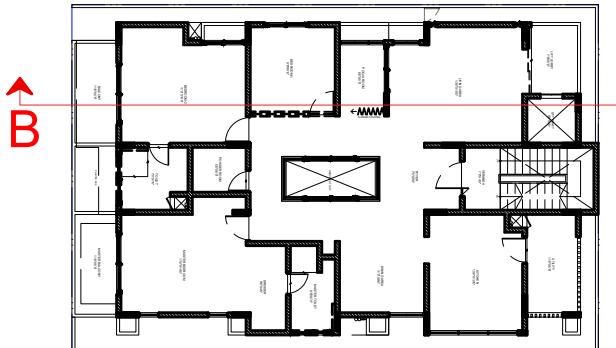


FIRST FLOOR PLAN

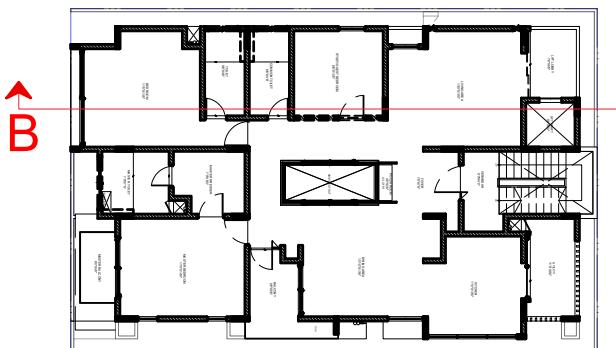


SECOND FLOOR PLAN

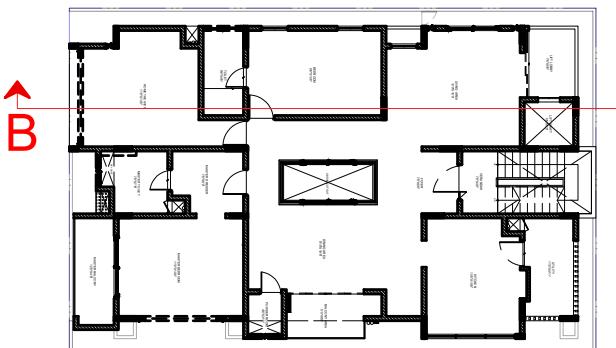

THIRD FLOOR PLAN

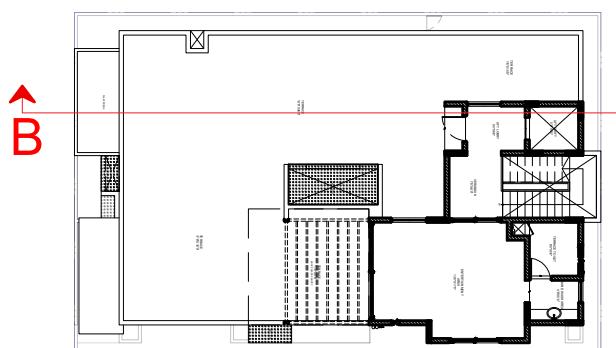

TERRACE FLOOR PLAN

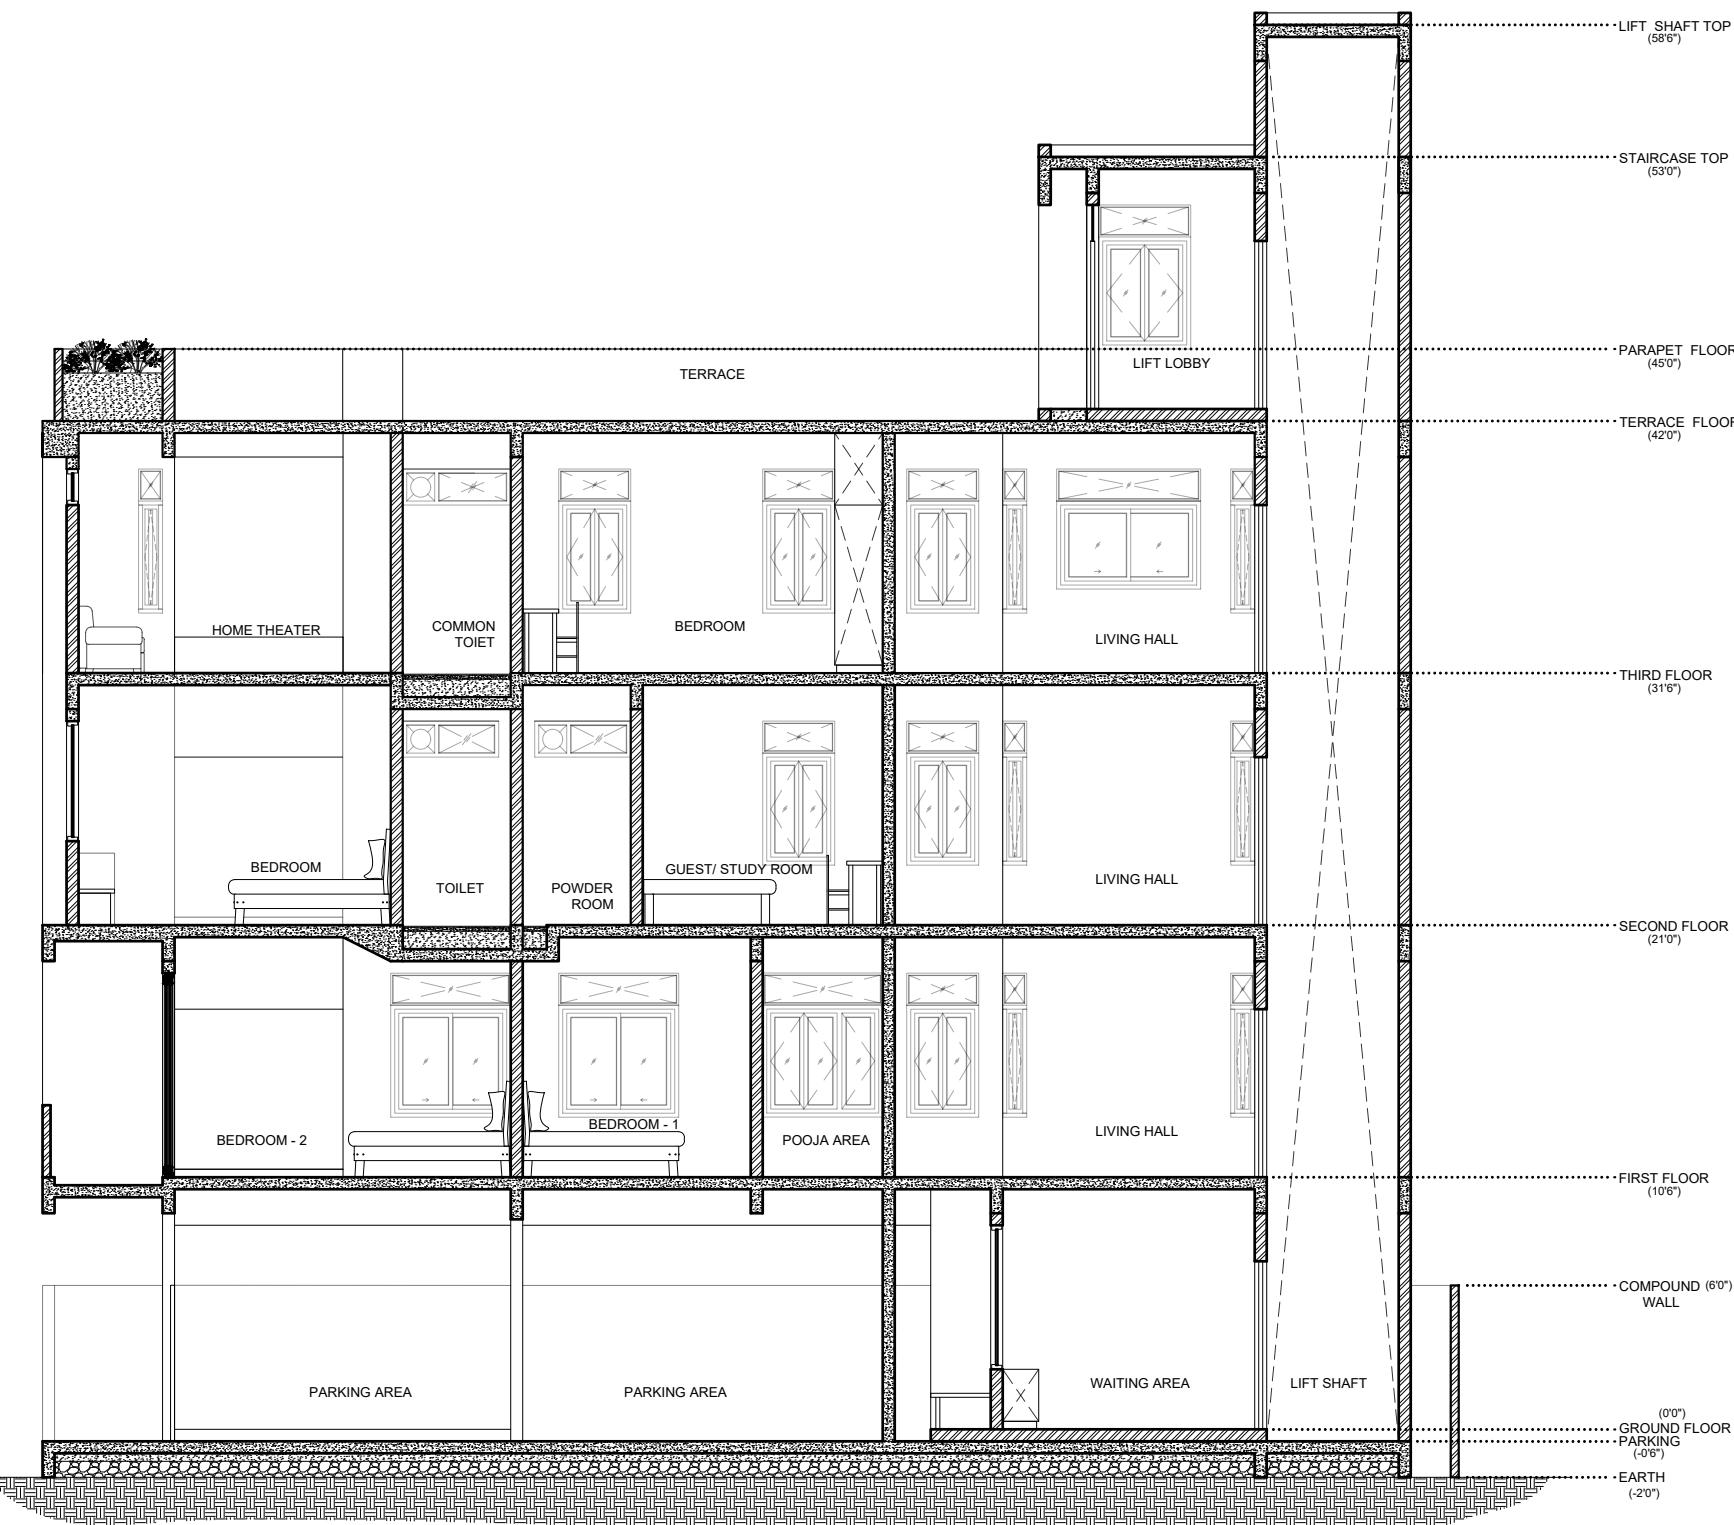

SECTION-BB

PROJECT
PROPOSED RESIDENCE
FOR AADHYA ATG

DRAWING TITLE
WORKING DRAWING

DRAWING TITLE
SECTION-BB

DATE 16 - 11 - 2022
SCALE 1" = 1'0"
PRINT ON A3
DRAWN BY JISHNU.K
CHECKED BY THEERTHAK

NOTE
GROUND FLOOR AREA
=1776 SQFT

FIRST FLOOR AREA
=1929 SQFT

PROJECT CODE AATG
DRAWING NUMBER WD-005
REVISION NUMBER 0



D. U. N. E

design unfiltered, a process never ending
54/2, 4th cross, Link road, Malleshwaram, Bangalore 560-003
designadune@gmail.com +91 23469351

PROJECT

PROPOSED RESIDENCE
FOR AADHYA ATG

DRAWING TITLE

WORKING DRAWING

DRAWING TITLE

SECTION-CC, SECTION-DD

DATE 16 - 11 - 2022

SCALE $\frac{1}{8}$ = 1'0"

PRINT ON A3

DRAWN BY JISHNU.K

CHECKED BY THEERTHAK

NOTE








GROUND FLOOR AREA
=1776 SQFT

FIRST FLOOR AREA
=1929 SQFT

PROJECT CODE AATG

DRAWING NUMBER WD-006

REVISION NUMBER 0

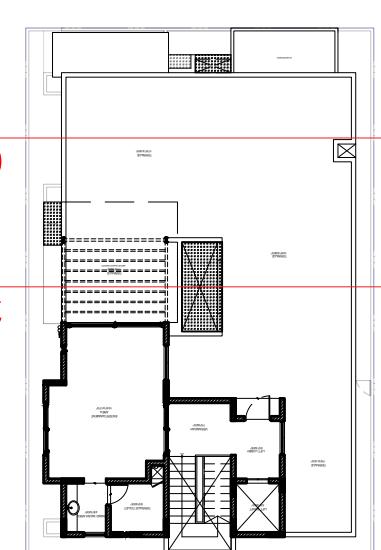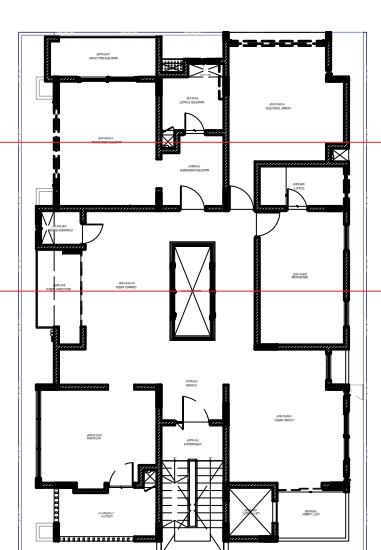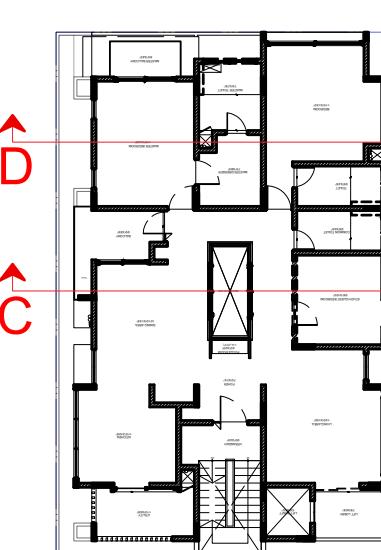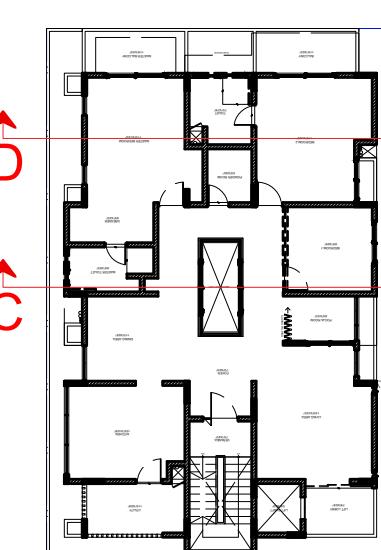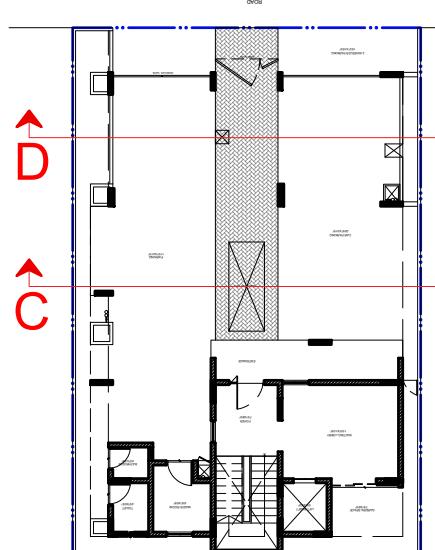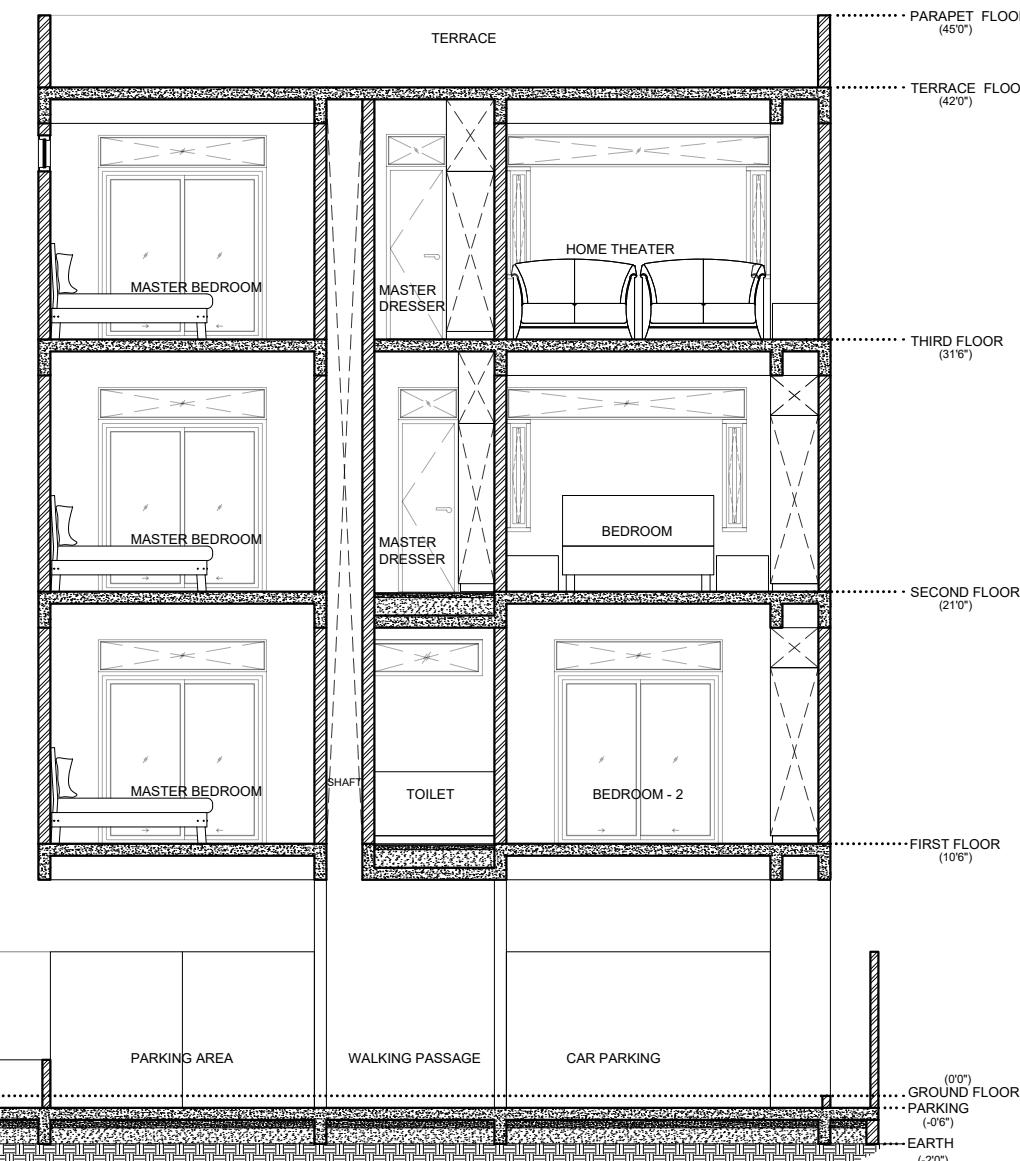
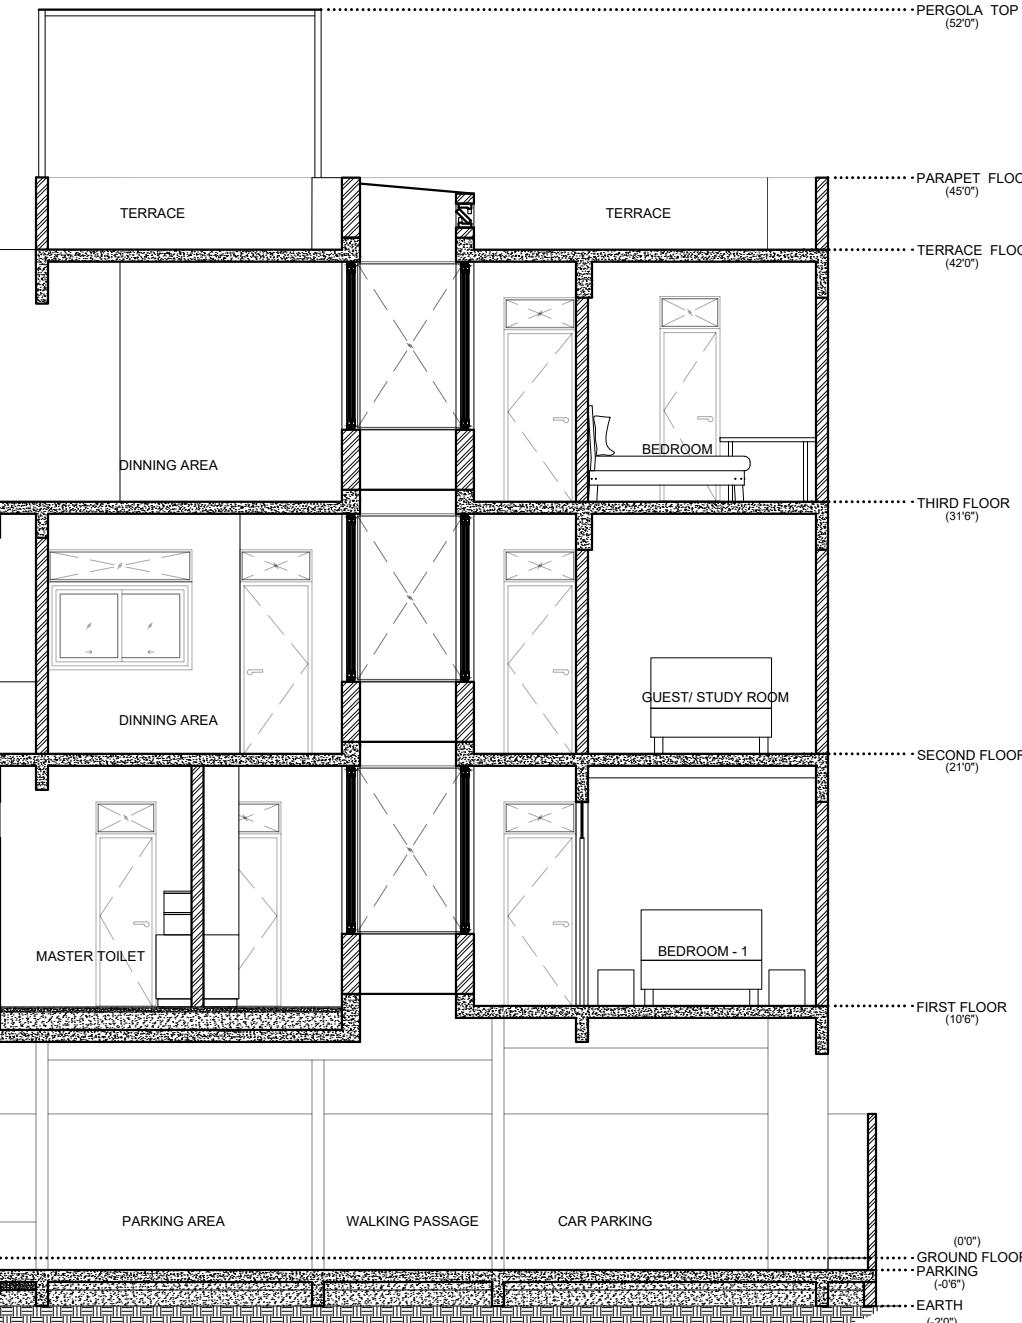


WORKING DRAWING

D. U. N. E

design unfiltered, a process never ending

54/2, 4th cross, Link road, Malleshwaram, Bangalore 560-003
designadune@gmail.com +91 23469351

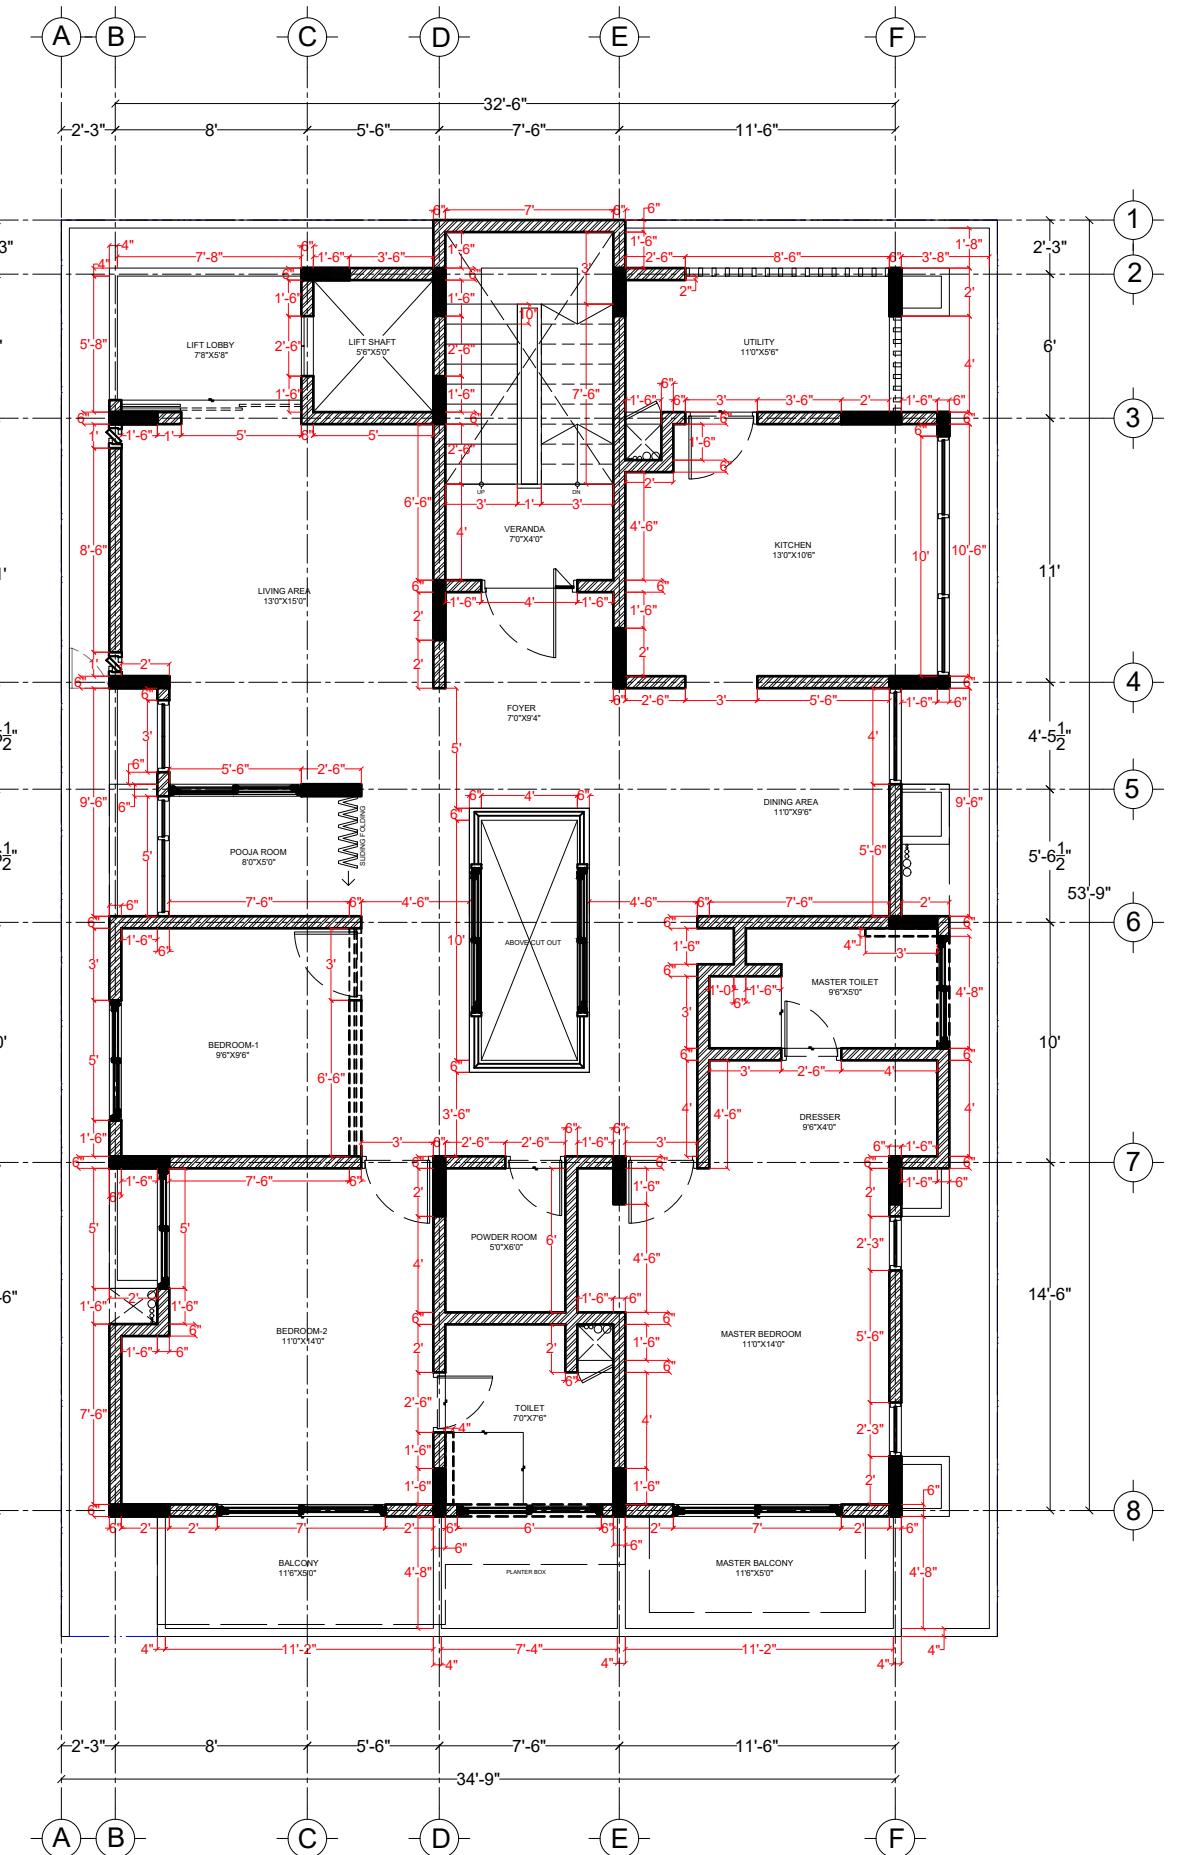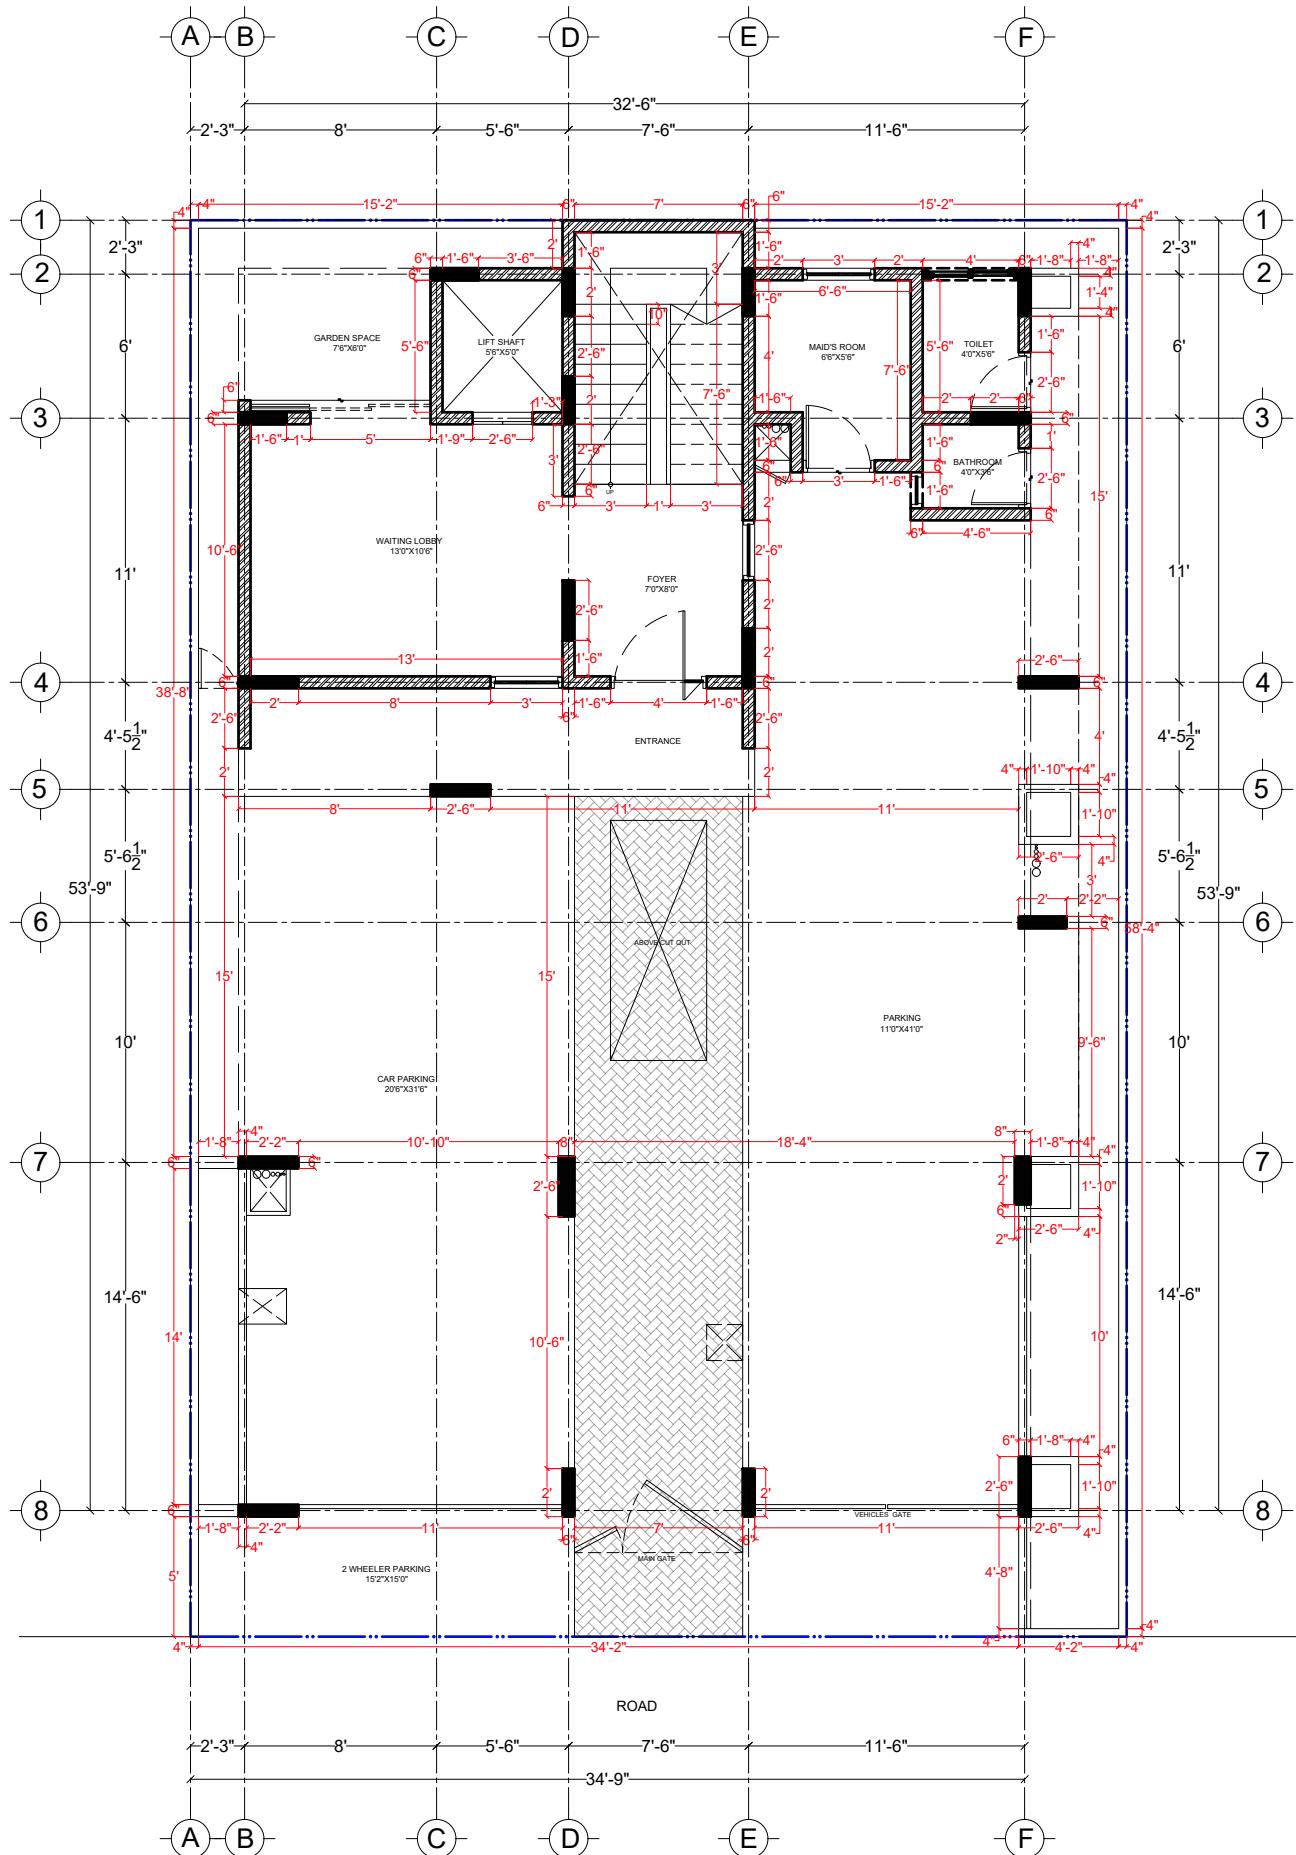

PROJECT

PROPOSED RESIDENCE
FOR AADHYA ATG

DRAWING TITLE

WORKING DRAWING

DRAWING TITLE

GROUND AND FIRST
FLOOR PLAN

DATE

16 - 11 - 2022

SCALE

1" = 1'0"

PRINT ON

A3

DRAWN BY

JISHNU.K

CHECKED BY

THEERTHAK

NOTE

GROUND FLOOR AREA
=1776 SQFT

FIRST FLOOR AREA

=1929 SQFT

PROJECT CODE

AATG

DRAWING NUMBER

WD-001


REVISION NUMBER

0




D. U. N. E

design unfiltered, a process never ending
54/2, 4th cross, Link road, Malleshwaram, Bangalore 560-003
designadune@gmail.com +91 23469351

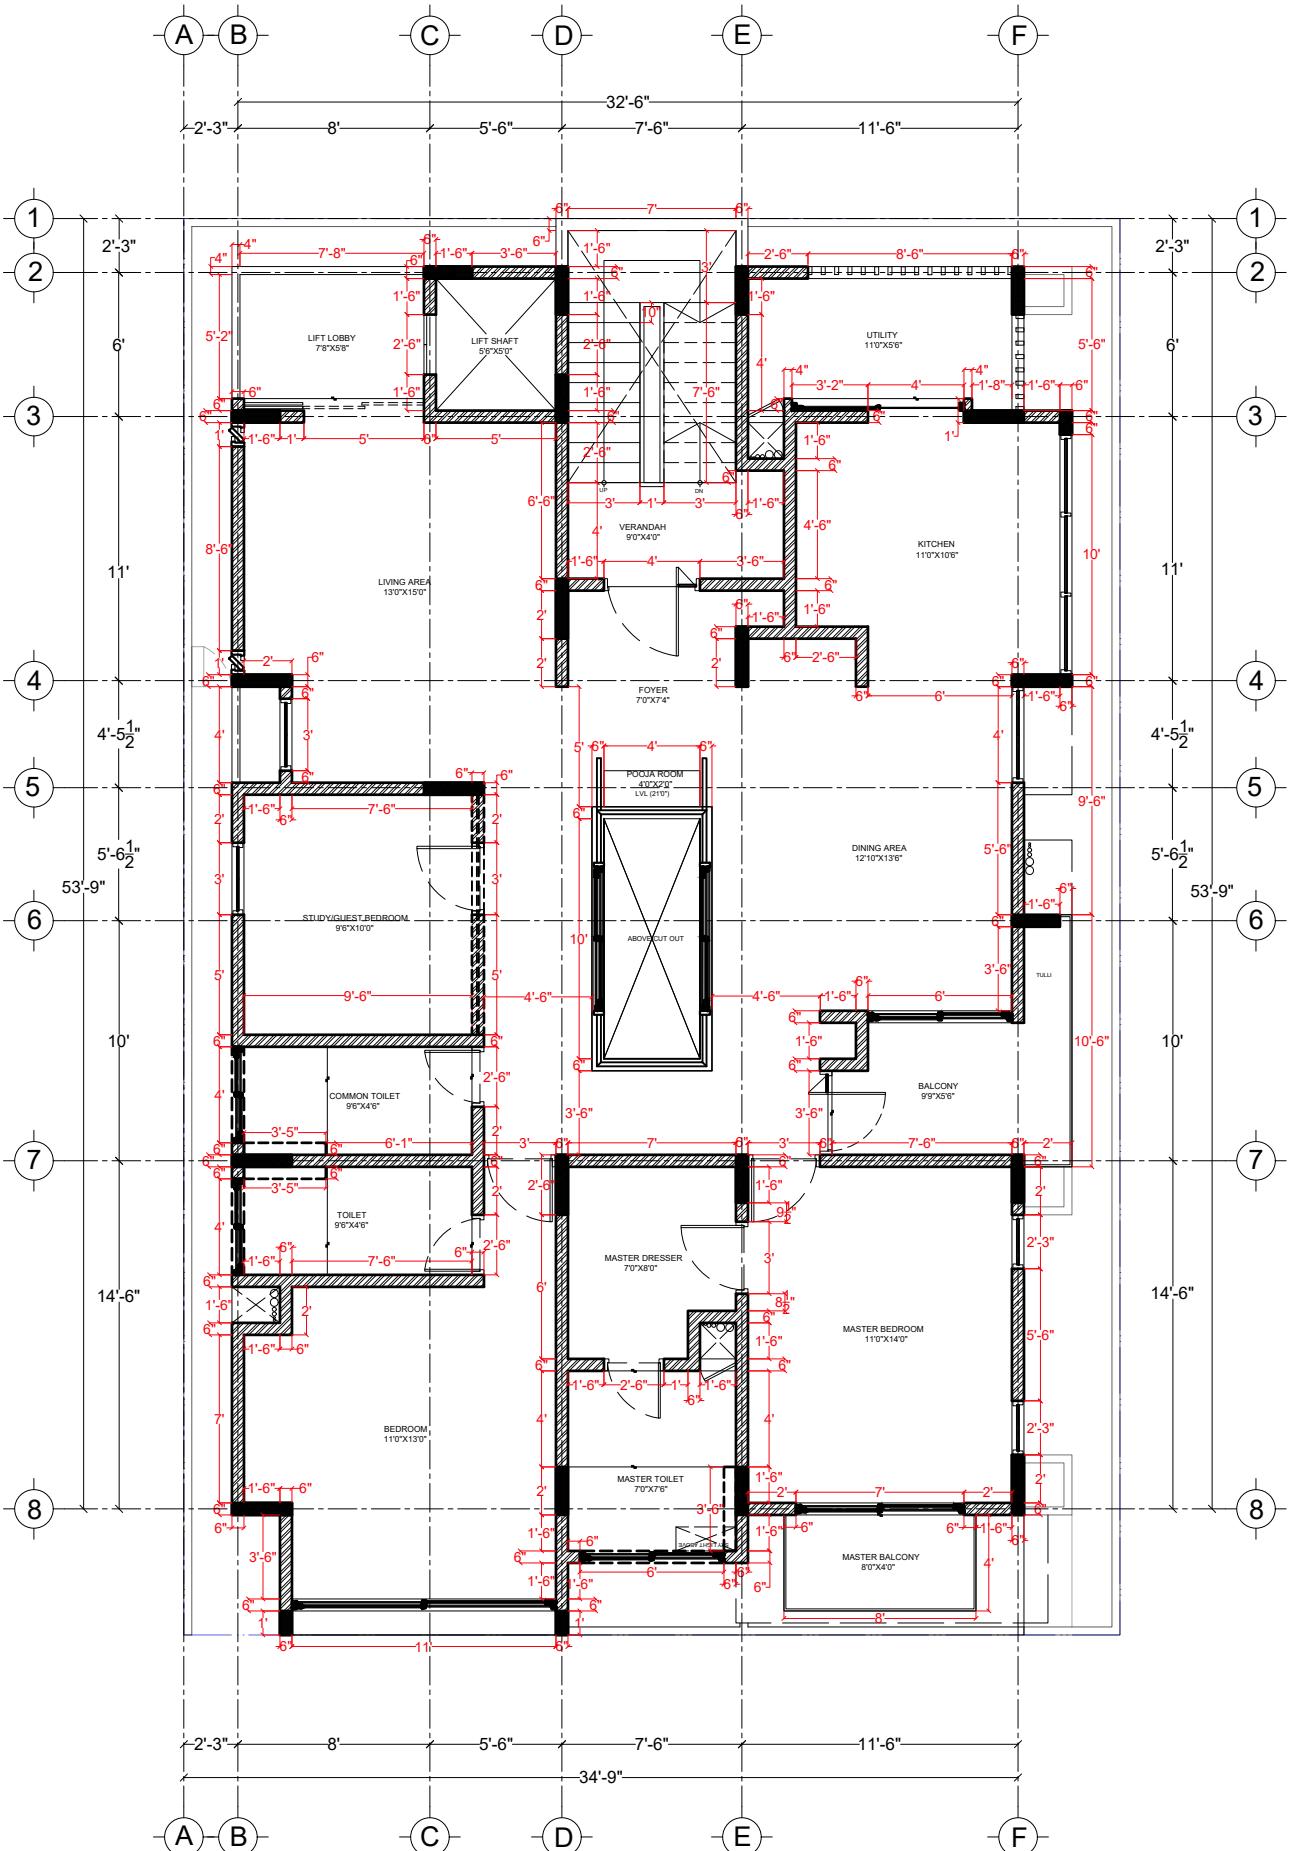

SECOND FLOOR PLAN

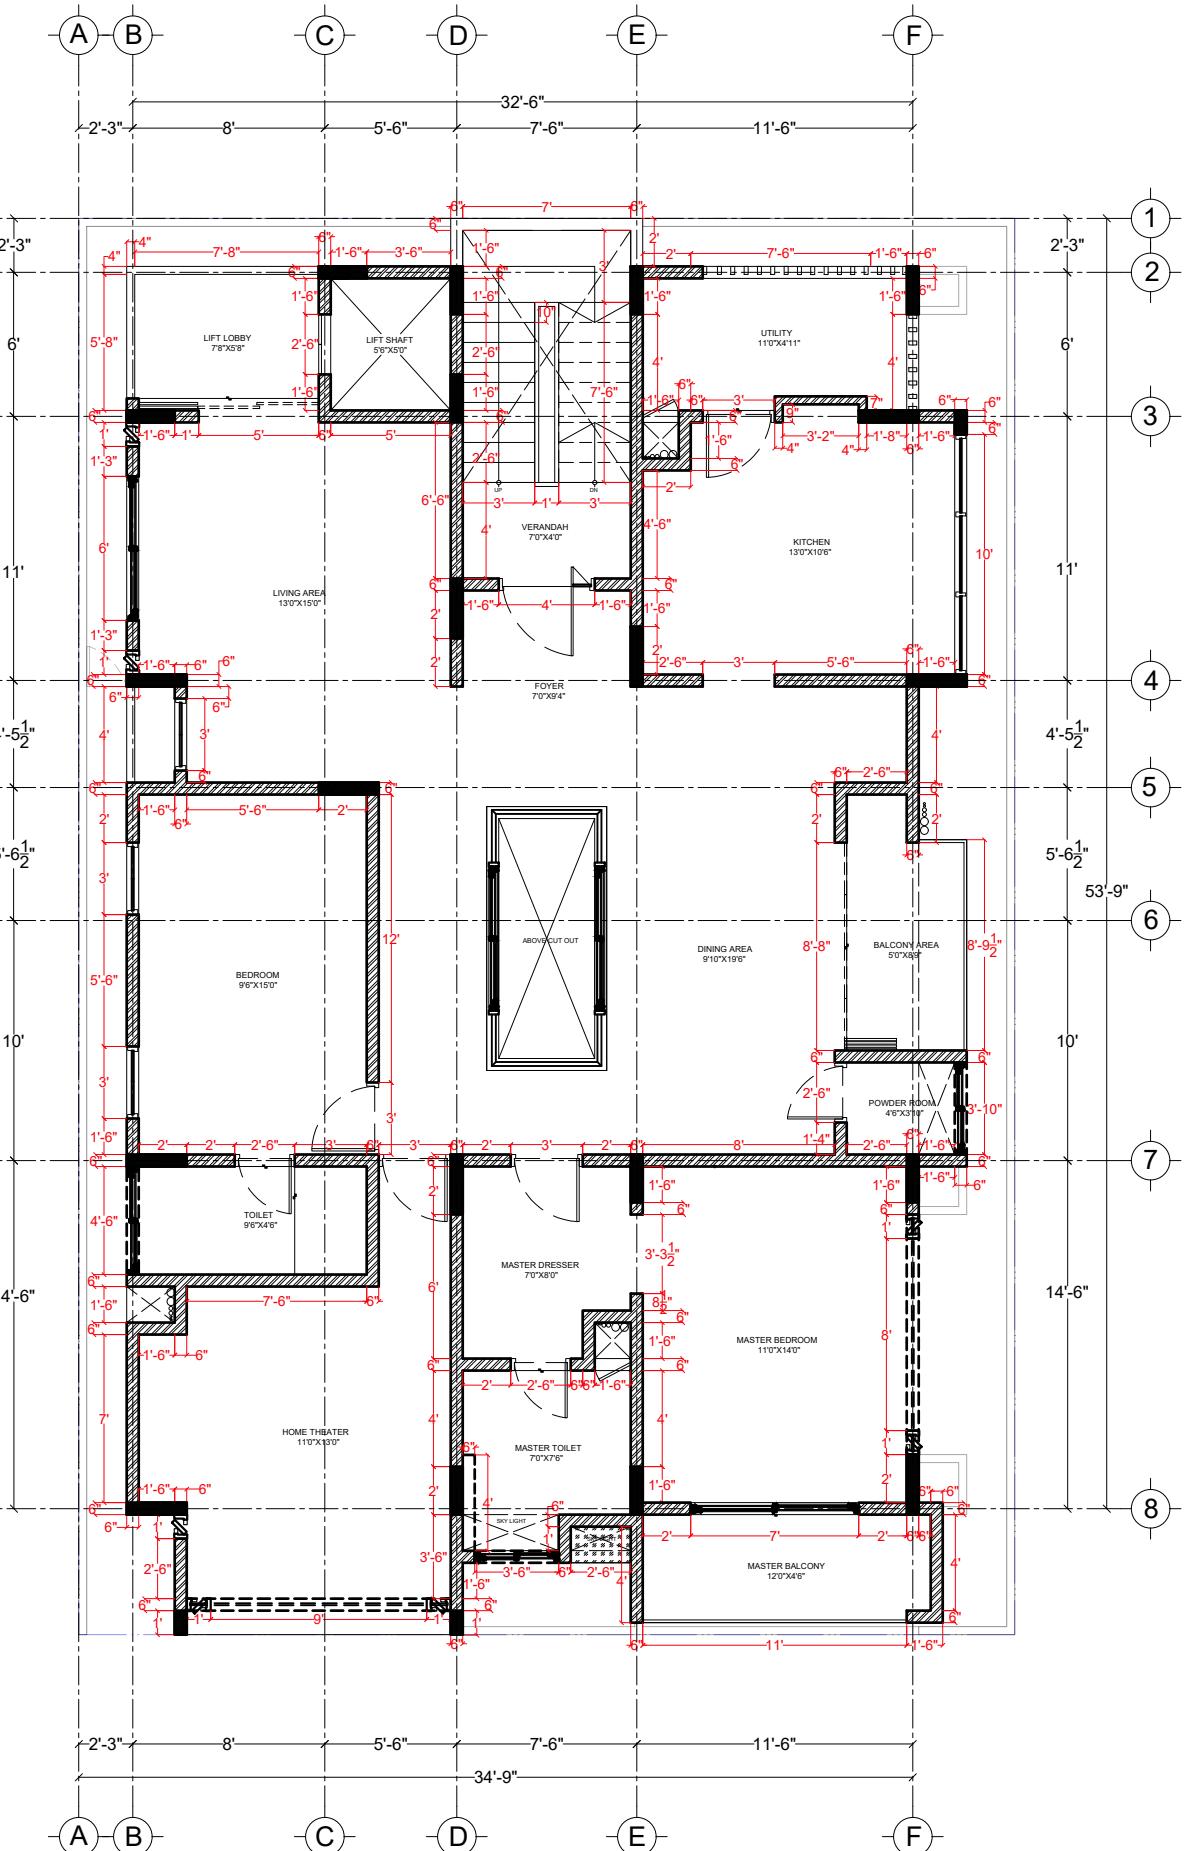

THIRD FLOOR PLAN

PROJECT

PROPOSED RESIDENCE
FOR AADHYA ATG

DRAWING TITLE

WORKING DRAWING

DRAWING TITLE

SECOND AND THIRD
FLOOR PLAN

DATE

16 - 11 - 2022
1" = 1'0"

SCALE

A3

PRINT ON

JISHNU.K
THEERTHAK

CHECKED BY

NOTE
SECOND FLOOR AREA
=1880 SQFT

THIRD FLOOR AREA
=1909 SQFT

PROJECT CODE

AATG

DRAWING NUMBER

WD-002


REVISION NUMBER

0



D. U. N. E

design unfiltered; a process never ending
54/2, 4th cross, Link road, Malleshwaram, Bangalore 560-003
designadune@gmail.com +91 23469351

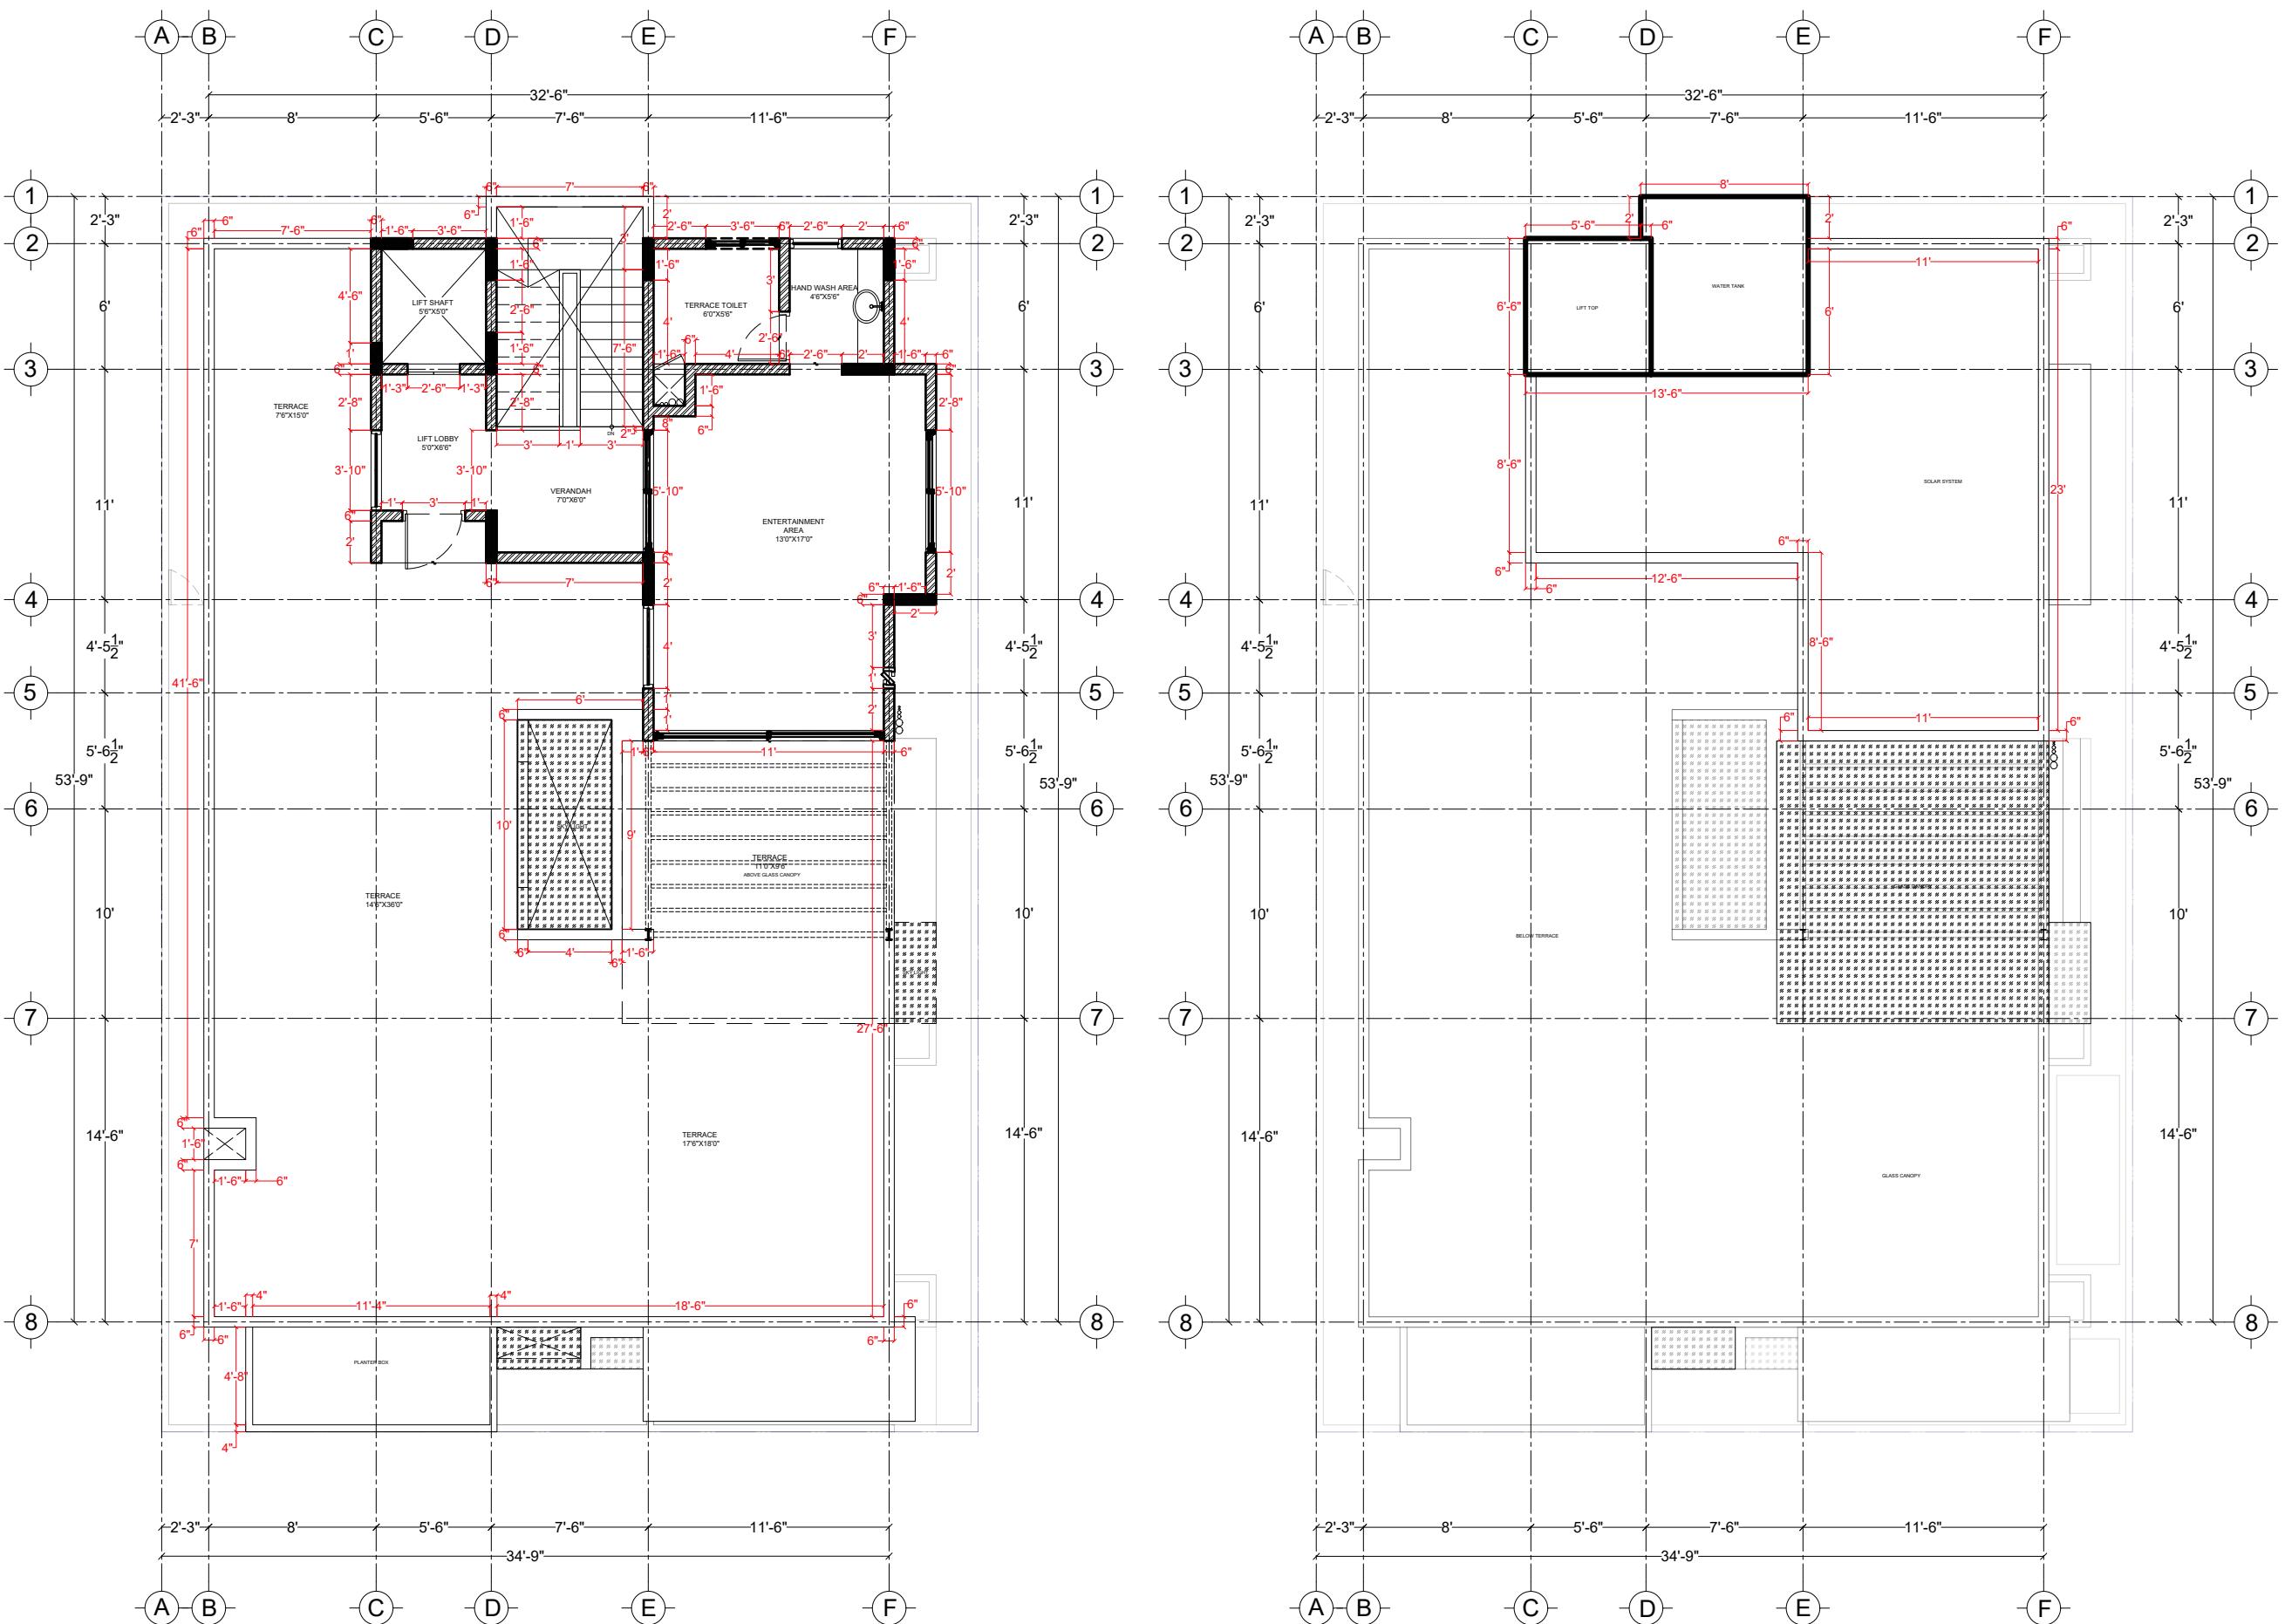

PROJECT

PROPOSED RESIDENCE
FOR AADHYA ATG

DRAWING TITLE

WORKING DRAWING

DRAWING TITLE

TERRACE AND ROOF
FLOOR PLAN

DATE 16 - 11 - 2022

SCALE 1" = 1'0"

PRINT ON A3

DRAWN BY JISHNU.K

CHECKED BY THEERTHAK

NOTE

TERRACE FLOOR AREA
=1783 SQFT

ROOF AREA
=506 SQFT

PROJECT CODE AATG

DRAWING NUMBER WD-003

REVISION NUMBER 0



TERRACE FLOOR PLAN

ROOF PLAN

ELECTRICAL DRAWING

D. U. N. E

design unfiltered, a process never ending

54/2, 4th cross, Link road, Malleshwaram, Bangalore 560-003
designadune@gmail.com +91 23469351

PROJECT

PROPOSED RESIDENCE
FOR AADHYA ATG

DRAWING TITLE

WORKING DRAWING

DRAWING TITLE

GROUND AND FIRST
ELECTRICAL DRAWING

DATE 16 - 11 - 2022

SCALE 1" = 1'0"

PRINT ON A3

DRAWN BY JISHNU.K

CHECKED BY THEERTHAK

NOTE


GROUND FLOOR AREA
=1776 SQFT

FIRST FLOOR AREA
=1929 SQFT


PROJECT CODE AATG

DRAWING NUMBER WD-001

REVISION NUMBER 0

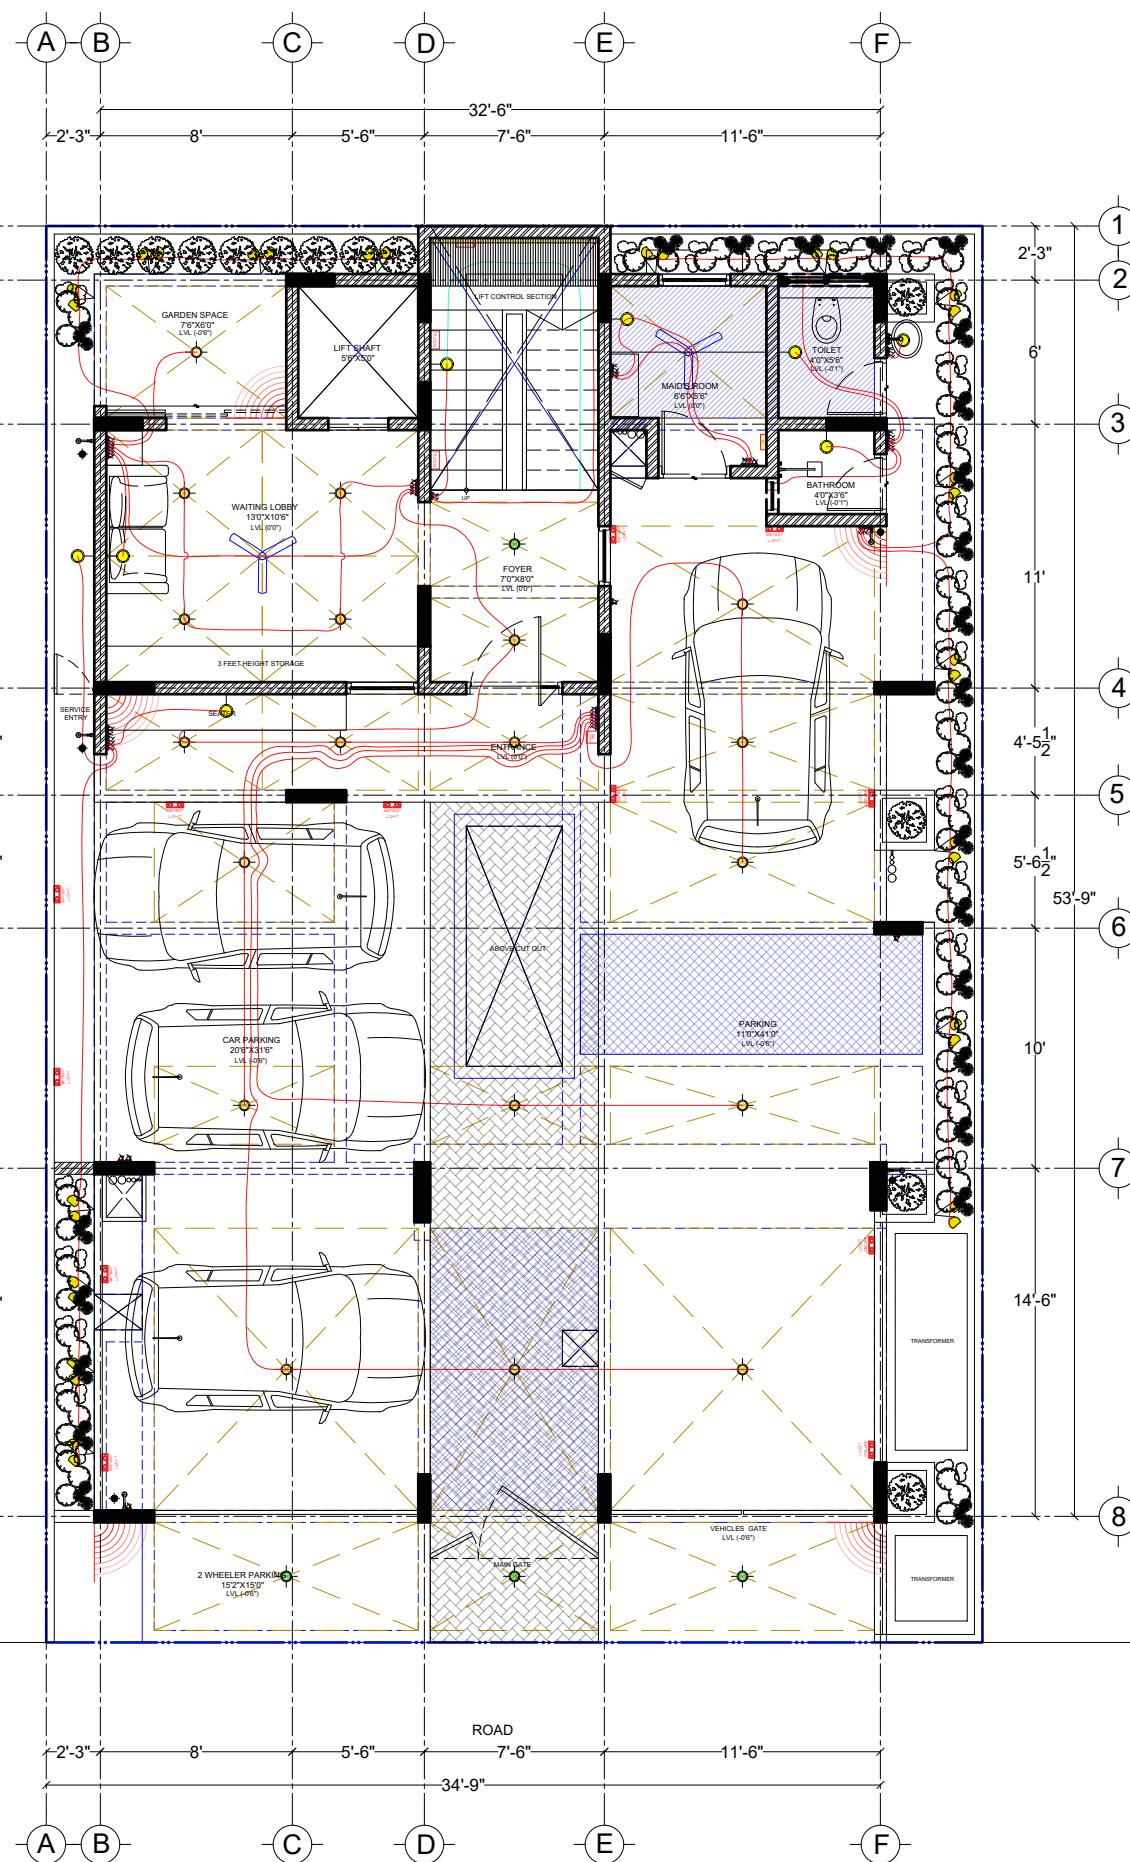

GROUND FLOOR PLAN

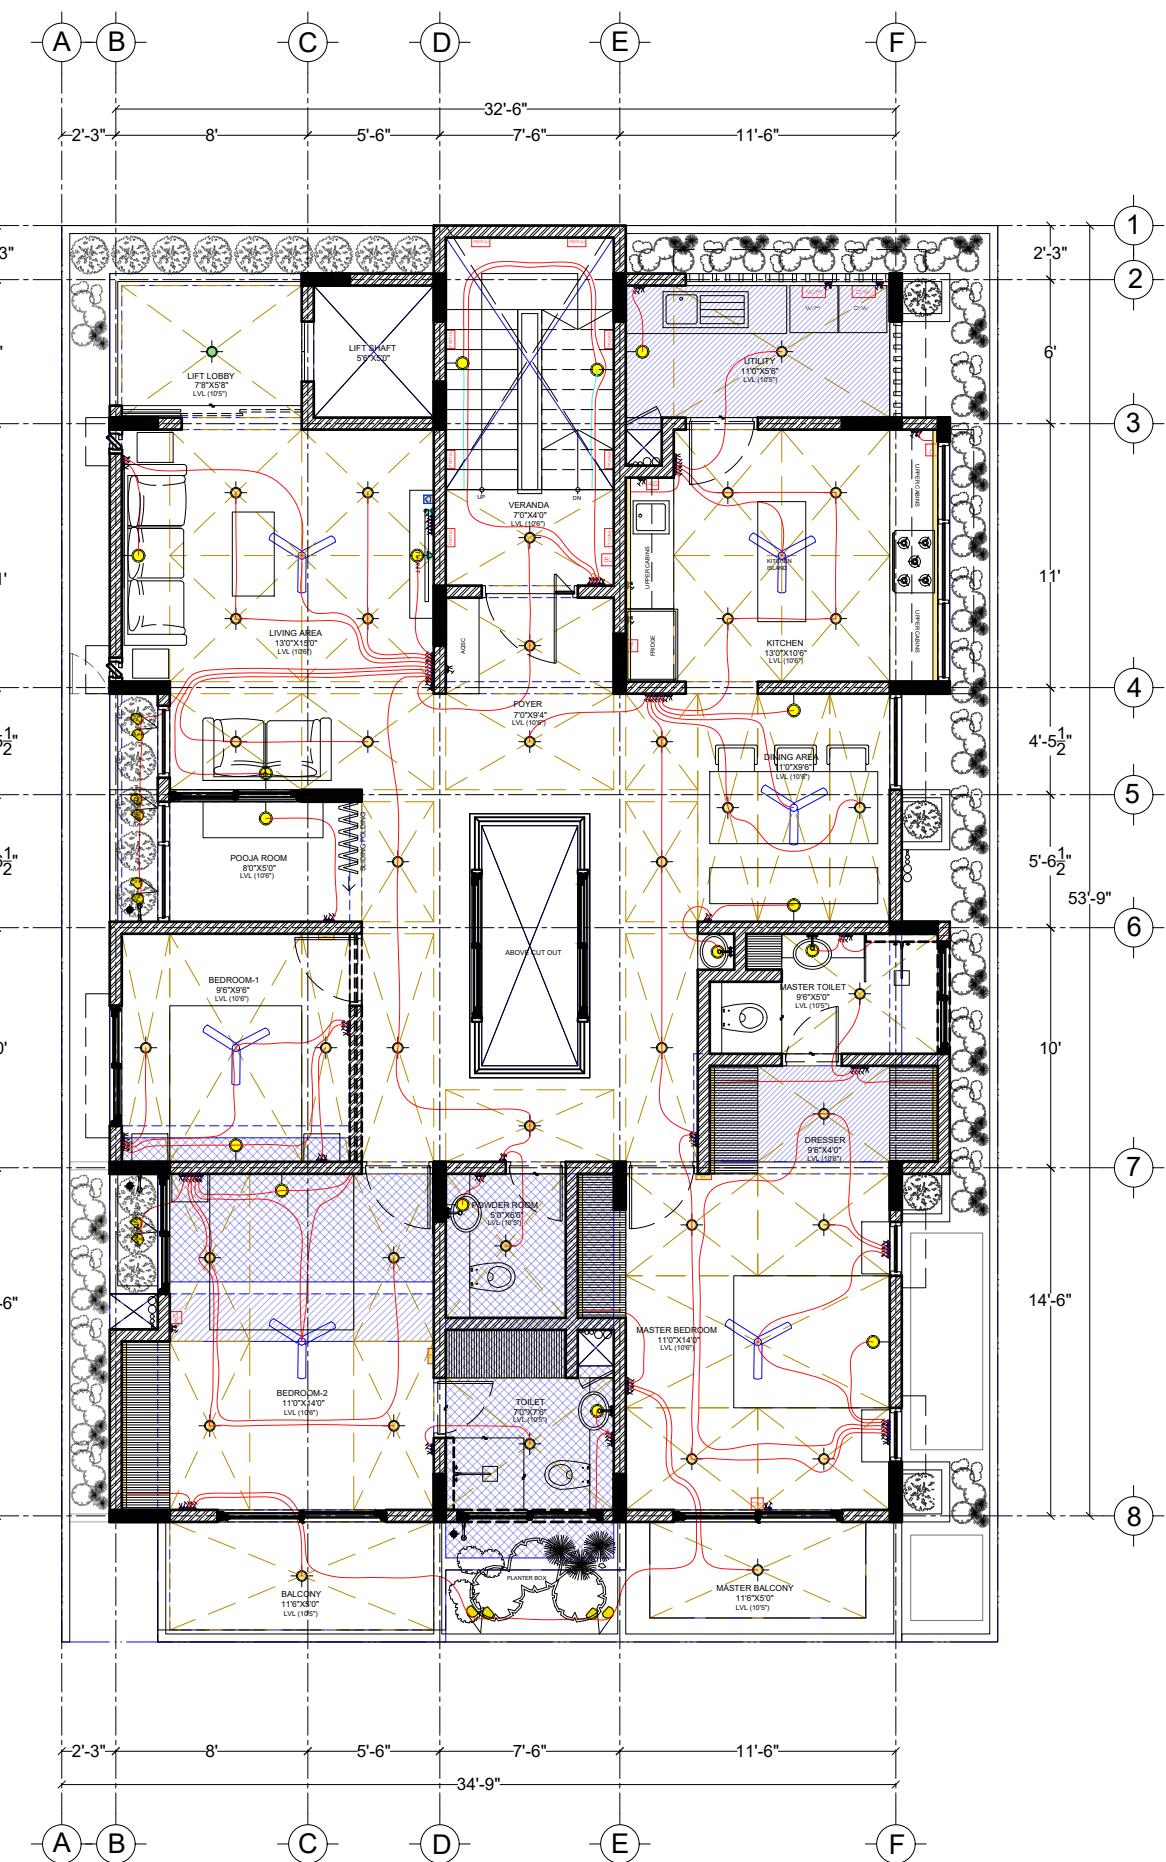

FIRST FLOOR PLAN

D. U. N. E

design unfiltered, a process never ending

54/2, 4th cross, Link road, Malleshwaram, Bangalore 560-003
designadune@gmail.com +91 23469351

PROJECT

PROPOSED RESIDENCE
FOR AADHYA ATG

DRAWING TITLE

WORKING DRAWING

DRAWING TITLE

SECOND AND THIRD
ELECTRICAL DRAWING

DATE 16 - 11 - 2022

SCALE 1" = 1'0"

PRINT ON A3

DRAWN BY JISHNU.K

CHECKED BY THEERTHAK

NOTE



SECOND FLOOR AREA
=1880 SQFT

THIRD FLOOR AREA
=1909 SQFT

PROJECT CODE AATG

DRAWING NUMBER WD-001

REVISION NUMBER 0

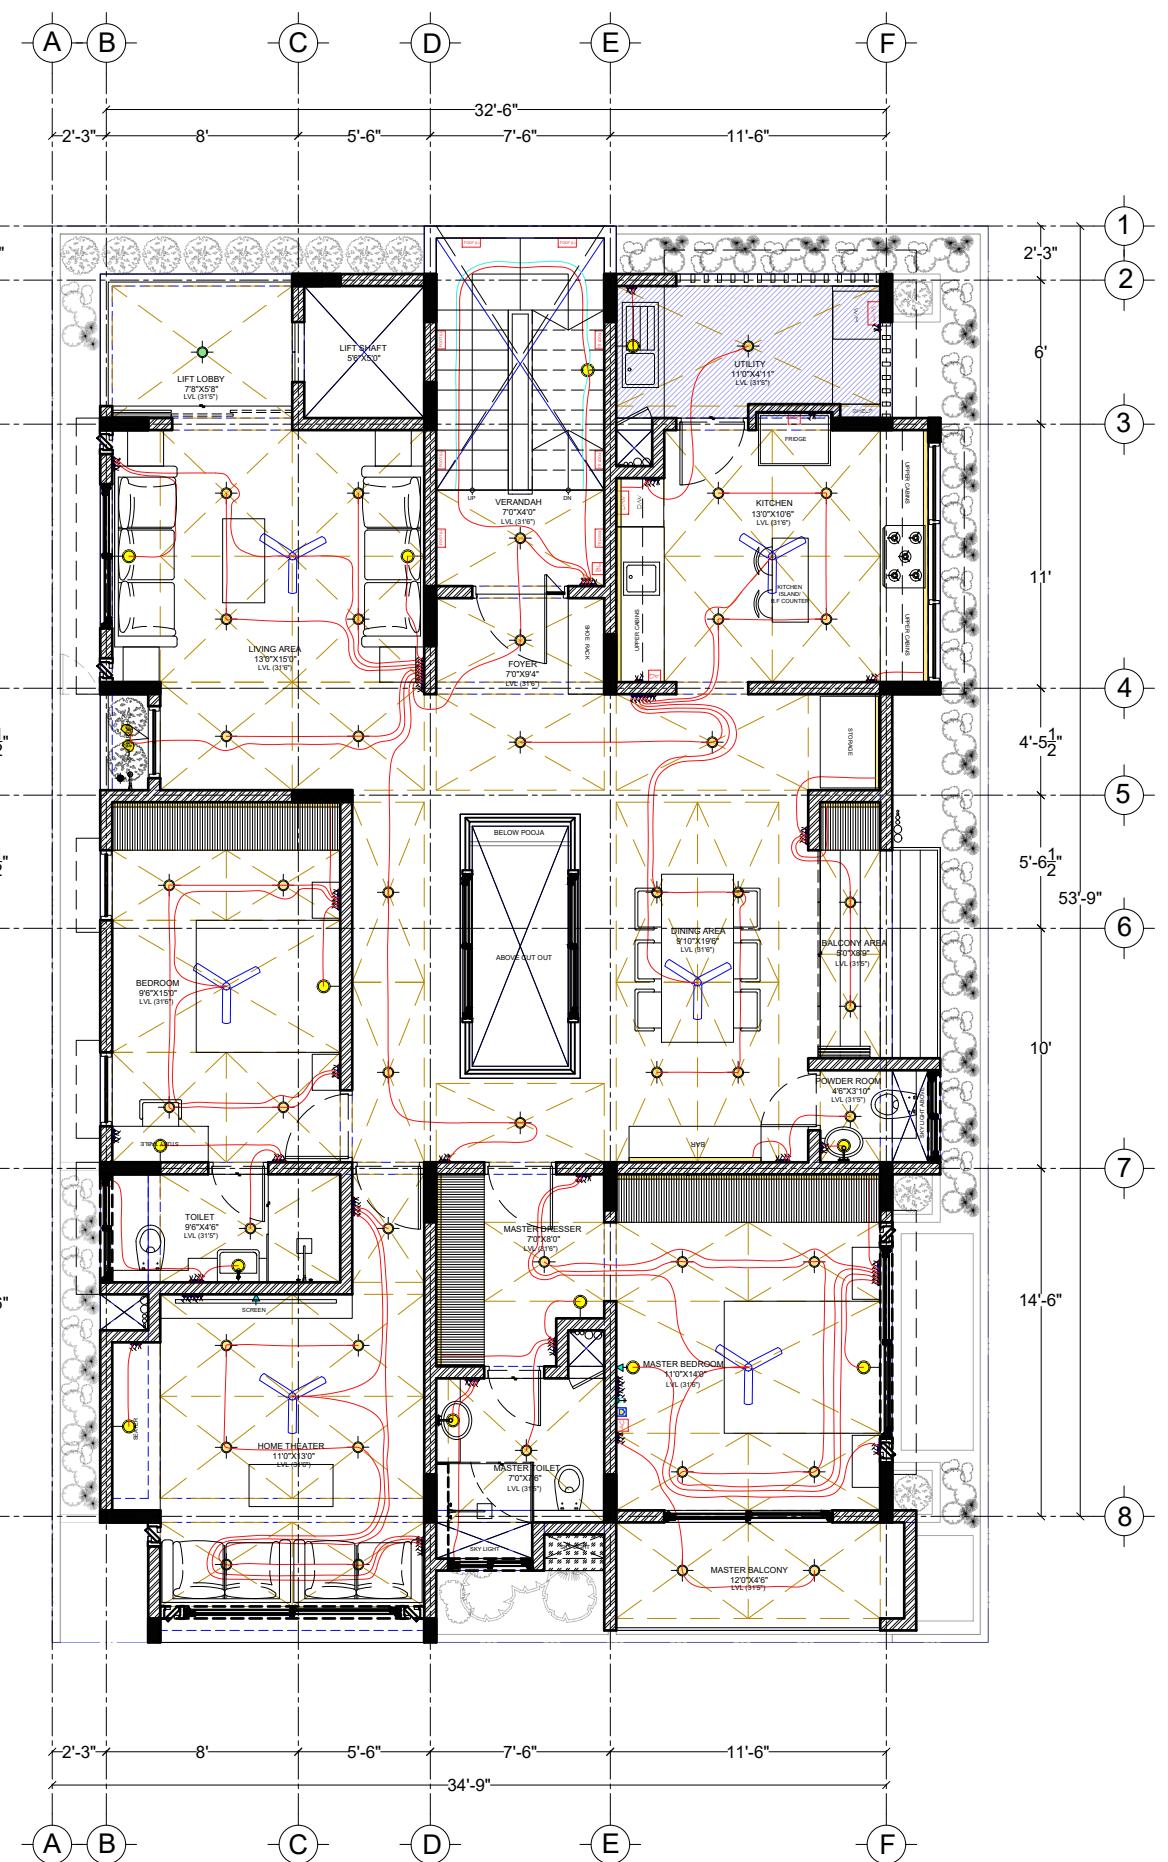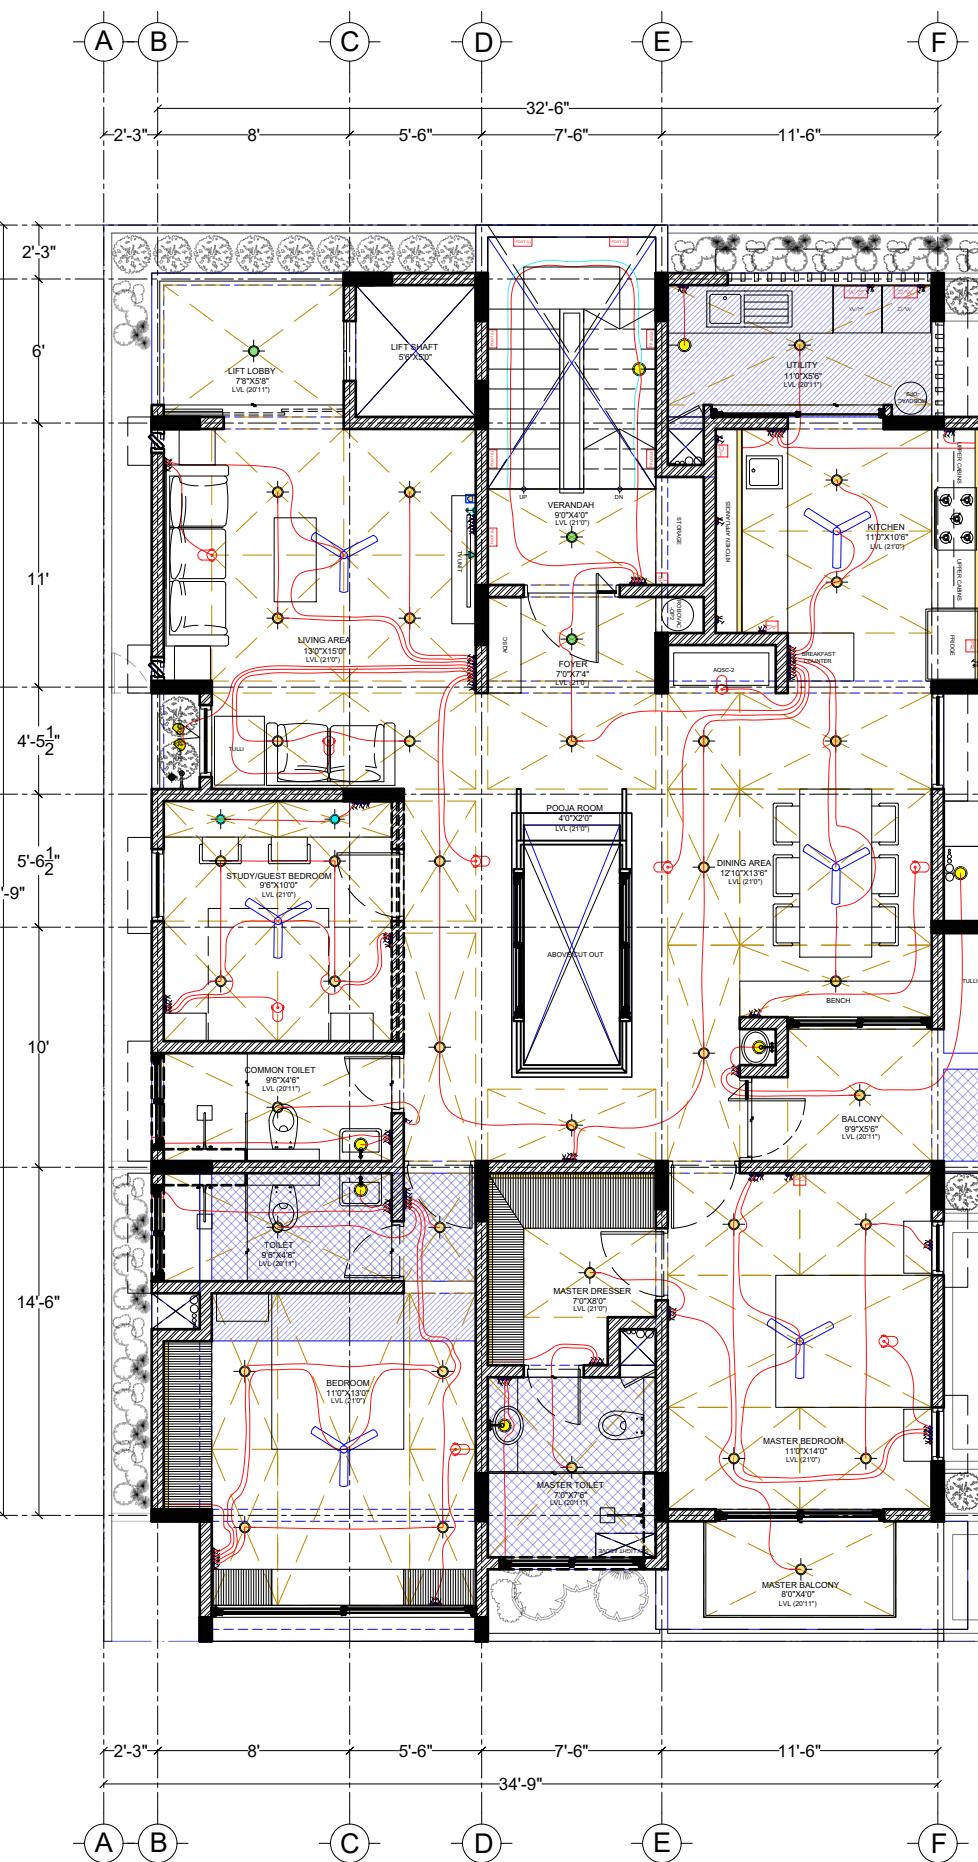

D. U. N. E

design unfiltered, a process never ending
54/2, 4th cross, Link road, Malleshwaram, Bangalore 560-003
designadune@gmail.com +91 23469351

PROJECT

PROPOSED RESIDENCE
FOR AADHYA ATG

DRAWING TITLE

WORKING DRAWING

DRAWING TITLE

TERRACE ELECTRICAL DRAWING

DATE 16 - 11 - 2022

SCALE 1" = 1'0"

PRINT ON A3

DRAWN BY JISHNU.K

CHECKED BY THEERTHAK

NOTE

TERRACE FLOOR AREA
=1783 SQFT


PROJECT CODE AATG

DRAWING NUMBER WD-001

REVISION NUMBER 0



TERRACE FLOOR PLAN

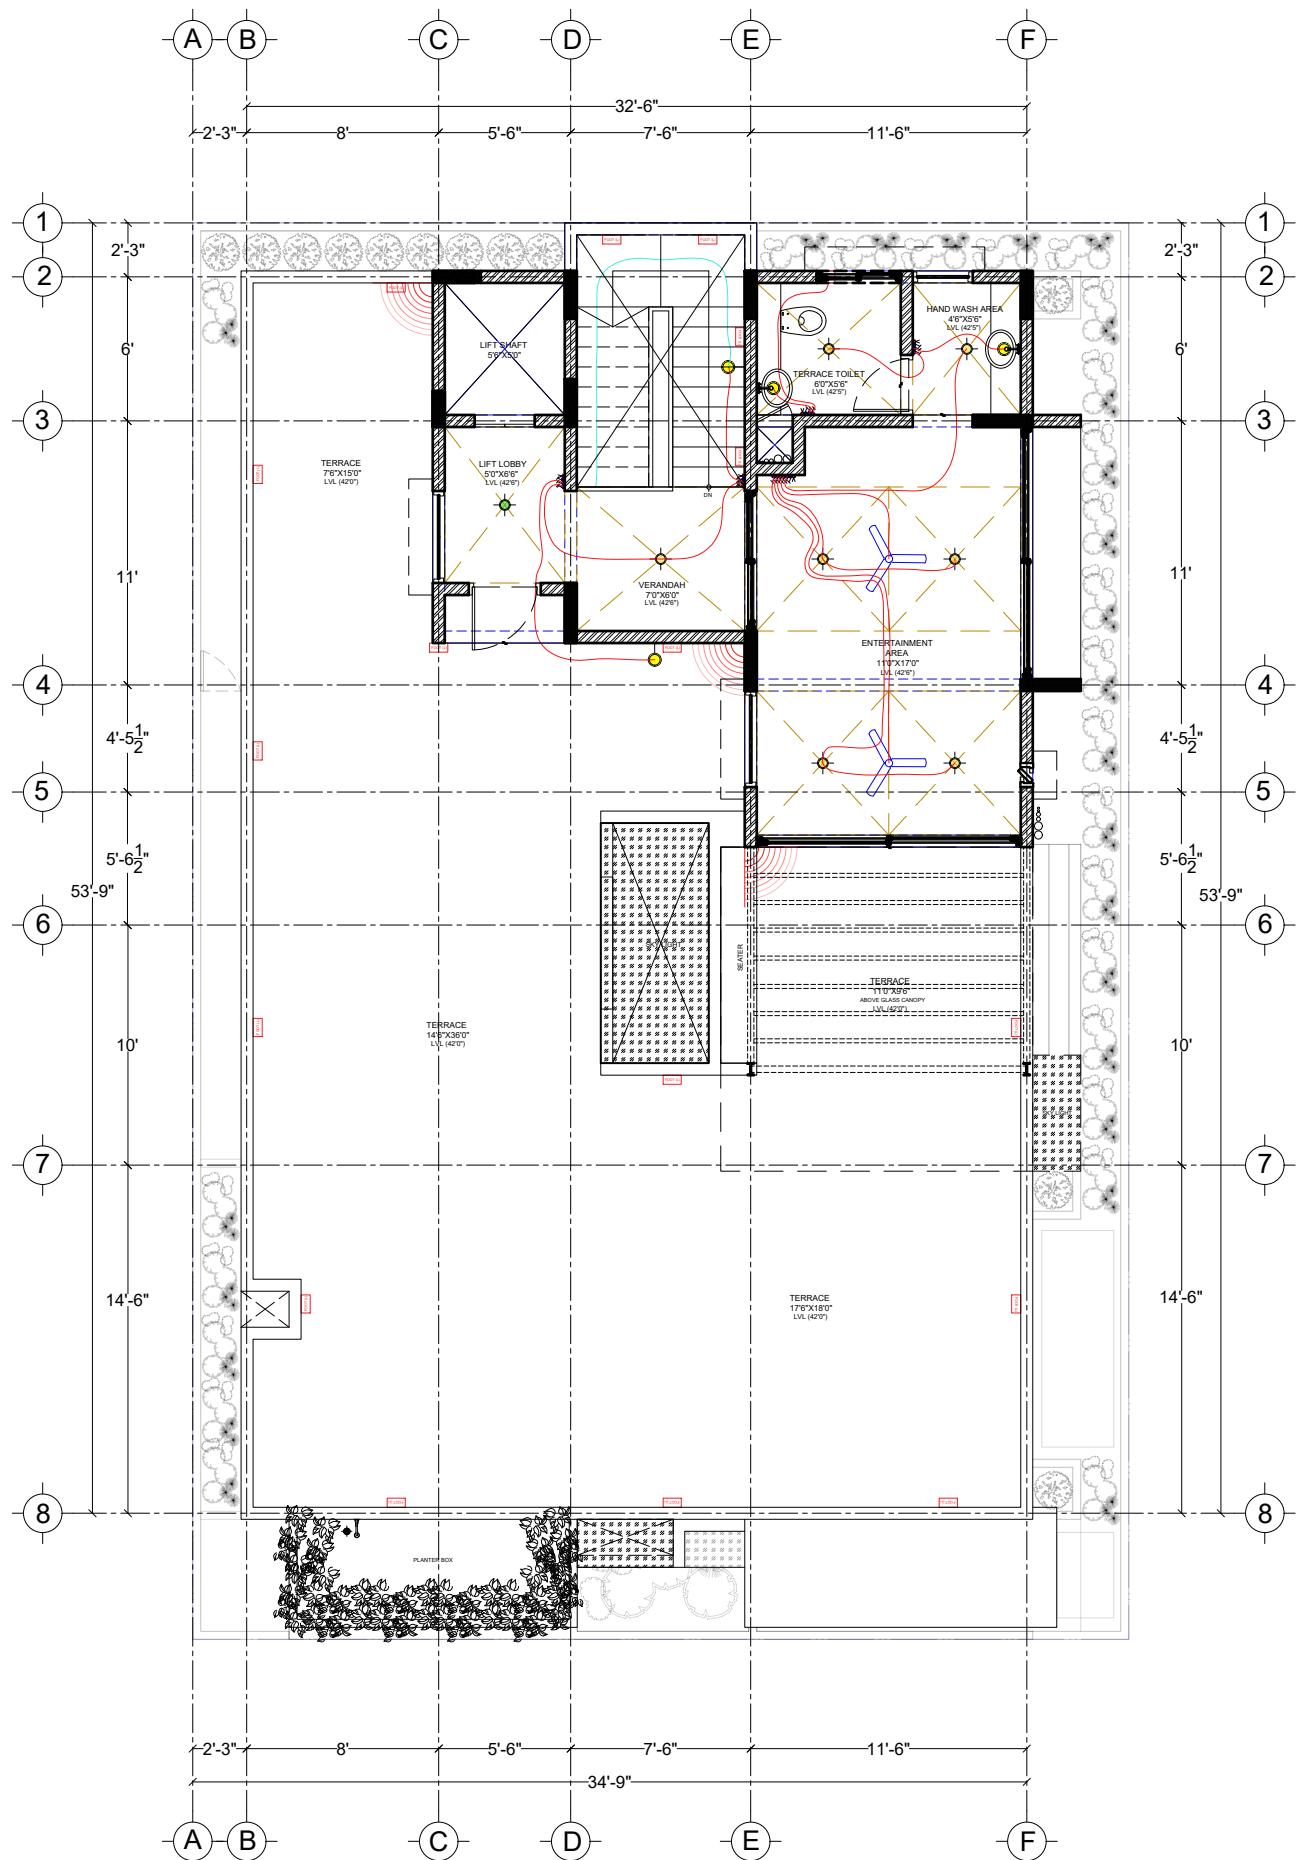

LEGEND	DESCRIPTION
	WALL POINT
	CEILING POINT
	CEILING FAN POINT
	NIGHT LIGHT
	GARDEN LIGHT
	WARDROBE LIGHT
	SPOT LIGHT
	CEILING SENSOR LIGHT
	DROP LIGHT
	16A CHARGING PORT
	5A SOCKET WITH SWITCH
	32A SOCKET WITH SWITCH
	ONE WAY SWITCH
	TWO WAY SWITCH
	TELEPHONE POINT
	T.V POINT
	DATA POINT
	SENSOR LIGHT
	AIR CONDITIONER
	DISTRIBUTION BOARD
	GEYSER
	EXHAUST FAN
	FRIDGE
	WATER PURIFIER
	METER BOARD
	WASHING MACHINE
	DISH WASHER
	CALLING BELL
	MICROWAVE OVEN
	FOOT LAMP
	CCTV

D. U. N. E

design unfiltered; a process never ending
54/2, 4th cross, Link road, Malleshwaram, Bangalore 560-003
designadune@gmail.com +91 23469351

PROJECT

NEW OFFICE
AUTUMN WOOD

DRAWING TITLE

WORKING DRAWING

DRAWING TITLE

ELECTRICAL
DRAWING

DATE 03 - 06 - 2024

SCALE NOT IN SCALE

PRINT ON A3

DRAWN BY JISHNU.K

CHECKED BY THEERTHAK



NOTE

PROJECT CODE AUT

DRAWING NUMBER WD-004

REVISION NUMBER 0

LEGEND	DESCRIPTION
	RECTANGLE DROP LIGHT
	WALL POINT
	CEILING POINT
	CEILING FAN POINT
	SENSOR LIGHT
	TABLE MOUNT SWITCH BOX
	5A SOCKET WITH SWITCH
	32A SOCKET WITH SWITCH
	ONE WAY SWITCH
	TWO WAY SWITCH
	TELEPHONE POINT
	CCTV MONITOR
	WHITE SCREEN
	T.V POINT
	DATA POINT
	AIR CONDITIONER
	DISTRIBUTION BOARD
	EXHAUST FAN
	WATER PURIFIER
	PROJECTOR
	PRINTER
	CENTRAL AC
	CCTV

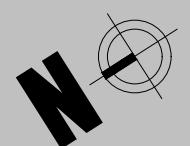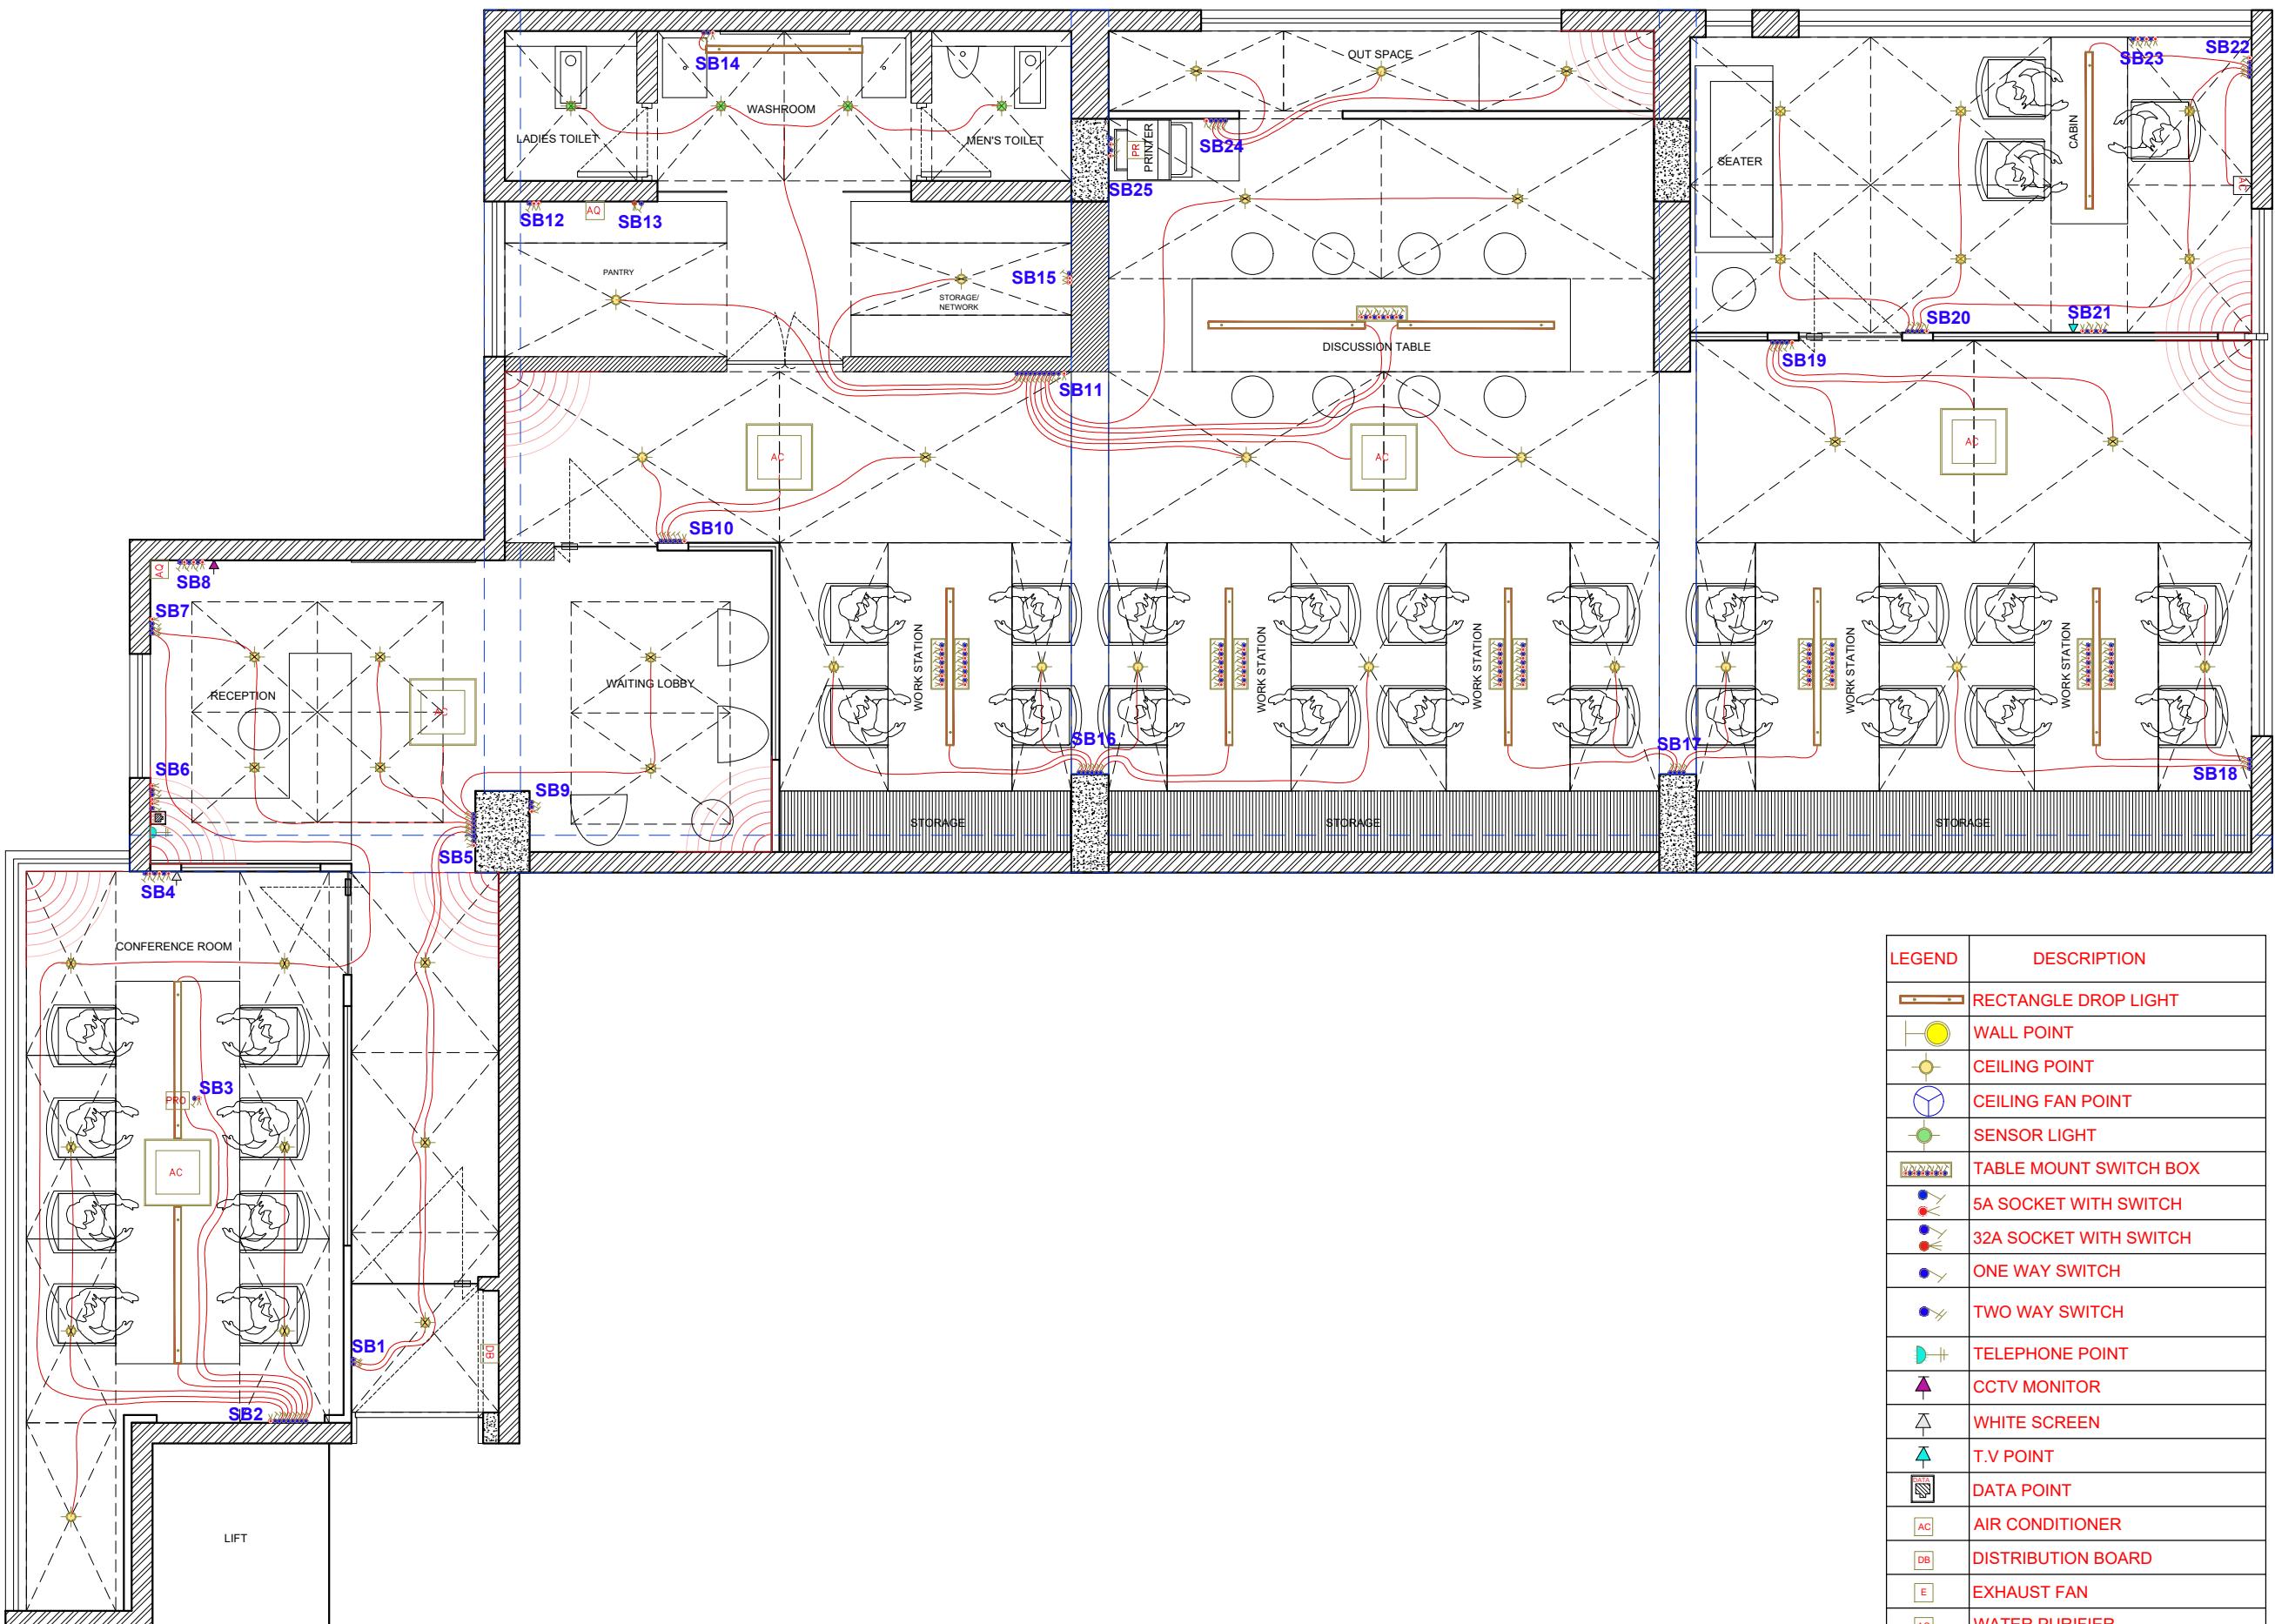

DOOR AND WINDOW DETAILS

D. U. N. E

design unfiltered; a process never ending
54/2, 4th cross, Link road, Malleshwaram, Bangalore 560-003
designadune@gmail.com +91 23469351

PROJECT

RENOVATION OF SKYGARDEN

DRAWING TITLE

WORKING DRAWING

DRAWING TITLE

DOOR & WINDOW 16A FLOOR PLAN

DATE 17 - 05 - 2025
SCALE $\frac{1}{8}$ " = 1'0"
PRINT ON A3
DRAWN BY JISHNU.K
CHECKED BY THEERTHAK



NOTE

PROJECT CODE

SKY

DRAWING NUMBER WD-002

REVISION NUMBER 0

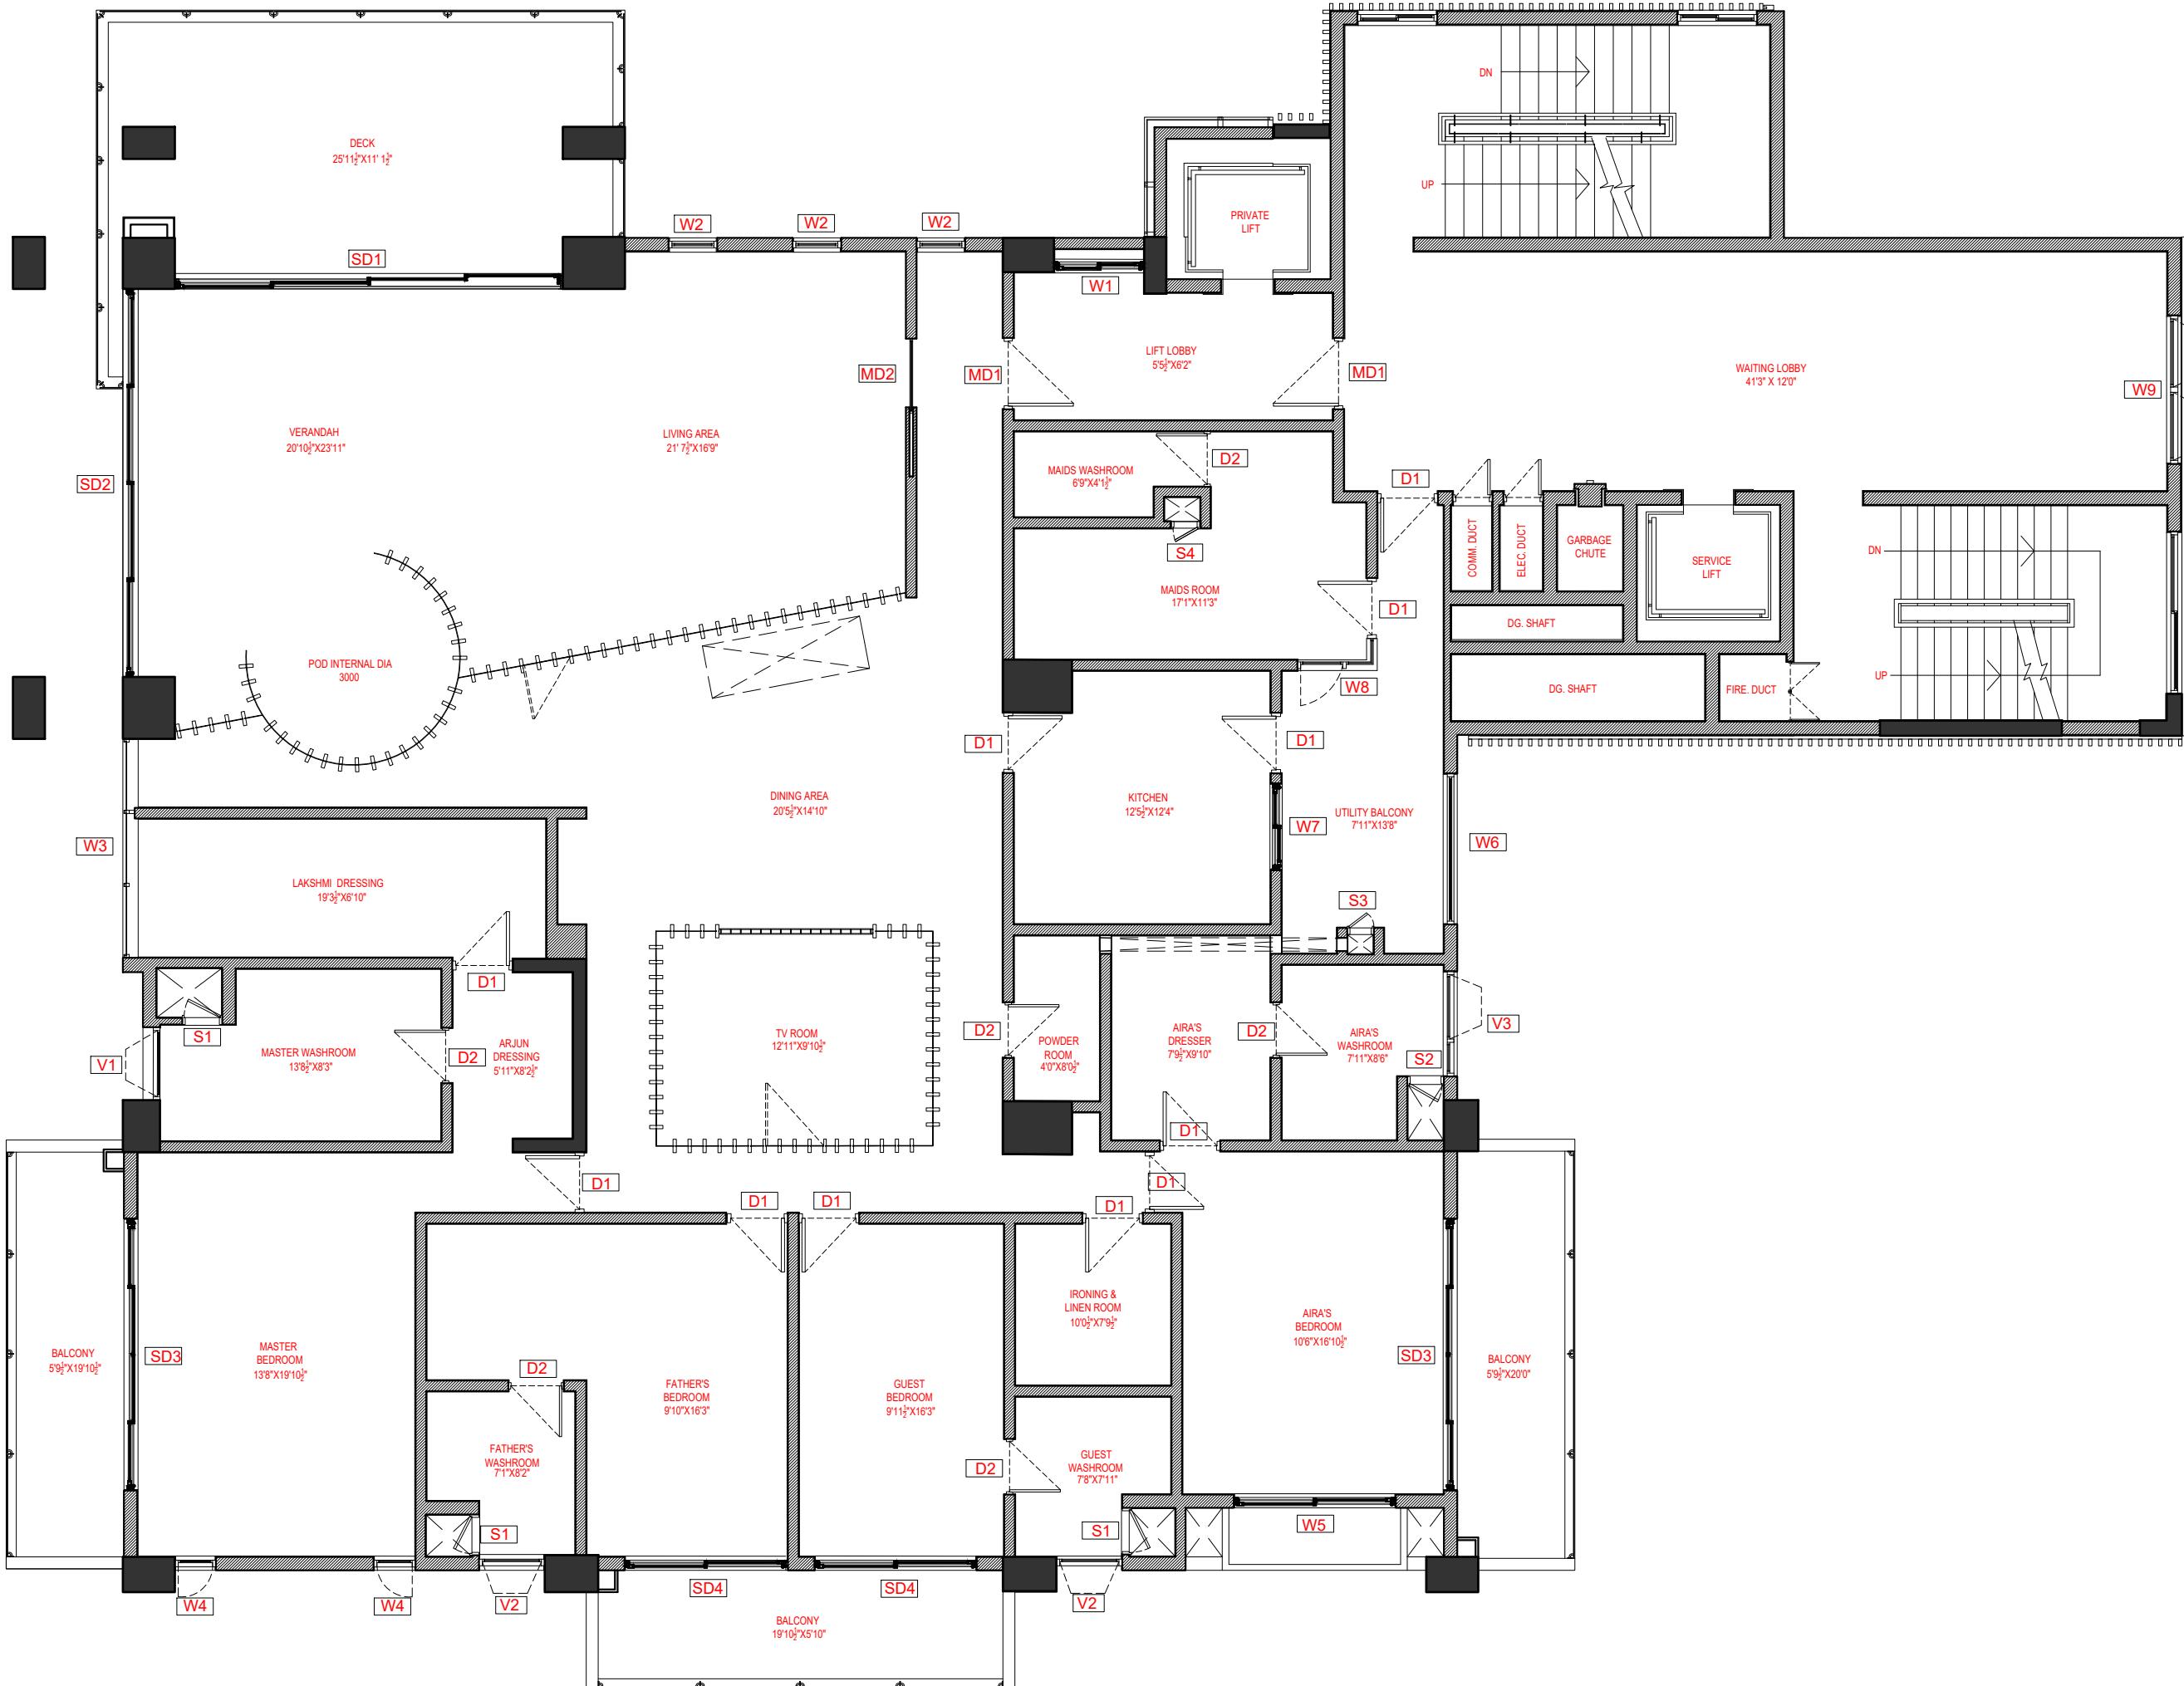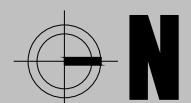

D. U. N. E

design unfiltered; a process never ending
54/2, 4th cross, Link road, Malleshwaram, Bangalore 560-003
designadune@gmail.com +91 23469351

PROJECT

RENOVATION OF SKYGARDEN

DRAWING TITLE

WORKING DRAWING

DRAWING TITLE

DOOR & WINDOW OPENING SCHEDULE

DATE 17 - 05 - 2025

SCALE NOT IN SCALE

PRINT ON A3

DRAWN BY JISHNU.K

CHECKED BY THEERTHAK


NOTE

PROJECT CODE SKY


DRAWING NUMBER WD-002

REVISION NUMBER 0


N

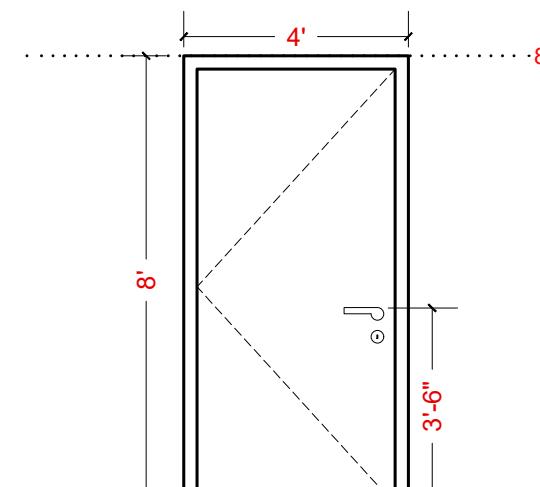


ELEVATION

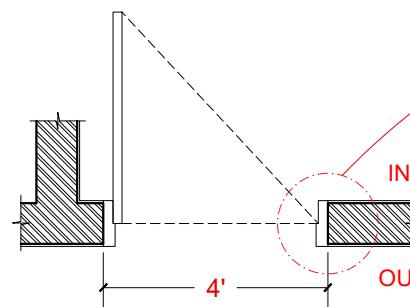


PLAN

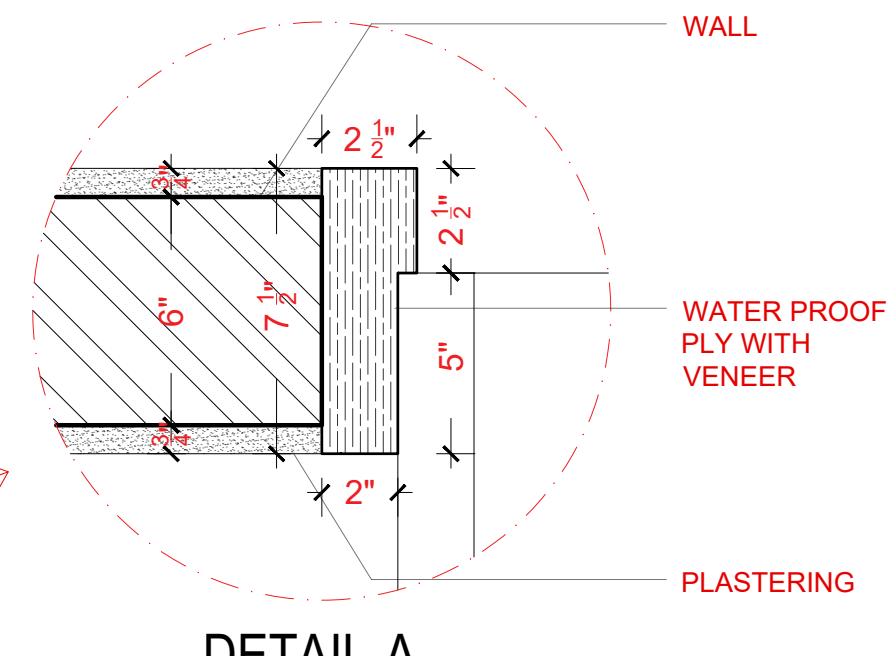

DETAIL-A

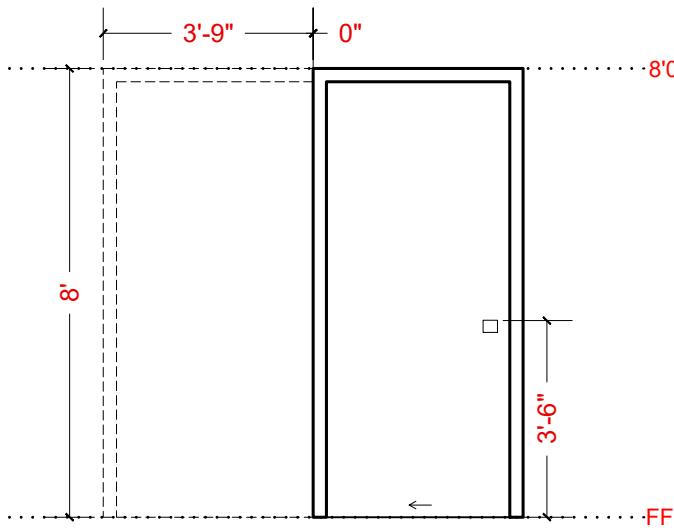

ELEVATION

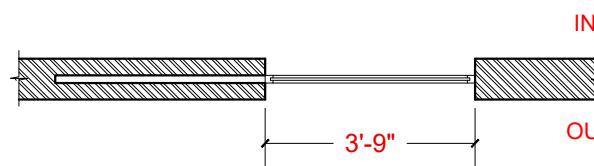

PLAN

MD1		2
LOCATION	16A-2 LIFT LOBBY	
FRAME	TIMBER	
SASH	FLUSH WITH VENEER	
HARDWARE	DIGITAL DOOR LOCK	

MD2		1
LOCATION	16A-1 LIVING	
FRAME	FLUSH + VENEER	
SASH		
HARDWARE		

D. U. N. E

design unfiltered; a process never ending
54/2, 4th cross, Link road, Malleshwaram, Bangalore 560-003
designadune@gmail.com +91 23469351

PROJECT

RENOVATION OF
SKYGARDEN

DRAWING TITLE

WORKING DRAWING

DRAWING TITLE

DOOR & WINDOW
OPENING SCHEDULE

DATE 17 - 05 - 2025

SCALE NOT IN SCALE

PRINT ON A3

DRAWN BY JISHNU.K

CHECKED BY THEERTHAK


NOTE

PROJECT CODE SKY


DRAWING NUMBER WD-002

REVISION NUMBER


0

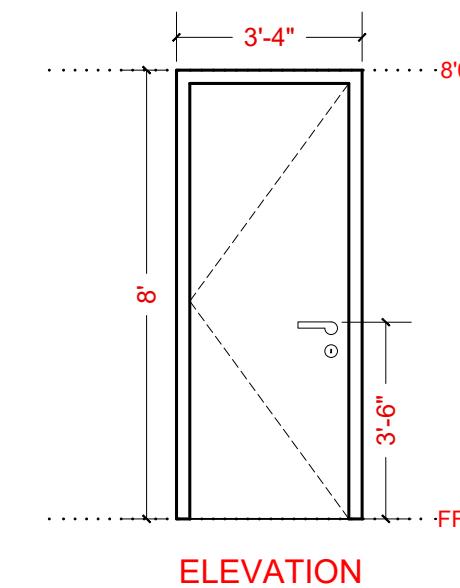


ELEVATION

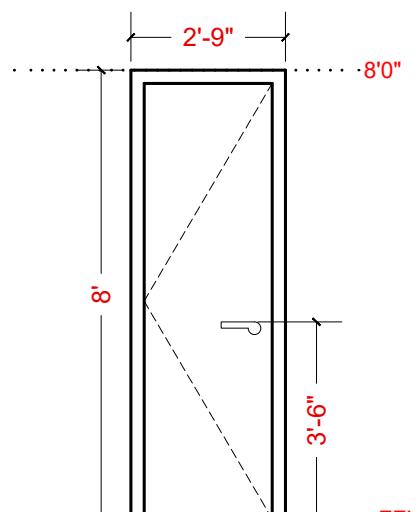

ELEVATION

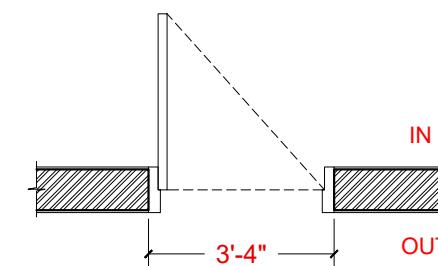

PLAN

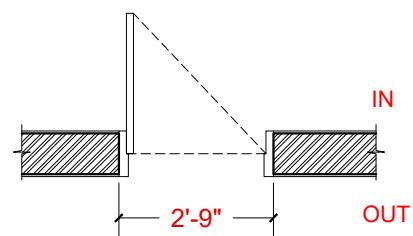

PLAN

D1		11
16A-11 MAID's ROOM, KITCHEN, AIRA's DRESSER, AIRA's BEDROOM, AIRA's DRESSER IRONING AND LINEN ROOM, GUEST BEDROOM, FATHER'S BEDROOM, MASTER BEDROOM, LAKSHMI DRESSER		
FRAME	TIMBER	
SASH	FLUSH WITH VENEER	

D2		6
16A-6 MASTER WASHROOM, FATHER's WASHROOM, GUEST WASHROOM, POWDER ROOM, AIRA's WASHROOM, MAID'S WASHROOM		
FRAME	TIMBER	
SASH	FLUSH WITH VENEER	



D. U. N. E

design unfiltered; a process never ending
54/2, 4th cross, Link road, Malleshwaram, Bangalore 560-003
designadune@gmail.com +91 23469351

PROJECT

RENOVATION OF
SKYGARDEN

DRAWING TITLE

WORKING DRAWING

DRAWING TITLE

DOOR & WINDOW
OPENING SCHEDULE

DATE 17 - 05 - 2025

SCALE NOT IN SCALE

PRINT ON A3

DRAWN BY JISHNU.K


CHECKED BY THEERTHAK

NOTE


PROJECT CODE SKY

DRAWING NUMBER WD-002


REVISION NUMBER 0

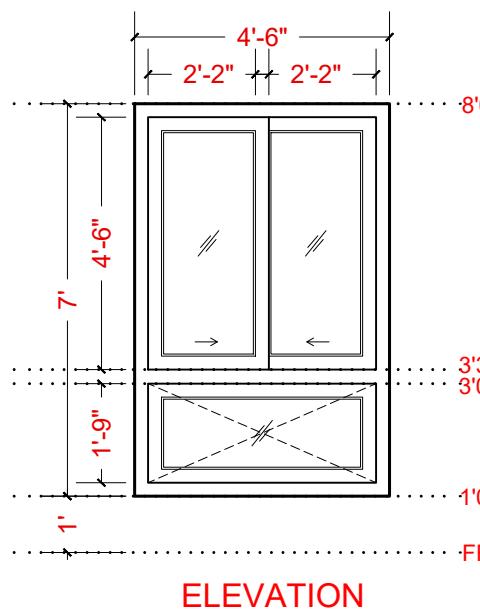


ELEVATION

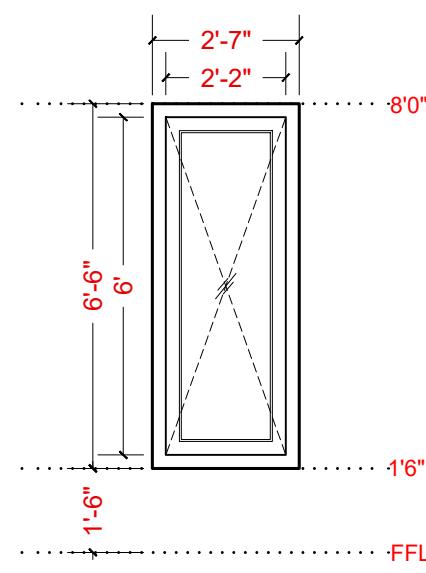


ELEVATION

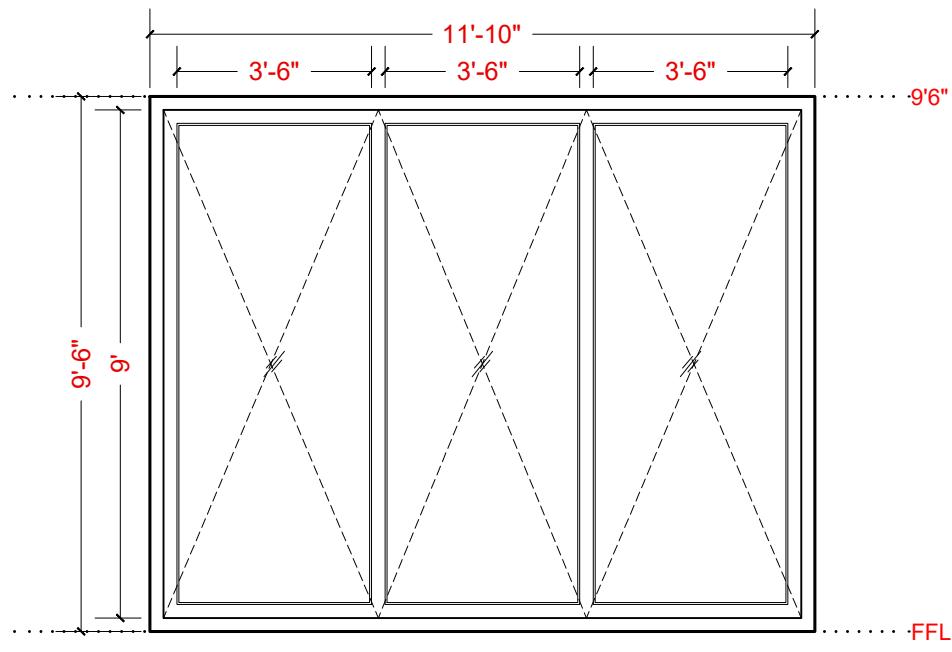


ELEVATION

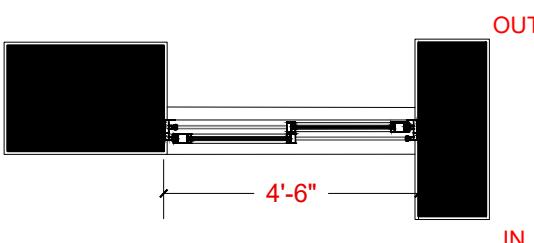

PLAN

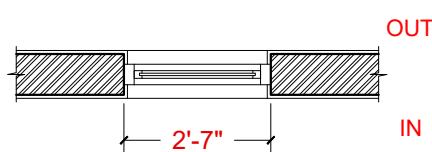

PLAN

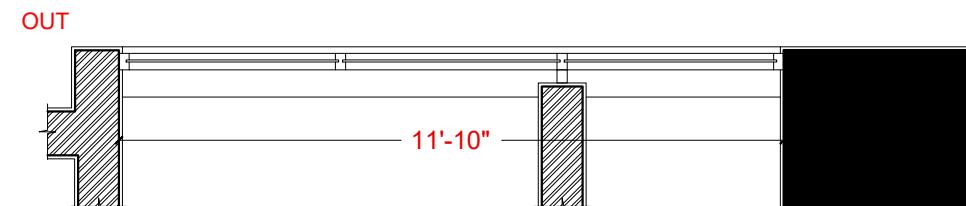

PLAN

W1		1
LOCATION	16A-1 AT LIFT LOBBY	
MATERIAL	ALUMINUM	
OPERATION	CASEMENT WINDOW, FIXED WINDOW	
NOTE	LINTEL DIMENSIONS MAY VARY BY UP TO +/- 30mm	

W2		3
LOCATION	16A-3 LIVING AREA	
MATERIAL	ALUMINUM	
OPERATION	FIXED WINDOW	
NOTE	LINTEL DIMENSIONS MAY VARY BY UP TO +/- 30mm	

W3		1
LOCATION	16A-1 LAKSHMI DRESSING,	
MATERIAL	ALUMINUM	
OPERATION	FIXED WINDOW	
NOTE	NEEDS EXTRA VERTICAL MEMBER AS INDICATED IN RED LINTEL DIMENSIONS MAY VARY BY UP TO +/- 30mm	



D. U. N. E

design unfiltered; a process never ending
54/2, 4th cross, Link road, Malleshwaram, Bangalore 560-003
designadune@gmail.com +91 23469351

PROJECT

RENOVATION OF
SKYGARDEN

DRAWING TITLE

WORKING DRAWING

DRAWING TITLE

DOOR & WINDOW
OPENING SCHEDULE

DATE 17 - 05 - 2025

SCALE NOT IN SCALE

PRINT ON A3

DRAWN BY JISHNU.K


CHECKED BY THEERTHAK

NOTE


PROJECT CODE SKY

DRAWING NUMBER WD-002


REVISION NUMBER 0

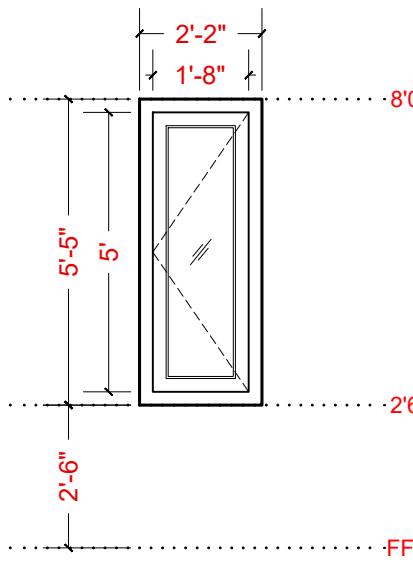


ELEVATION

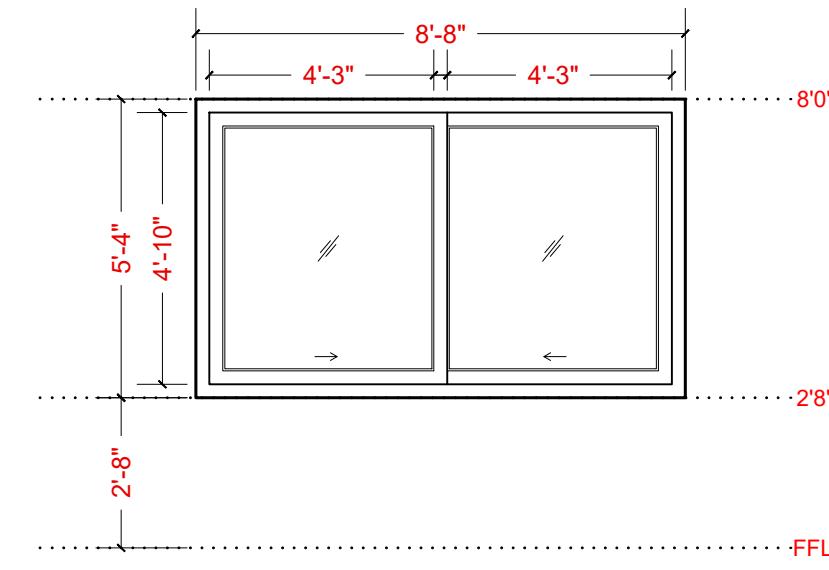


ELEVATION

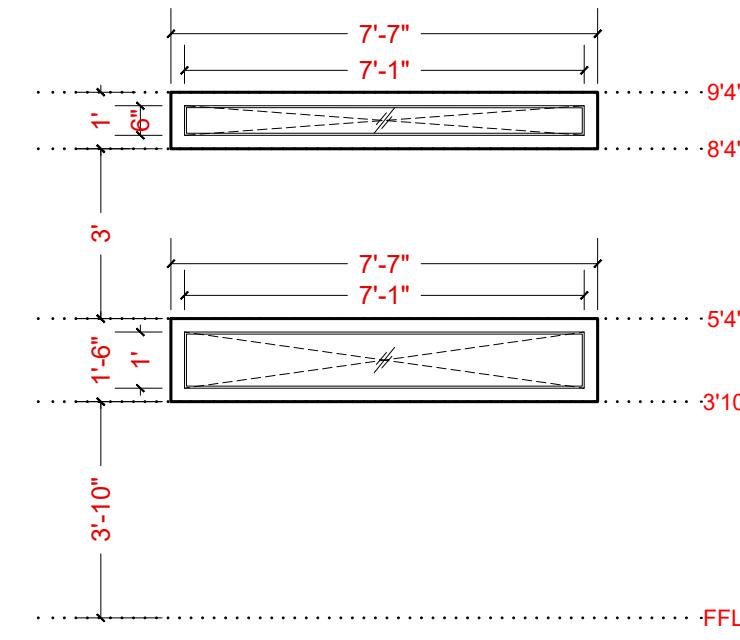


ELEVATION

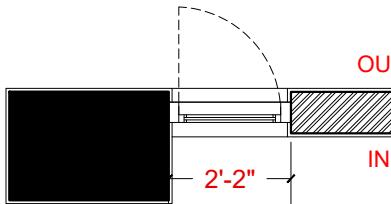

PLAN

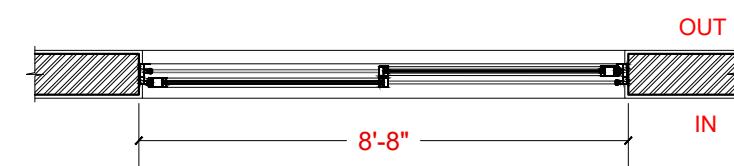

PLAN

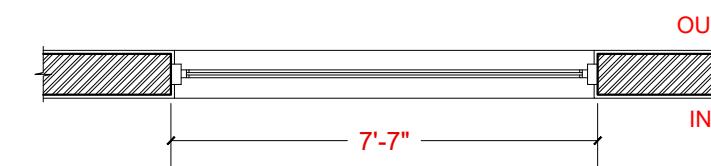

PLAN

W4		2
LOCATION	16A-2 MASTER BEDROOM,	
MATERIAL		
OPERATION	CASEMENT WINDOW	
NOTE	LINTEL DIMENSIONS MAY VARY BY UP TO +/- 30mm	

W5		1
LOCATION	16A-1 AIRA's BED ROOM	
MATERIAL		
OPERATION	SLIDING WINDOW + SLIDING MESH	
NOTE	LINTEL DIMENSIONS MAY VARY BY UP TO +/- 30mm	

W6		1
LOCATION	16A-1 UTILITY BALCONY	
MATERIAL		
OPERATION	FIXED WINDOW	
NOTE	LINTEL DIMENSIONS MAY VARY BY UP TO +/- 30mm	

D. U. N. E

design unfiltered; a process never ending
54/2, 4th cross, Link road, Malleshwaram, Bangalore 560-003
designadune@gmail.com +91 23469351

PROJECT

RENOVATION OF
SKYGARDEN

DRAWING TITLE

WORKING DRAWING

DRAWING TITLE

DOOR & WINDOW
OPENING SCHEDULE

DATE 17 - 05 - 2025

SCALE NOT IN SCALE

PRINT ON A3

DRAWN BY JISHNU.K







CHECKED BY THEERTHAK

NOTE

PROJECT CODE SKY

DRAWING NUMBER WD-002

REVISION NUMBER 0

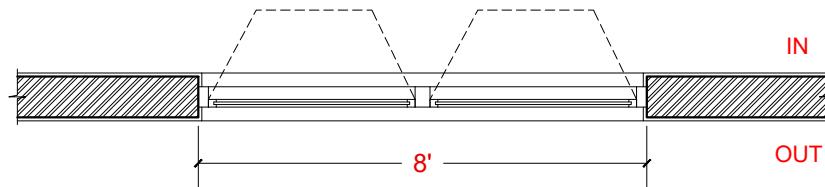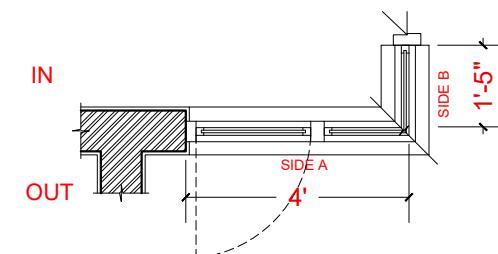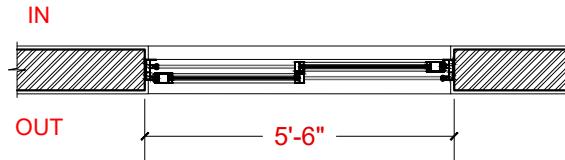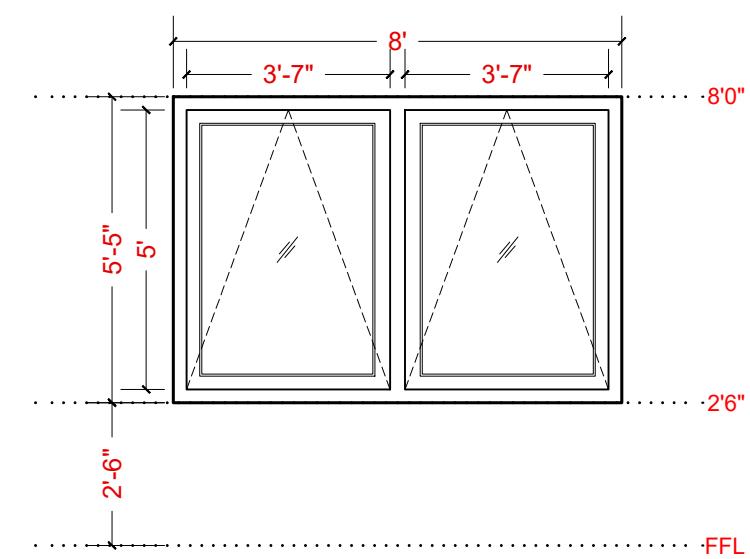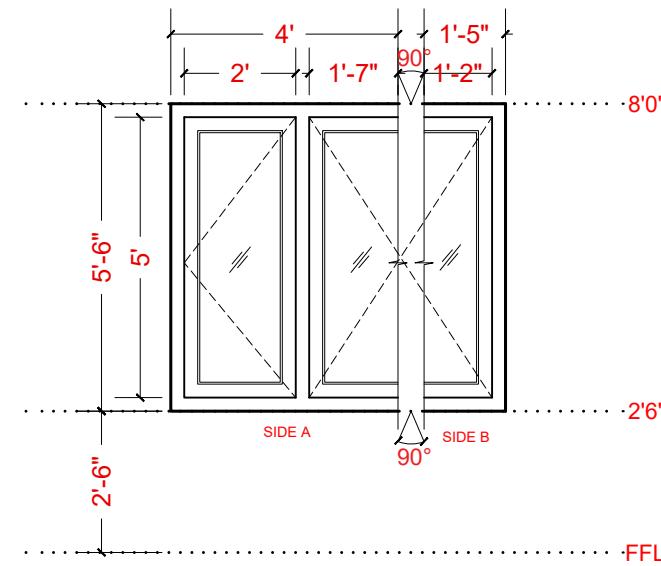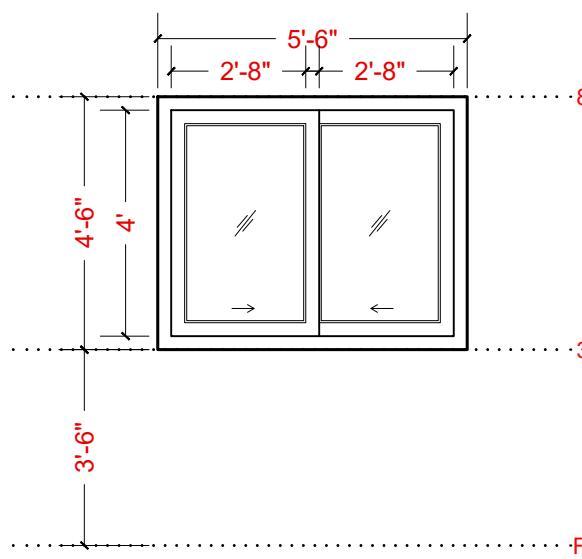

W7		1
LOCATION	16A-1 KITCHEN	
MATERIAL		
OPERATION	SLIDING WINDOW	
NOTE	LINTEL DIMENSIONS MAY VARY BY UP TO +/- 30mm	

W8		1
LOCATION	16A-1 MAID's ROOM	
MATERIAL		
OPERATION	CASEMENT + FIXED WINDOW	
NOTE	LINTEL DIMENSIONS MAY VARY BY UP TO +/- 30mm	

W9		1
LOCATION	16AB-1 WAITING LOBBY	
MATERIAL		
OPERATION	2 PANEL TOP HUNG	
NOTE	LINTEL DIMENSIONS MAY VARY BY UP TO +/- 30mm	

D. U. N. E

design unfiltered; a process never ending
54/2, 4th cross, Link road, Malleshwaram, Bangalore 560-003
designadune@gmail.com +91 23469351

PROJECT

RENOVATION OF
SKYGARDEN

DRAWING TITLE

WORKING DRAWING

DRAWING TITLE

DOOR & WINDOW
OPENING SCHEDULE



DATE 17 - 05 - 2025
SCALE NOT IN SCALE
PRINT ON A3
DRAWN BY JISHNU.K
CHECKED BY THEERTHAK

NOTE

PROJECT CODE SKY

DRAWING NUMBER WD-002

REVISION NUMBER 0

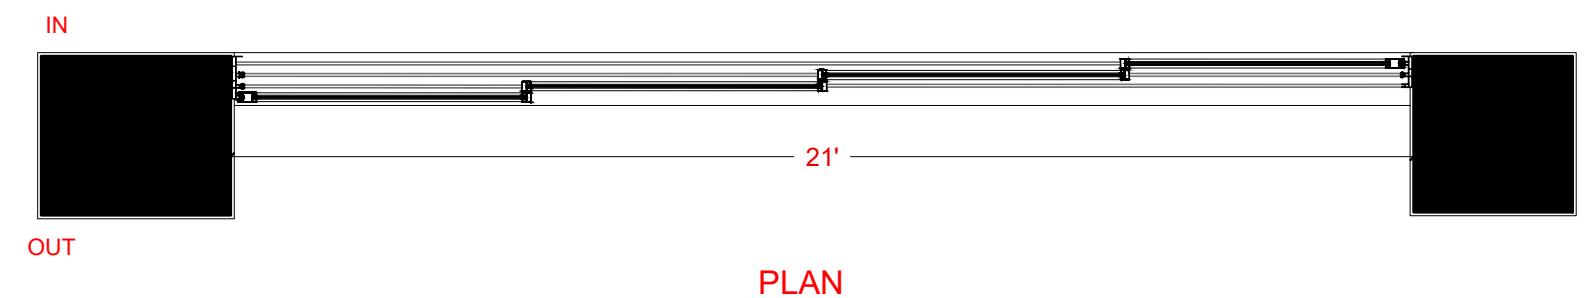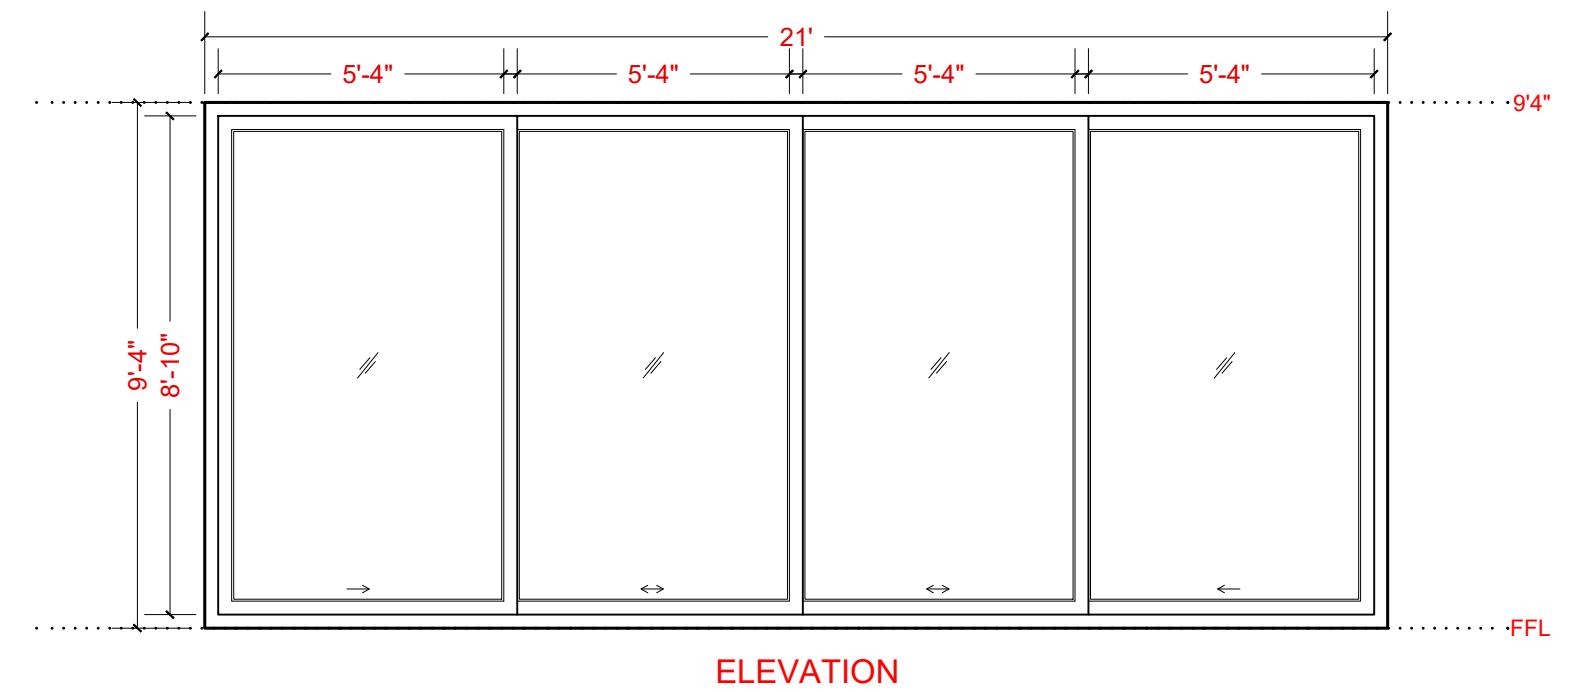

SD1		1
LOCATION	16A-1 VERANDHA	
MATERIAL		
OPERATION	4 PANELS OF SLIDING WINDOW + (SLIM AND SEMI HIDDEN) + NO GUTTER	
NOTE	LINTEL DIMENSIONS MAY VARY BY UP TO +/- 30mm	

D. U. N. E

design unfiltered; a process never ending
54/2, 4th cross, Link road, Malleshwaram, Bangalore 560-003
designadune@gmail.com +91 23469351

PROJECT

RENOVATION OF
SKYGARDEN

DRAWING TITLE

WORKING DRAWING

DRAWING TITLE

DOOR & WINDOW
OPENING SCHEDULE


DATE 17 - 05 - 2025
SCALE NOT IN SCALE
PRINT ON A3
DRAWN BY JISHNU.K
CHECKED BY THEERTHAK

NOTE


PROJECT CODE SKY

DRAWING NUMBER WD-002


REVISION NUMBER 0

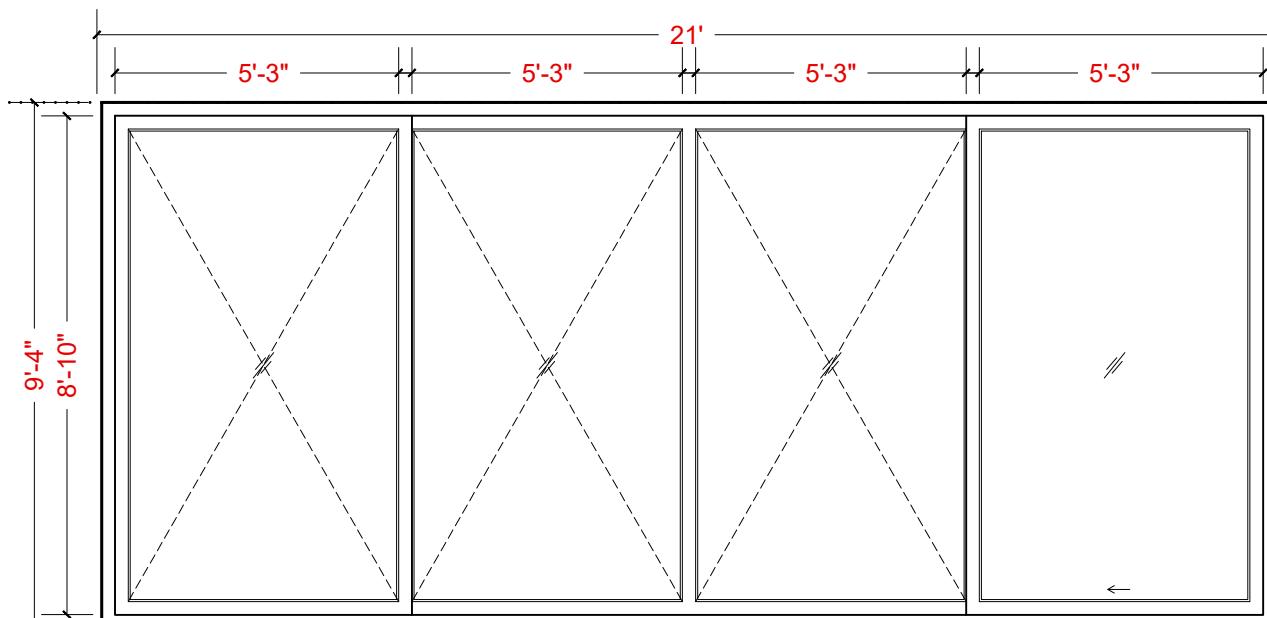


ELEVATION

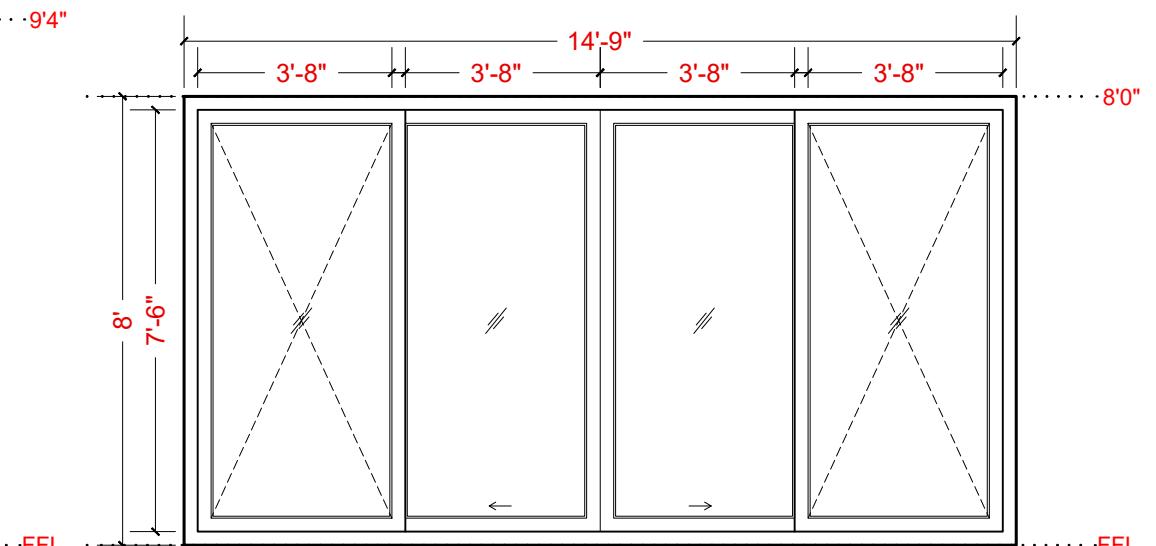

ELEVATION

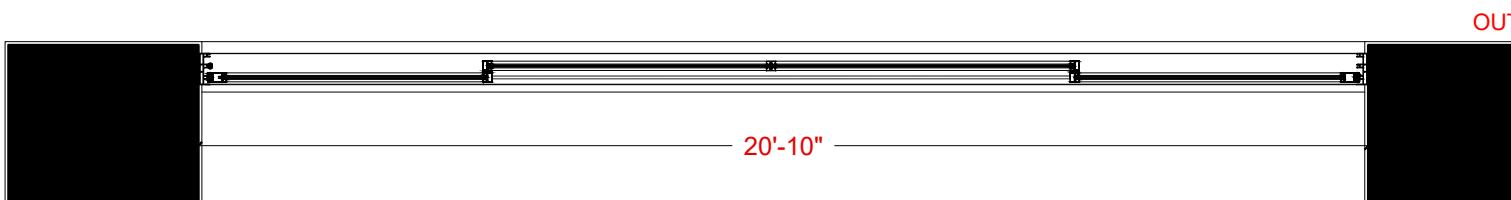

PLAN

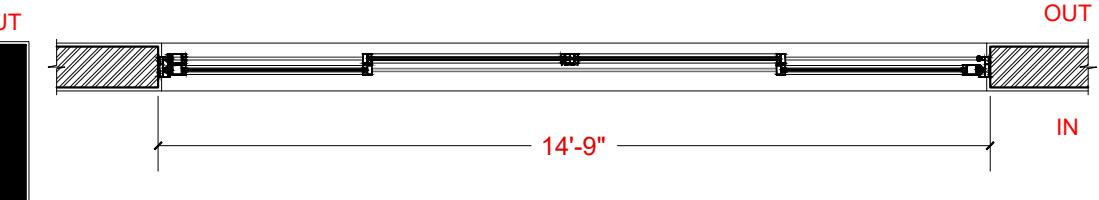

PLAN

SD2		1
LOCATION	16A-1 VERANDHA	
MATERIAL		
OPERATION	3 PANELS OF FIXED 1 PANELS OF SLIDING	
NOTE	LINTEL DIMENSIONS MAY VARY BY UP TO +/- 30mm	

SD3		2
LOCATION	16A-2 MASTER BEDROOM, AIRA's BEDROOM	
MATERIAL		
OPERATION	2 PANELS OF FIXED 2 PANELS OF SLIDING	
NOTE	LINTEL DIMENSIONS MAY VARY BY UP TO +/- 30mm	

D. U. N. E

design unfiltered; a process never ending
54/2, 4th cross, Link road, Malleshwaram, Bangalore 560-003
designadune@gmail.com +91 23469351

PROJECT

RENOVATION OF
SKYGARDEN

DRAWING TITLE

WORKING DRAWING

DRAWING TITLE

DOOR & WINDOW
OPENING SCHEDULE

DATE 17 - 05 - 2025

SCALE NOT IN SCALE

PRINT ON A3

DRAWN BY JISHNU.K


CHECKED BY THEERTHAK

NOTE


PROJECT CODE SKY

DRAWING NUMBER WD-002

REVISION NUMBER 0

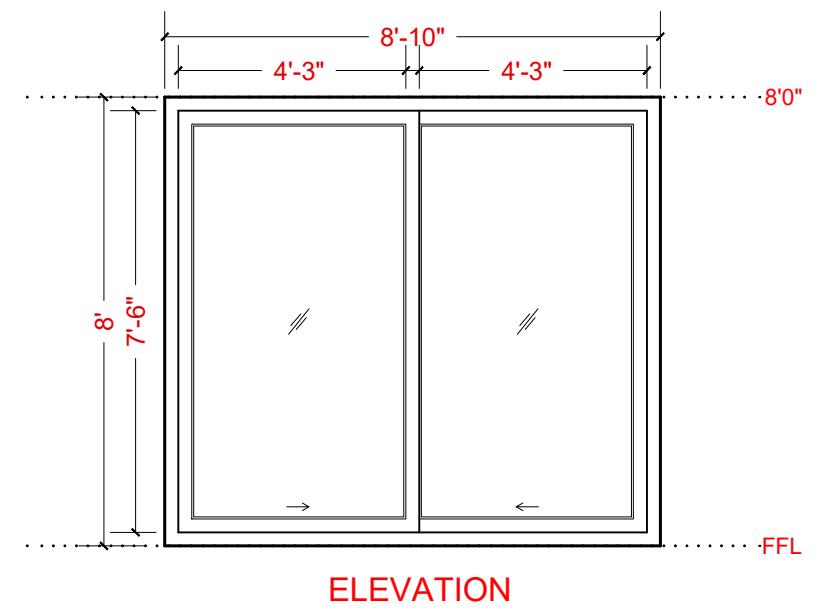

ELEVATION

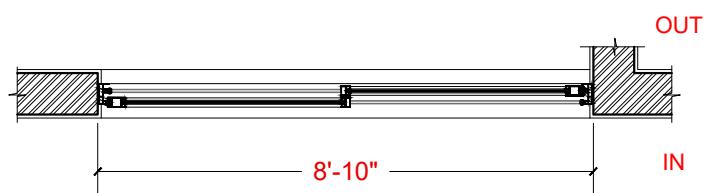

PLAN

SD4		2
LOCATION		
MATERIAL		
OPERATION	SLIDING DOOR	
NOTE	LINTEL DIMENSIONS MAY VARY BY UP TO +/- 30mm	



D. U. N. E

design unfiltered; a process never ending
54/2, 4th cross, Link road, Malleshwaram, Bangalore 560-003
designadune@gmail.com +91 23469351

PROJECT

RENOVATION OF
SKYGARDEN

DRAWING TITLE

WORKING DRAWING

DRAWING TITLE

DOOR & WINDOW
OPENING SCHEDULE

DATE 17 - 05 - 2025

SCALE NOT IN SCALE

PRINT ON A3

DRAWN BY JISHNU.K







CHECKED BY THEERTHAK

NOTE

PROJECT CODE SKY

DRAWING NUMBER WD-002

REVISION NUMBER 0

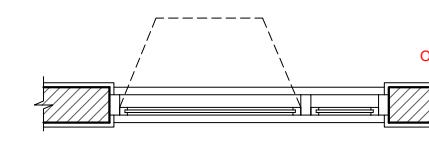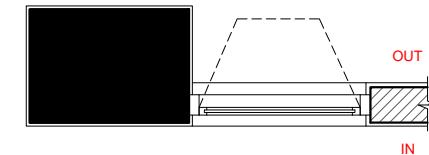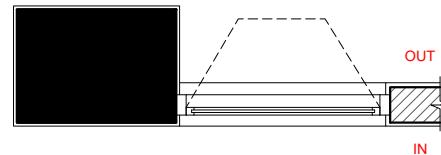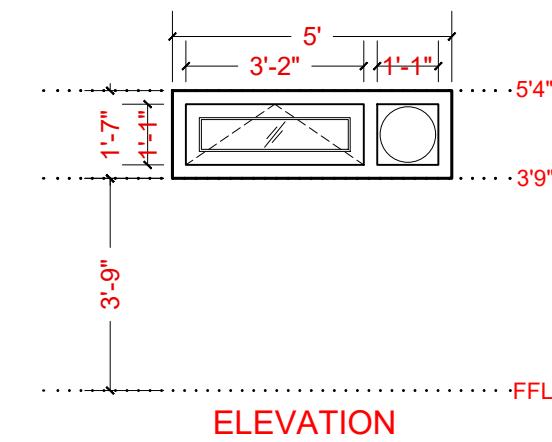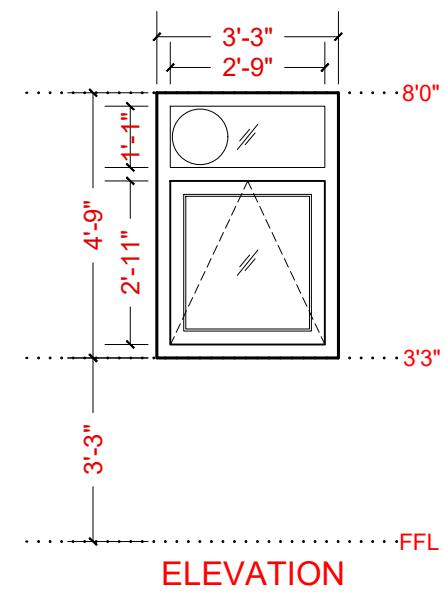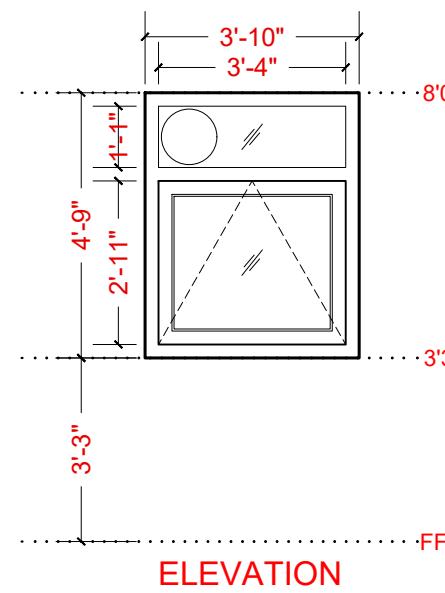

V1		1	V2		2	V3		1
LOCATION	16A-1 MASTER WASHROOM		LOCATION	16A-2 FATHER's WASHROOM, GUEST WASHROOM		LOCATION	16A-1 AIRS's WASHROOM	
MATERIAL	ALUMINIUM		MATERIAL	ALUMINIUM		MATERIAL	ALUMINIUM	
OPERATION	TOP HUNG WITH EXHAUST FAN		OPERATION	TOP HUNG WITH EXHAUST FAN		OPERATION	TOP HUNG WITH EXHAUST FAN	
NOTE	LINTEL DIMENSIONS MAY VARY BY UP TO +/- 30mm		NOTE	LINTEL DIMENSIONS MAY VARY BY UP TO +/- 30mm		NOTE	LINTEL DIMENSIONS MAY VARY BY UP TO +/- 30mm	

D. U. N. E

design unfiltered; a process never ending
54/2, 4th cross, Link road, Malleshwaram, Bangalore 560-003
designadune@gmail.com +91 23469351

PROJECT

RENOVATION OF
SKYGARDEN

DRAWING TITLE

WORKING DRAWING

DRAWING TITLE

DOOR & WINDOW
OPENING SCHEDULE

DATE 17 - 05 - 2025

SCALE NOT IN SCALE

PRINT ON A3

DRAWN BY JISHNU.K


CHECKED BY THEERTHAK

NOTE


PROJECT CODE SKY

DRAWING NUMBER WD-002


REVISION NUMBER 0

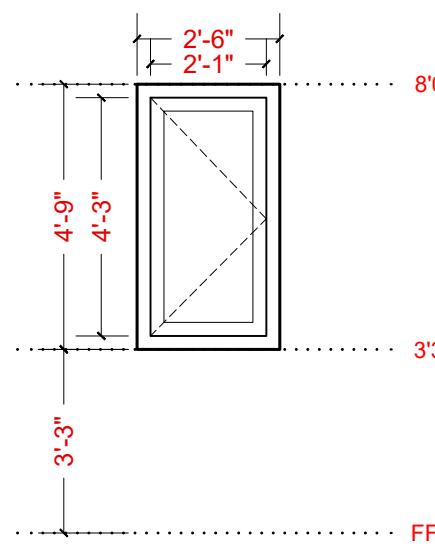


ELEVATION

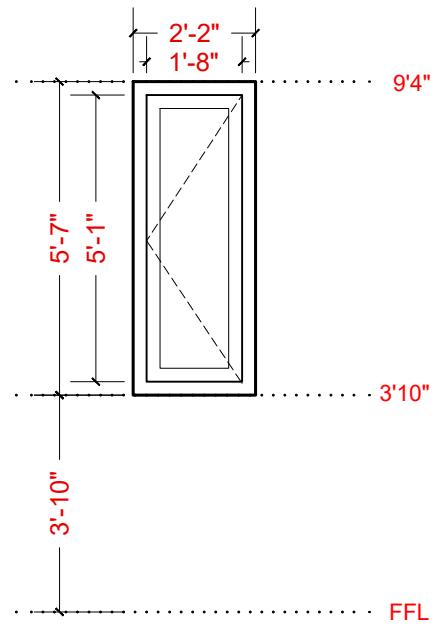


ELEVATION

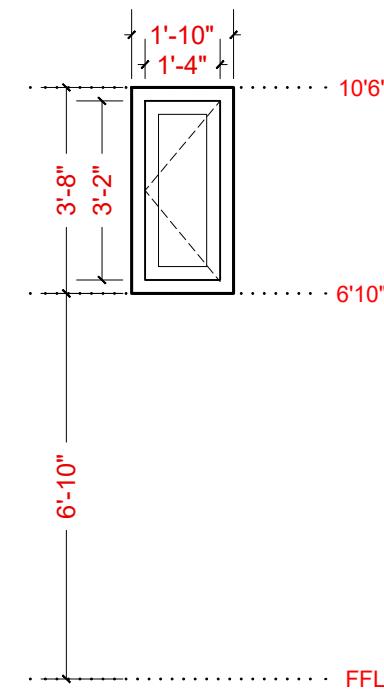


ELEVATION

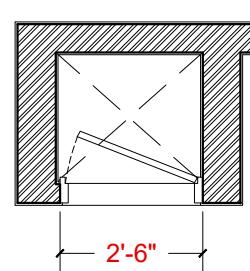

PLAN

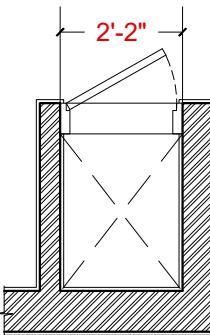

PLAN

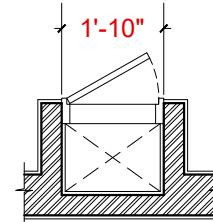

PLAN

S1		3	S2		1	S3		1
LOCATION	16A-3 MASTER WASHROOM, FATHER's WASHROOM, GUEST WASHROOM		LOCATION	16A-1 AIRA's WASHROOM,		LOCATION	16A-1 UTILITY	
MATERIAL	TRANSLUCENT GLASS/ ALUMINUM		MATERIAL	TRANSLUCENT GLASS/ ALUMINUM		MATERIAL	TRANSLUCENT GLASS/ ALUMINUM	
OPERATION	SOLID COVER, HANDLE FREE OPTION		OPERATION	SOLID COVER, HANDLE FREE OPTION		OPERATION	SOLID COVER, HANDLE FREE OPTION	

D. U. N. E

design unfiltered; a process never ending
54/2, 4th cross, Link road, Malleshwaram, Bangalore 560-003
designadune@gmail.com +91 23469351

PROJECT

RENOVATION OF
SKYGARDEN

DRAWING TITLE

WORKING DRAWING

DRAWING TITLE

DOOR & WINDOW
OPENING SCHEDULE


DATE 17 - 05 - 2025
SCALE NOT IN SCALE
PRINT ON A3
DRAWN BY JISHNU.K
CHECKED BY THEERTHAK

NOTE


PROJECT CODE SKY

DRAWING NUMBER WD-002

REVISION NUMBER 0

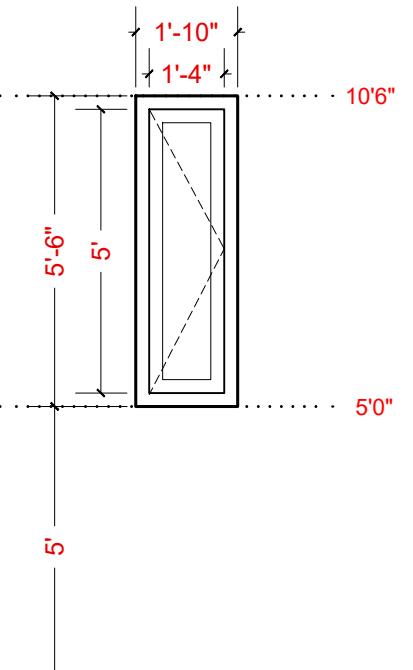


ELEVATION

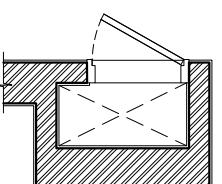

PLAN


S4		1
LOCATION	16A-1 MAID ROOM	
MATERIAL	TRANSLUCENT GLASS/ ALUMINUM	
OPERATION	SOLID COVER, HANDLE FREE OPTION	

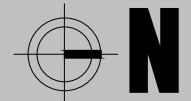


PLUMBING DRAWINGS

D. U. N. E


design unfiltered, a process never ending
54/2, 4th cross, Link road, Malleshwaram, Bangalore 560-003
designadune@gmail.com +91 23469351

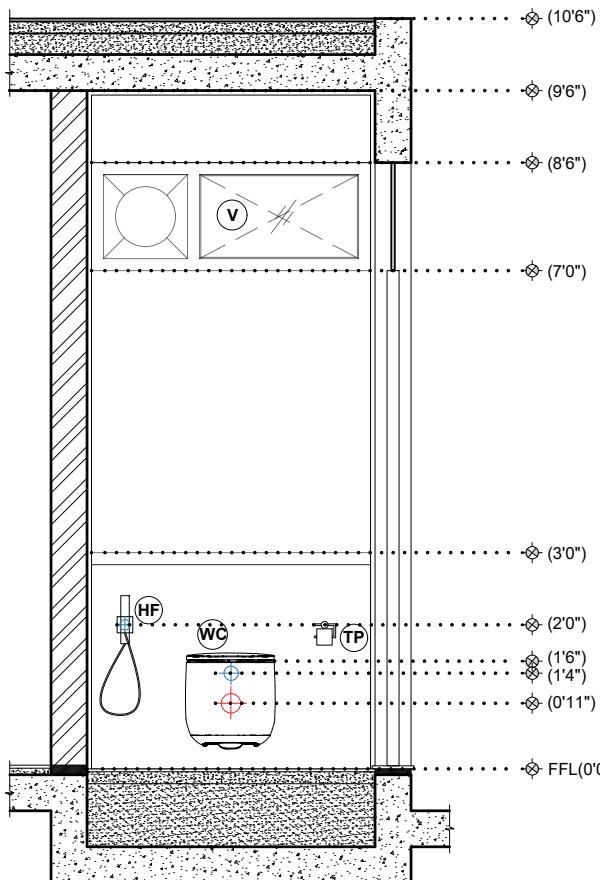


ELEVATION-AA

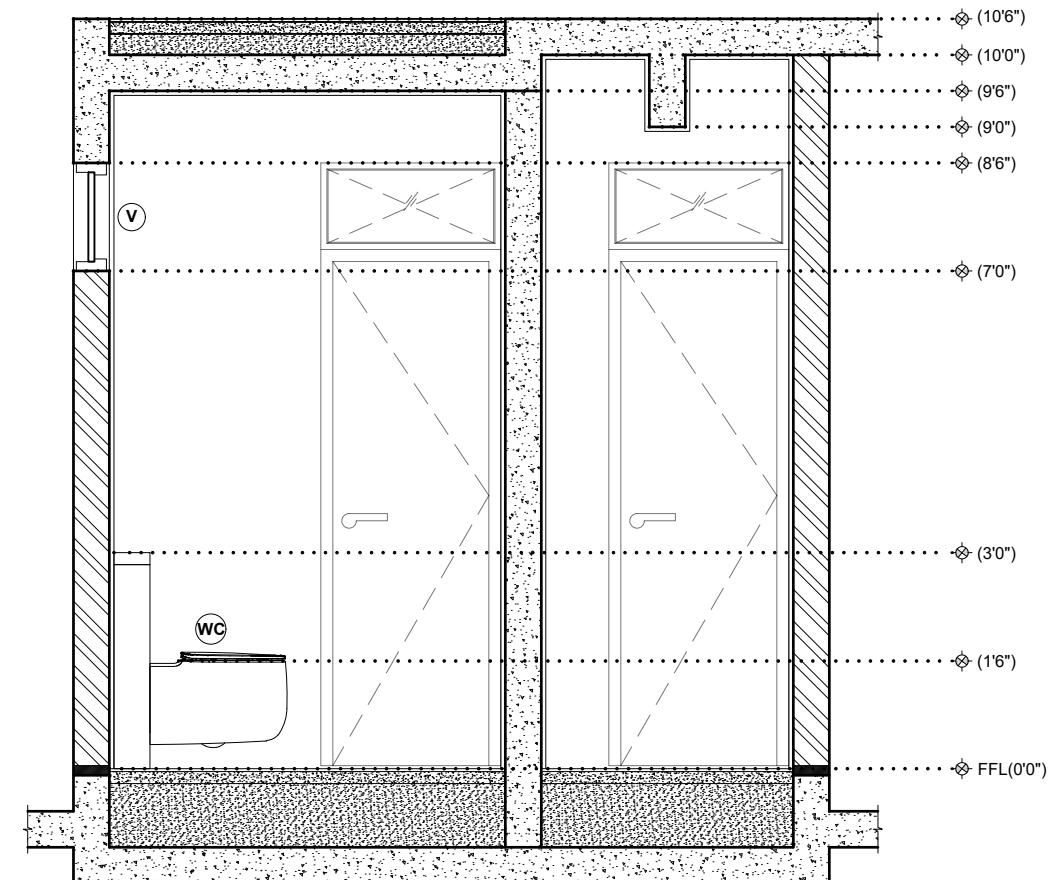

ELEVATION-BB

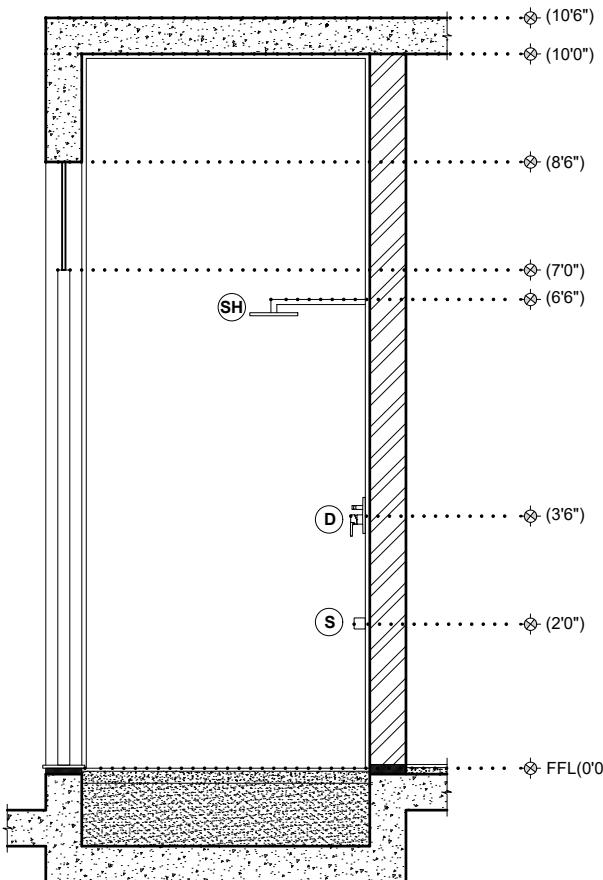

ELEVATION-CC

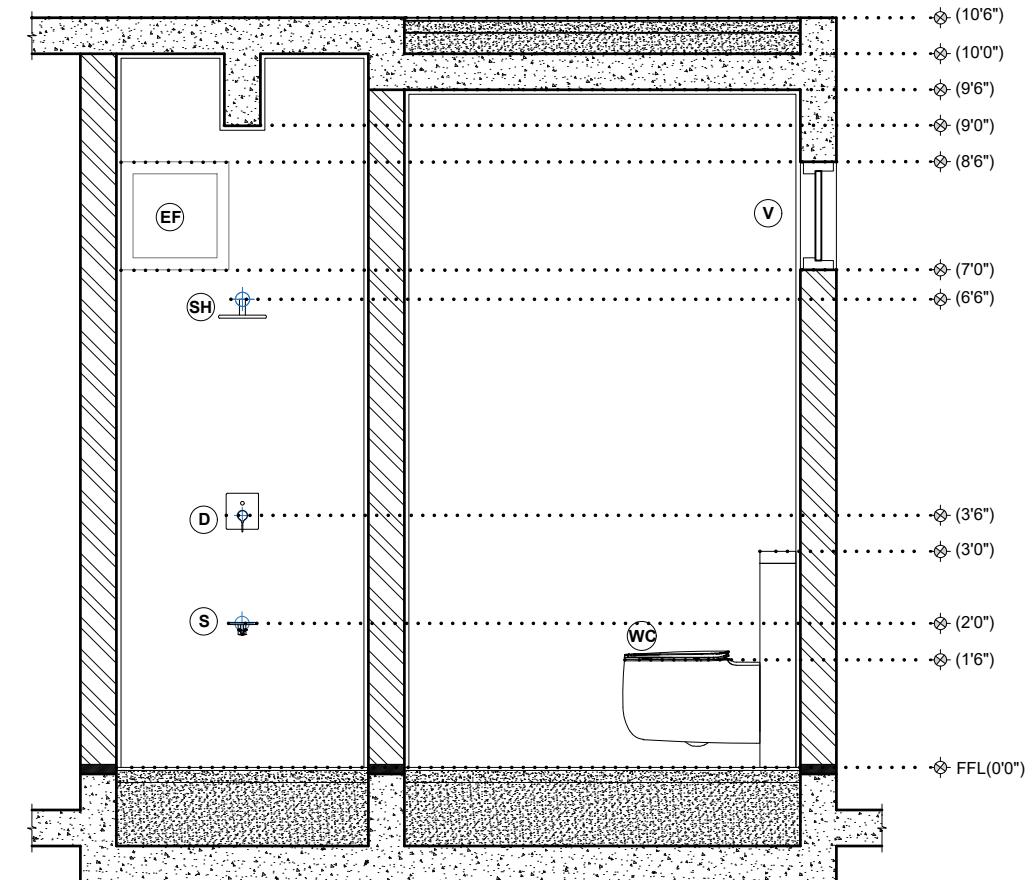

ELEVATION-DD

WC	WATER CLOSET	HF	HEALTH FAUCET
BT	BOTTLE TRAP	S	SPOUT
VT	VANITY TOP	D	DIVERTOR
V	VENTILATOR	FP	FLUSH PLATE
SH	SHOWER HEAD	FRESH WATER PIPE	FRESH WATER PIPE
TP	TISSUE PAPER HOLDER	WASTE WATER PIPE	WASTE WATER PIPE

AREA

1. WALL AREA = 252 SQFT

2. FLOOR AREA = 39 SQFT

FIXTURES

1. WC -WALL HUNG

2. SHOWER-SINGLE LIVER DIVERTER WITH 3 WAY OUT

PROJECT

PROPOSED RESIDENCE
FOR AADHYA ATG

DRAWING TITLE

WORKING DRAWING

DRAWING TITLE

PLUMBING DRAWINGS

DATE 16 - 11 - 2022

SCALE $\frac{3}{8}'' = 1'0''$

PRINT ON A3

DRAWN BY JISHNU.K

CHECKED BY THEERTHAK


NOTE

"FOR ESTIMATION PURPOSE ONLY"
"PLUMBING DRAWING MAY CHANGE
BASED ON FIXTURE SELECTIONS"

PROJECT CODE AATG

DRAWING NUMBER WD-004

REVISION NUMBER 0

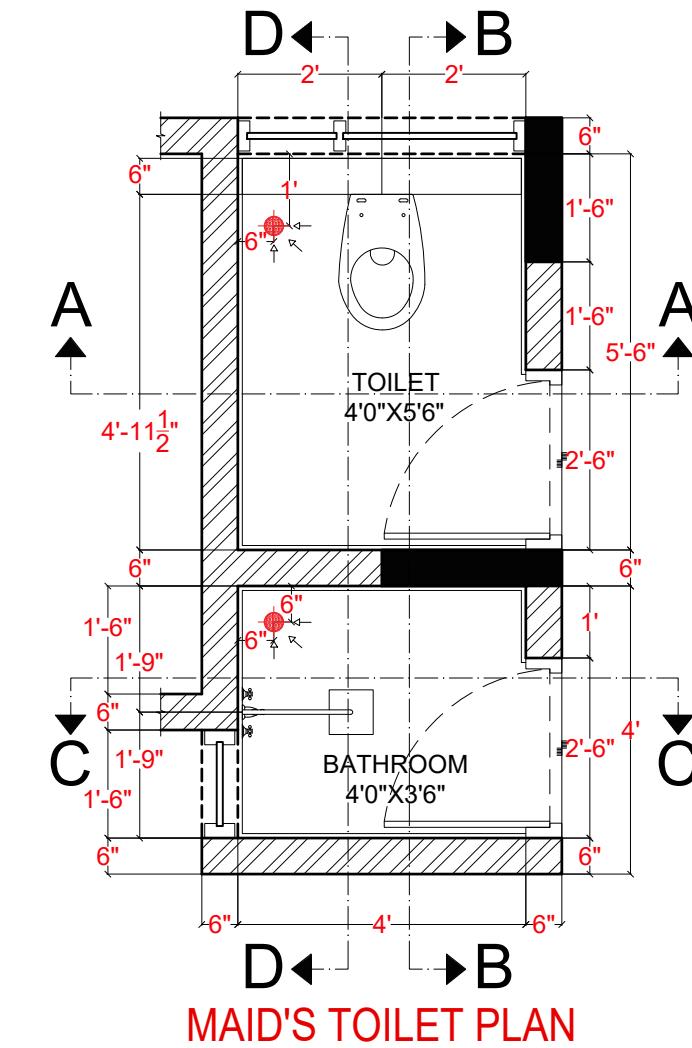


MAID'S TOILET PLAN




D. U. N. E


design unfiltered, a process never ending
54/2, 4th cross, Link road, Malleshwaram, Bangalore 560-003
designadune@gmail.com +91 23469351

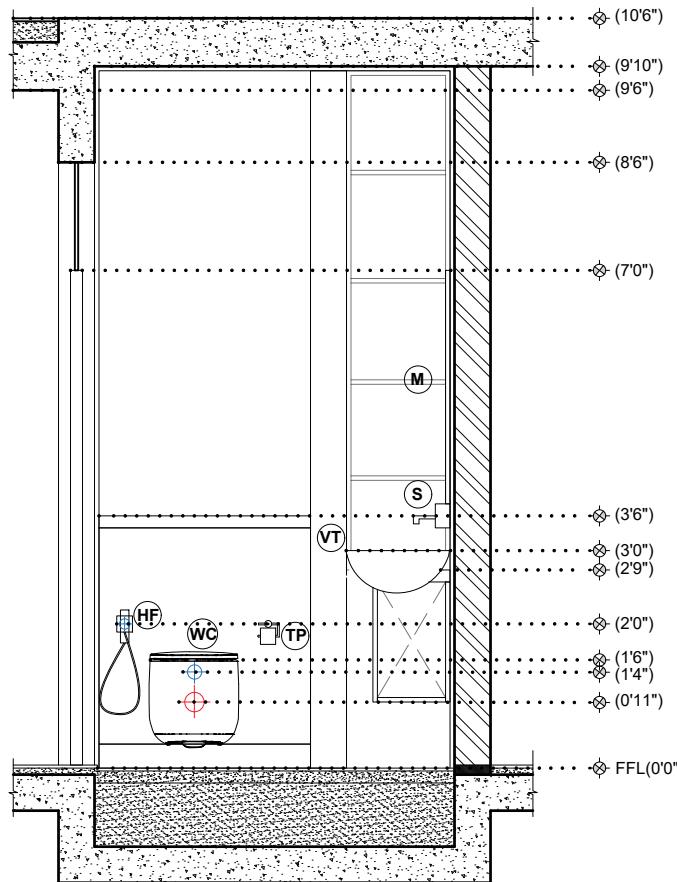


ELEVATION-AA

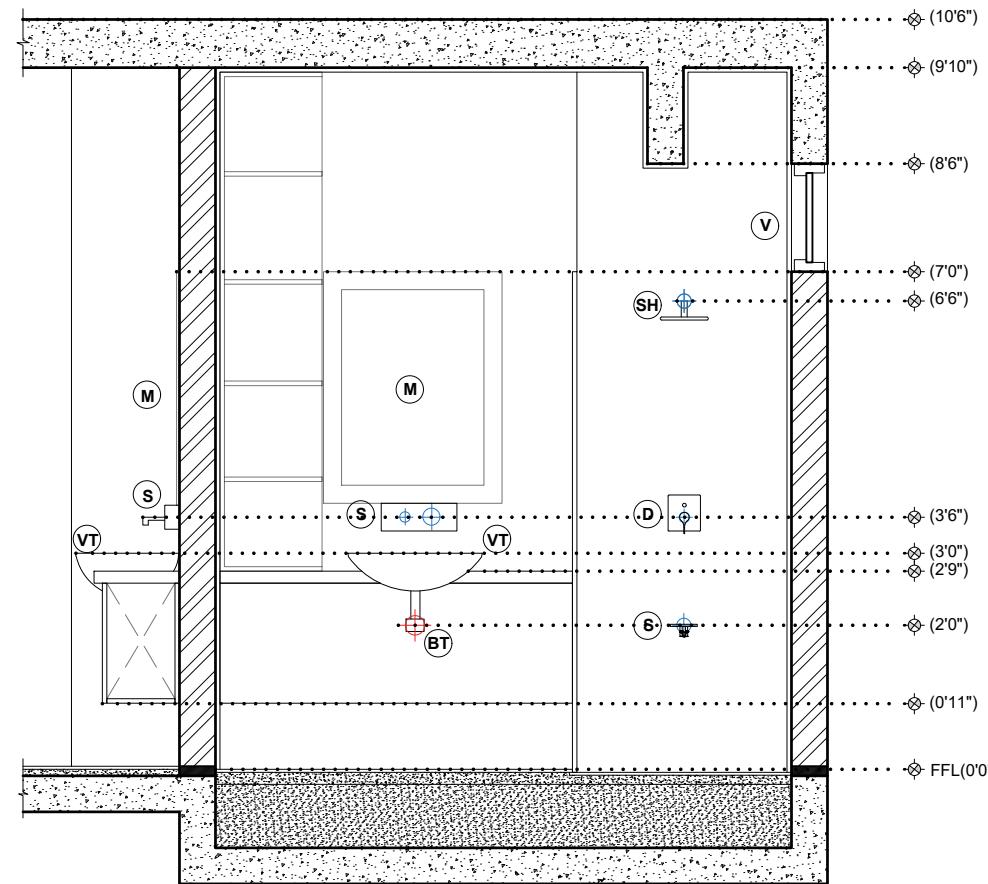

ELEVATION-BB

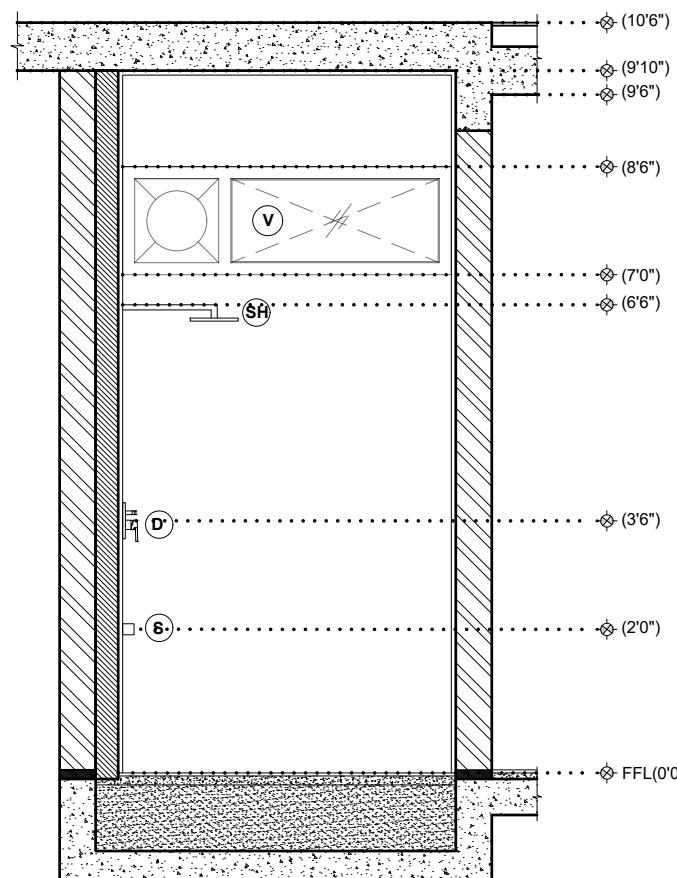

ELEVATION-CC

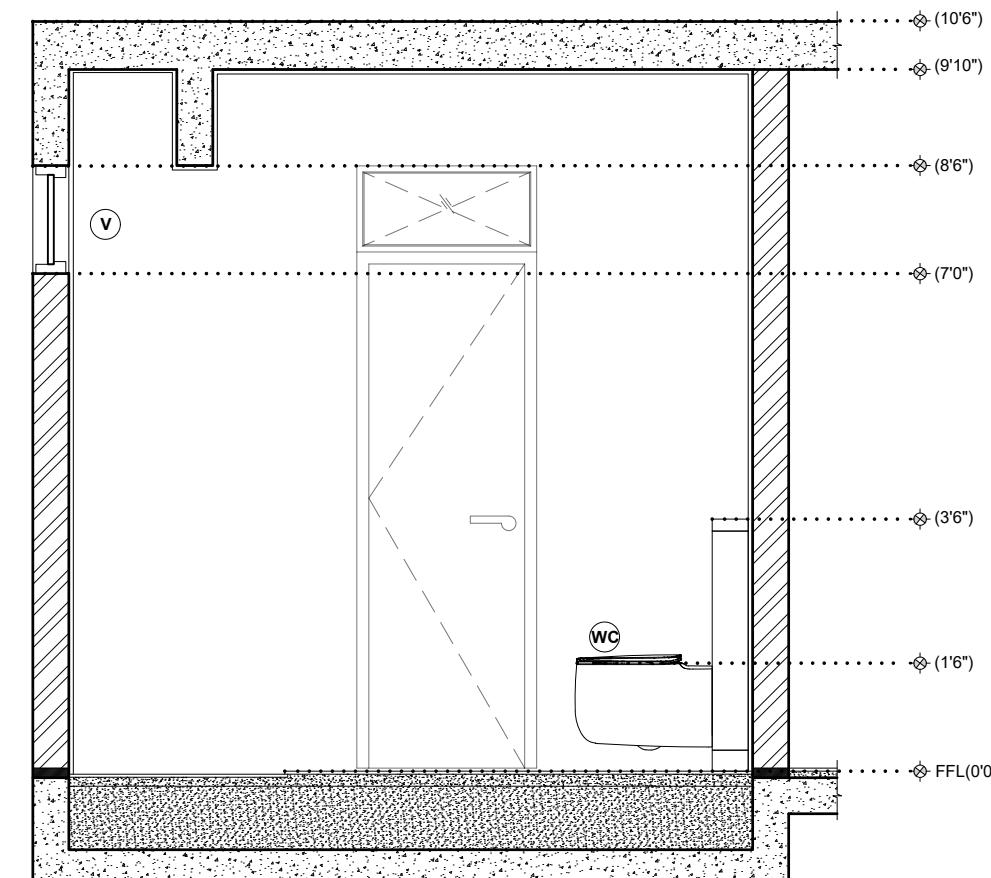

ELEVATION-DD

WC	WATER CLOSET	HF	HEALTH FAUCET
BT	BOTTLE TRAP	S	SPOUT
VT	VANITY TOP	D	DIVERTOR
V	VENTILATOR	FP	FLUSH PLATE
SH	SHOWER HEAD	FWP	FRESH WATER PIPE
TP	TISSUE PAPER HOLDER	WWP	WASTE WATER PIPE

AREA

1. WALL AREA = 268 SQFT


2. FLOOR AREA = 44 SQFT

FIXTURES

1. WC -WALL HUNG

2. BASIN - SEMI RECESSED

3. SHOWER-SINGLE LIVER
DIVERTER WITH 3 WAY
OUT

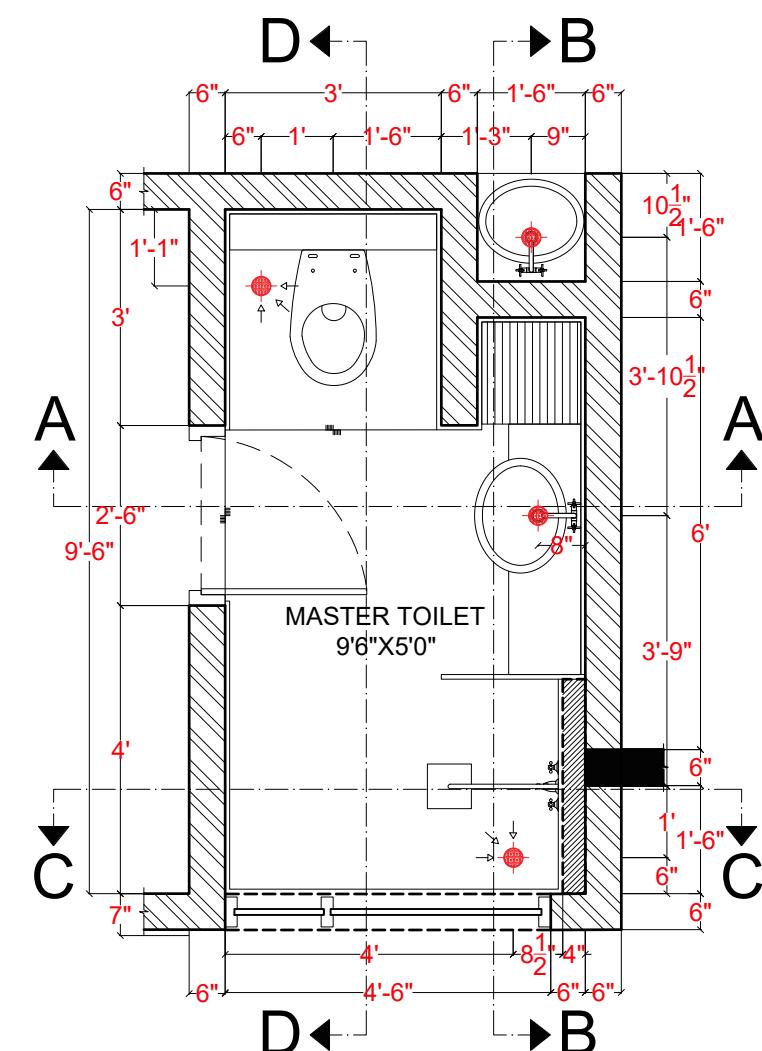

MASTER TOILET PLAN

"FOR ESTIMATION PURPOSE ONLY"
"PLUMBING DRAWING MAY CHANGE
BASED ON FIXTURE SELECTIONS"

PROJECT CODE
AATG

DRAWING NUMBER
WD-004

REVISION NUMBER
0



PROJECT

PROPOSED RESIDENCE
FOR AADHYA ATG

DRAWING TITLE

WORKING DRAWING

DRAWING TITLE

PLUMBING DRAWINGS

DATE 16 - 11 - 2022

SCALE 3/8 = 1'0"

PRINT ON A3

DRAWN BY JISHNU.K


CHECKED BY THEERTHAK

NOTE


"FOR ESTIMATION PURPOSE ONLY"
"PLUMBING DRAWING MAY CHANGE
BASED ON FIXTURE SELECTIONS"

D. U. N. E


design unfiltered, a process never ending
54/2, 4th cross, Link road, Malleshwaram, Bangalore 560-003
designadune@gmail.com +91 23469351

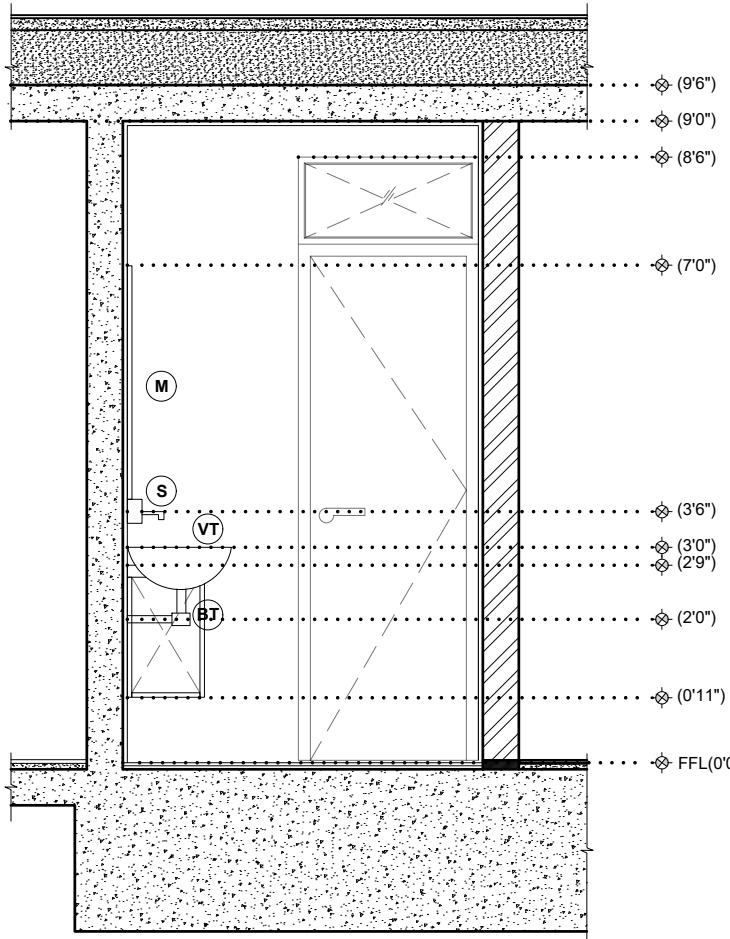


ELEVATION-AA

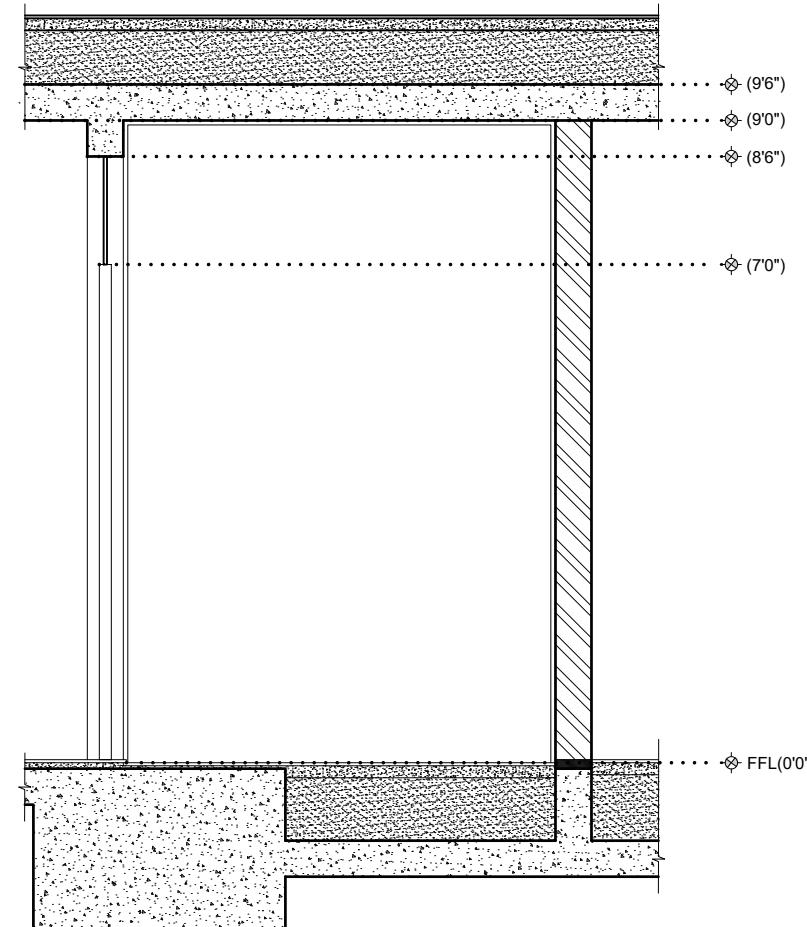

ELEVATION-BB

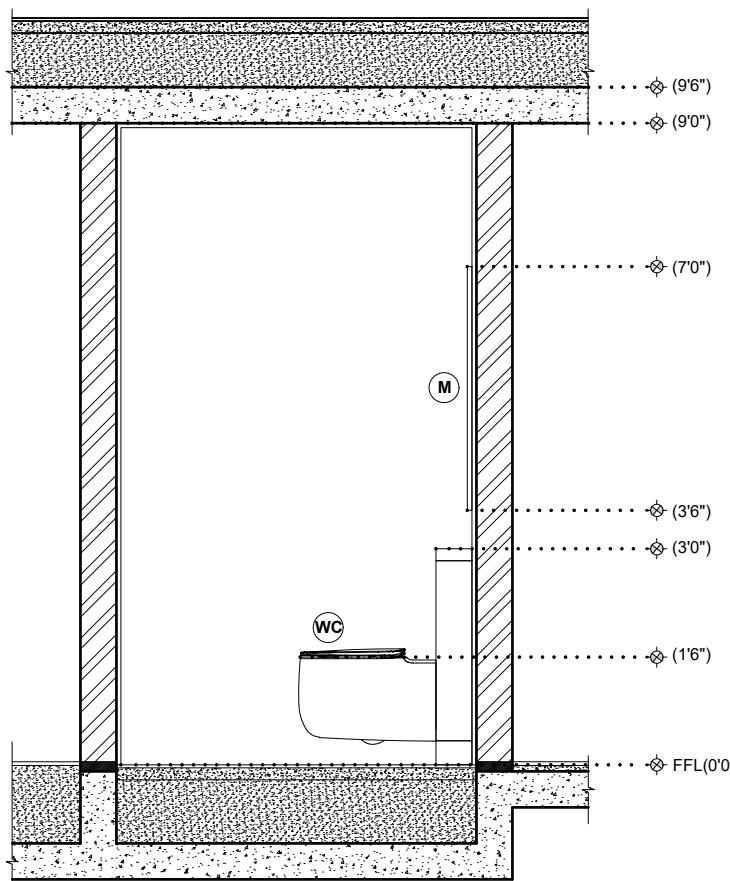

ELEVATION-CC

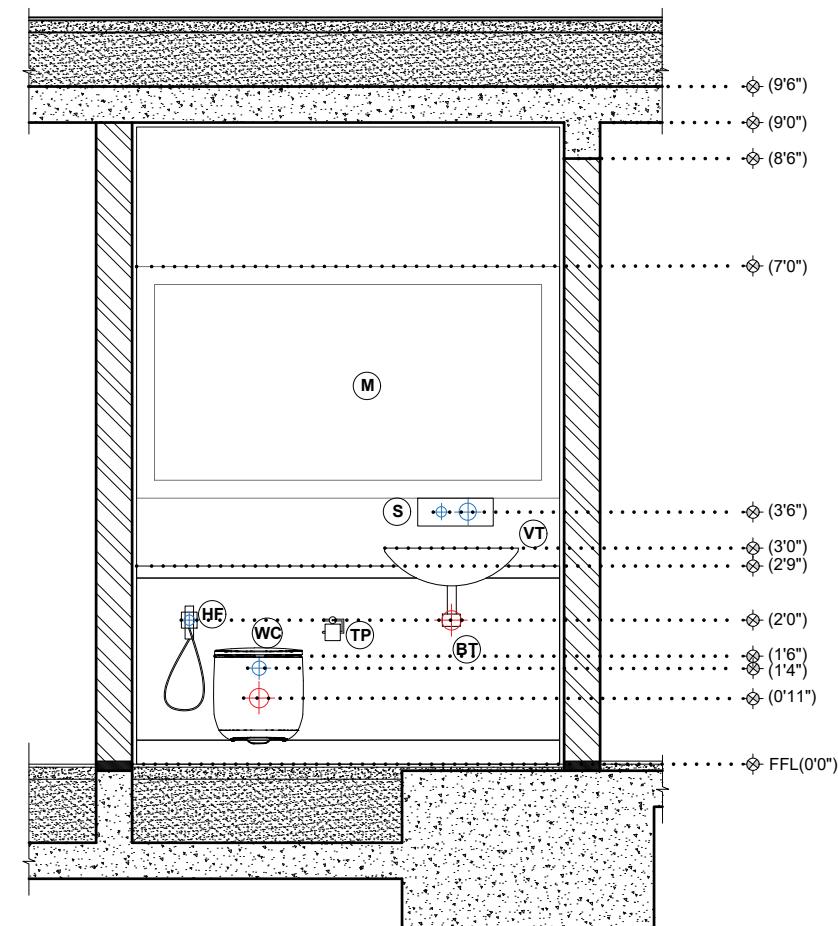


ELEVATION-DD

WC	WATER CLOSET	HF	HEALTH FAUCET
BT	BOTTLE TRAP	S	SPOUT
VT	VANITY TOP	D	DIVERTOR
V	VENTILATOR	FP	FLUSH PLATE
SH	SHOWER HEAD		FRESH WATER PIPE
TP	TISSUE PAPER HOLDER		WASTE WATER PIPE

AREA FIXTURES

- 1. WALL AREA = 196 SQFT
- 2. FLOOR AREA = 30 SQFT
- 1. WC -WALL HUNG
- 2. BASIN - SEMI RECESSED

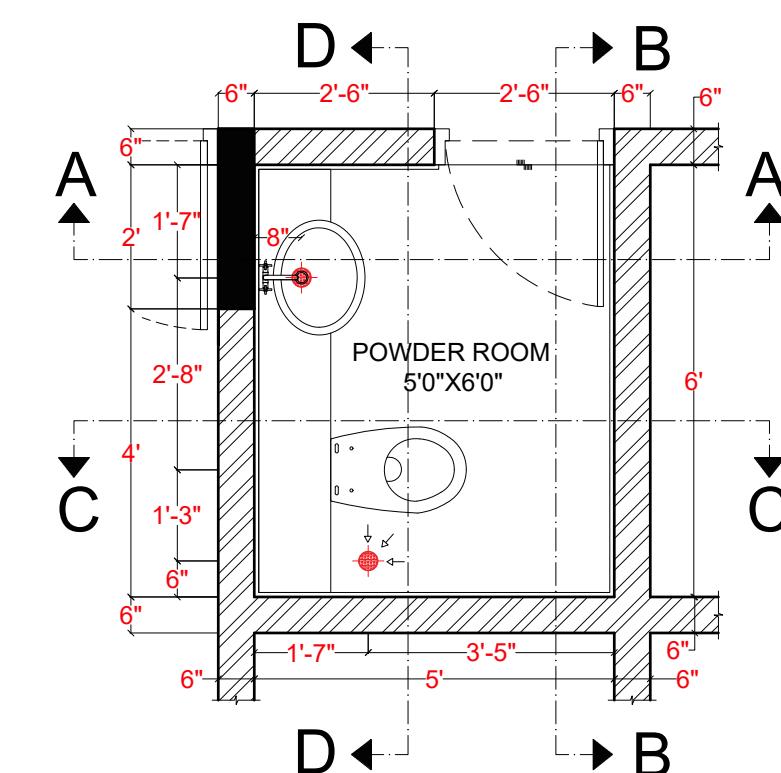

POWDER ROOM PLAN

PROJECT

PROPOSED RESIDENCE
FOR AADHYA ATG

DRAWING TITLE

WORKING DRAWING

DRAWING TITLE

PLUMBING DRAWINGS

DATE 16 - 11 - 2022

SCALE $\frac{3}{8}$ = 1'0"

PRINT ON A3

DRAWN BY JISHNU.K

CHECKED BY THEERTHAK

NOTE

"FOR ESTIMATION PURPOSE ONLY"
"PLUMBING DRAWING MAY CHANGE
BASED ON FIXTURE SELECTIONS"

PROJECT CODE AATG

DRAWING NUMBER WD-004

REVISION NUMBER 0



FLOORING DETAIL

D. U. N. E

design unfiltered; a process never ending
54/2, 4th cross, Link road, Malleshwaram, Bangalore 560-003
designadune@gmail.com +91 23469351

PROJECT

RENOVATION OF
SKYGARDEN

DRAWING TITLE

WORKING DRAWING

DRAWING TITLE

16-A FLOORING

DATE 17 - 05 - 2025
SCALE $\frac{1}{8}$ " = 1'0"
PRINT ON A3
DRAWN BY JISHNU.K
CHECKED BY THEERTHAK

NOTE

PROJECT CODE

SKY

DRAWING NUMBER WD-002

REVISION NUMBER

0

TOTAL AREA=1742 SQFT

TOTAL AREA=288 SQFT

TOTAL AREA=484 SQFT

TOTAL AREA=143 SQFT

TOTAL AREA=279 SQFT


TOTAL AREA=165 SQFT

TOTAL AREA=179 SQFT

TOTAL AREA=528 SQFT

TOTAL AREA=635SQFT

TOTAL AREA=471 SQFT

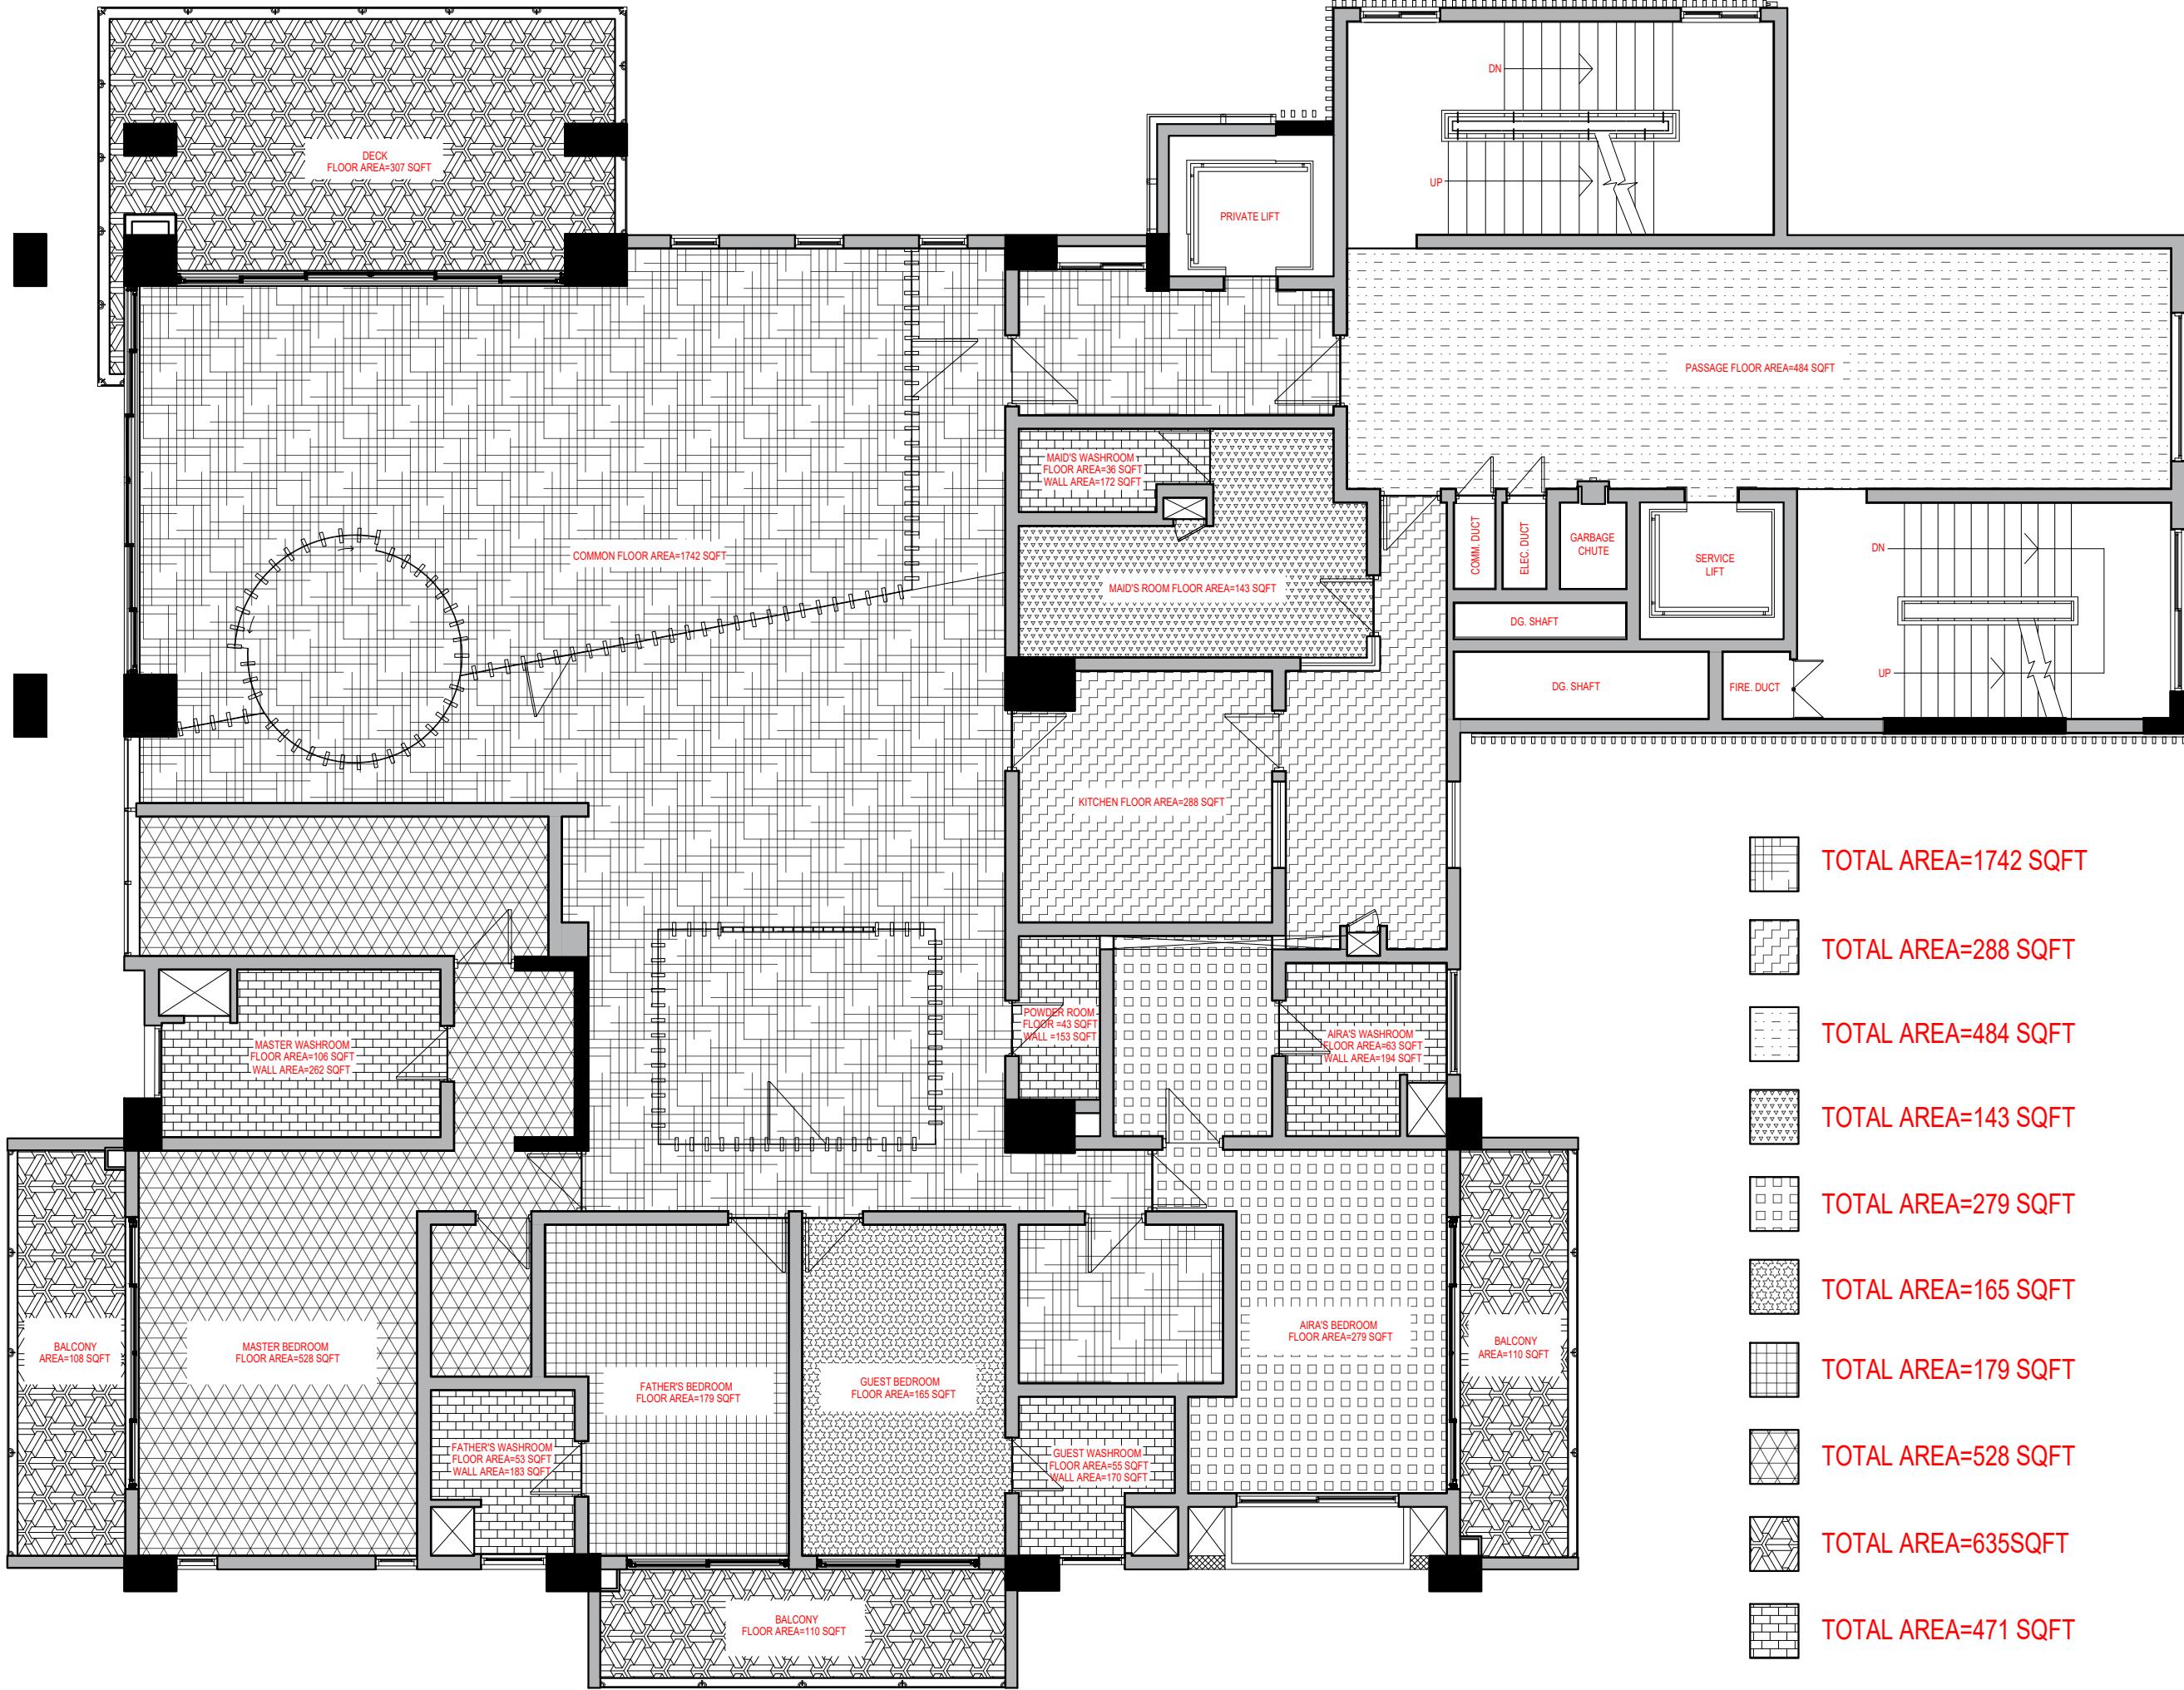

DETAILS

D. U. N. E

design unfiltered; a process never ending
54/2, 4th cross, Link road, Malleshwaram, Bangalore 560-003
designadune@gmail.com +91 23469351

PROJECT

PROPOSED RESIDENCE
FOR BALAJI

DRAWING TITLE

WORKING DRAWING

DRAWING TITLE

CONCRETE STAIRCASE
DETAILS

DATE 09 - 07 - 2025

SCALE NOT IN SCALE

PRINT ON A3

DRAWN BY JISHNU.K

CHECKED BY THEERTHAK

NOTE

PROJECT CODE



BALAJI

DRAWING NUMBER


WD-001

REVISION NUMBER


0

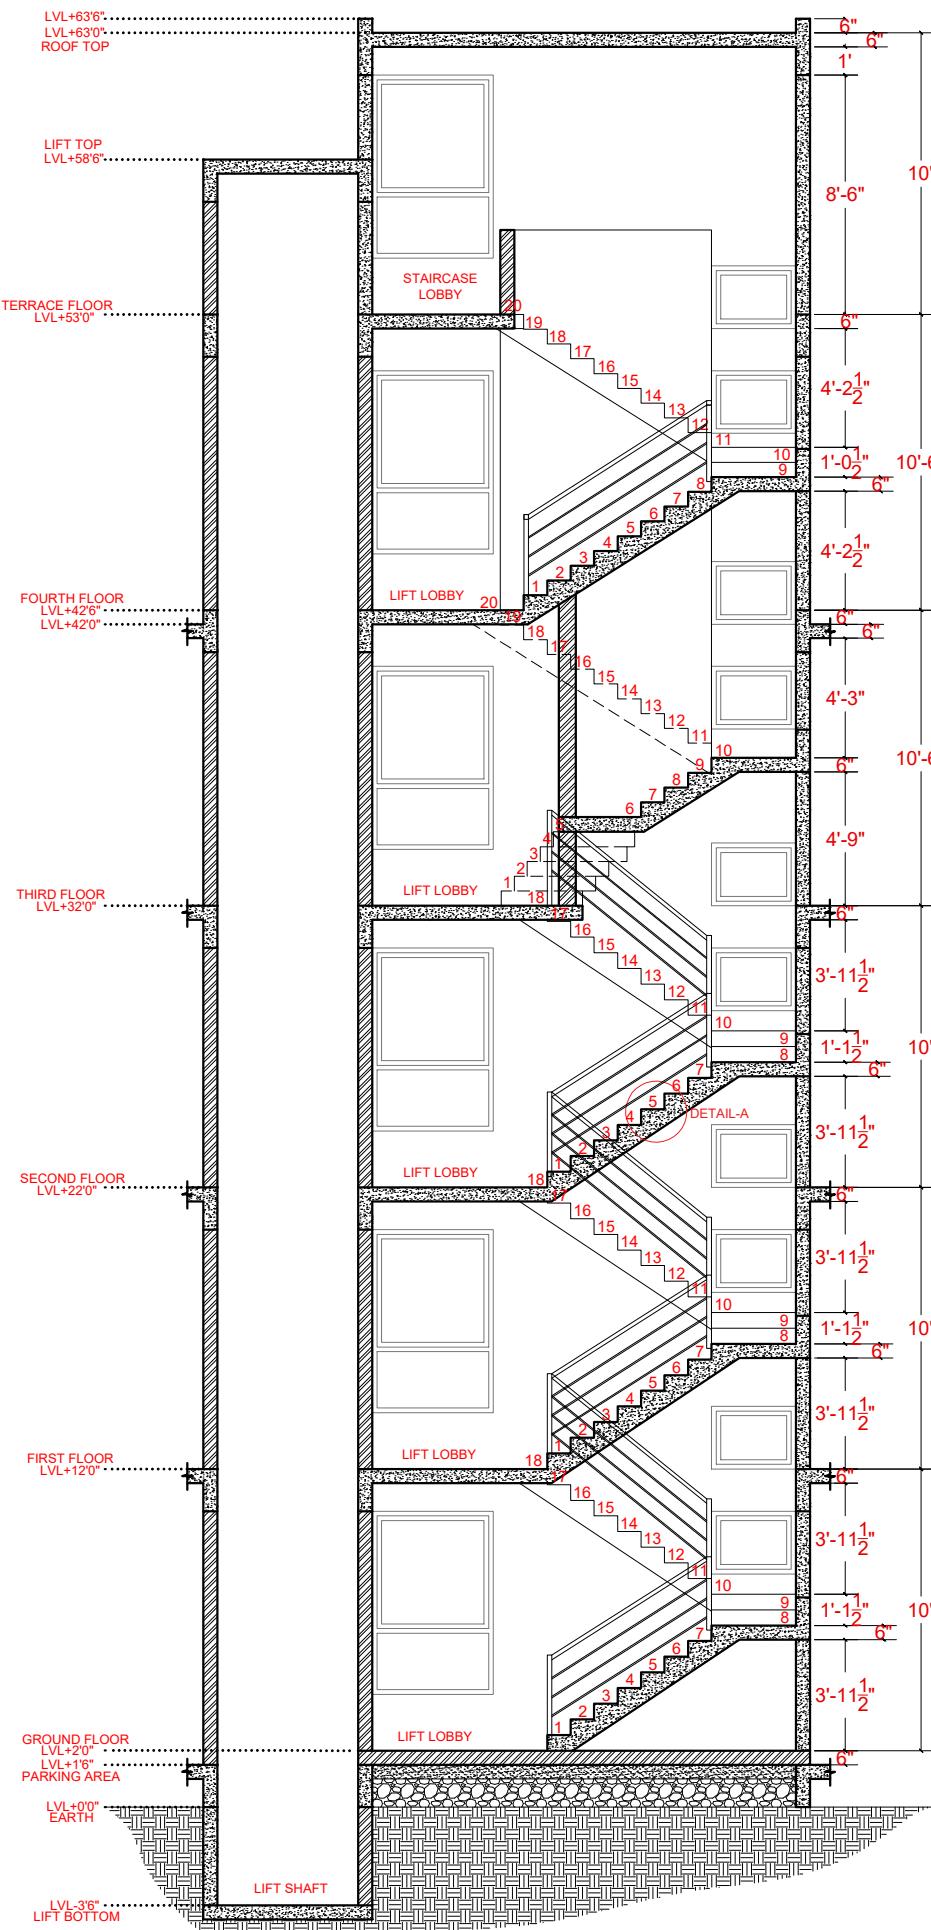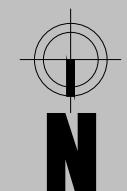


SECTION-AA

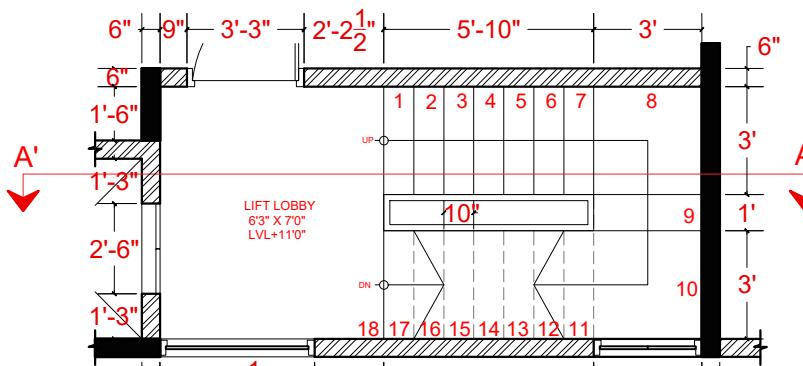


TYPICAL FLOOR STAIRCASE PLAN

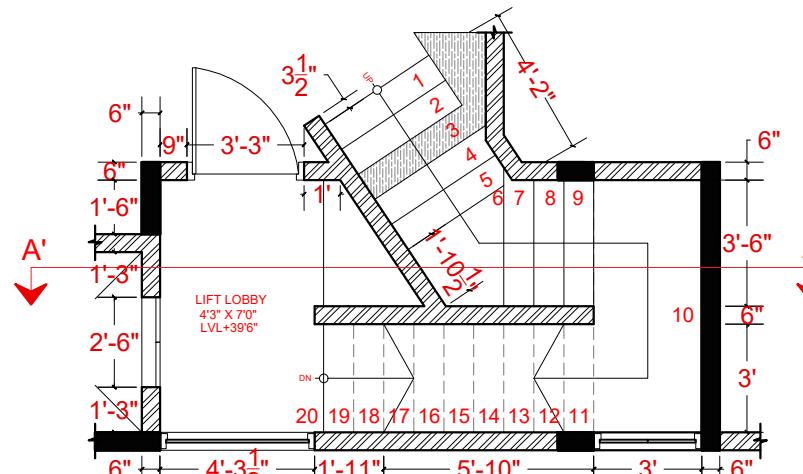


THIRD FLOOR STAIRCASE PLAN

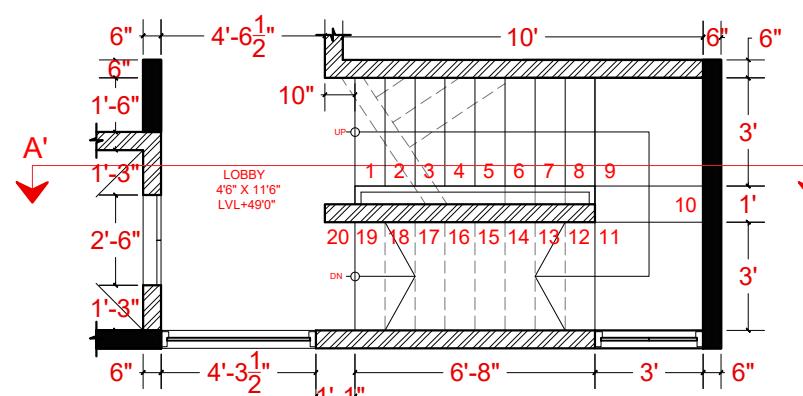


FOURTH FLOOR STAIRCASE PLAN

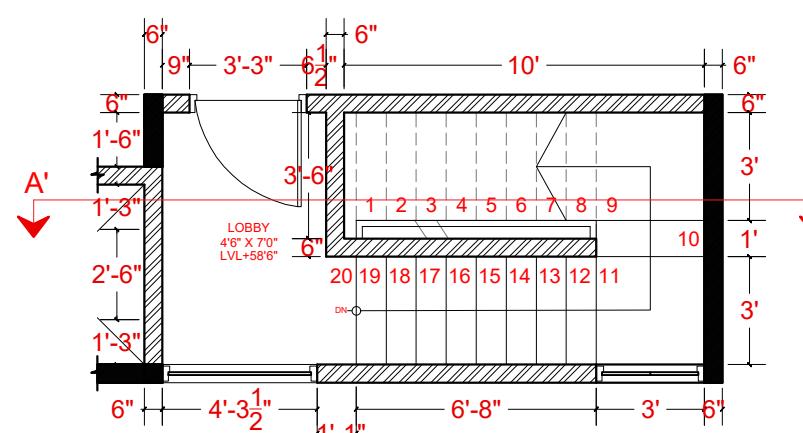


TERRACE FLOOR STAIRCASE PLAN

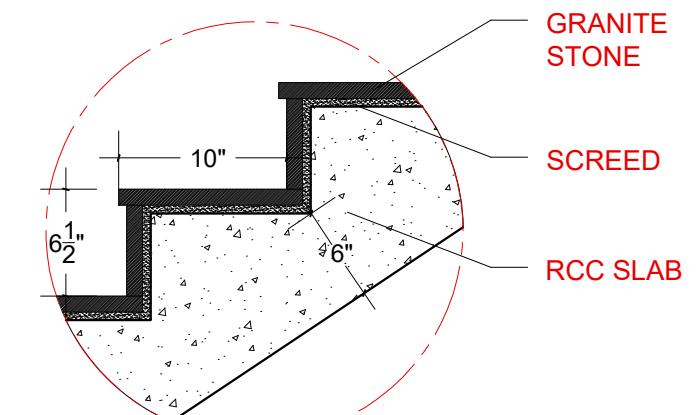


DETAIL-A

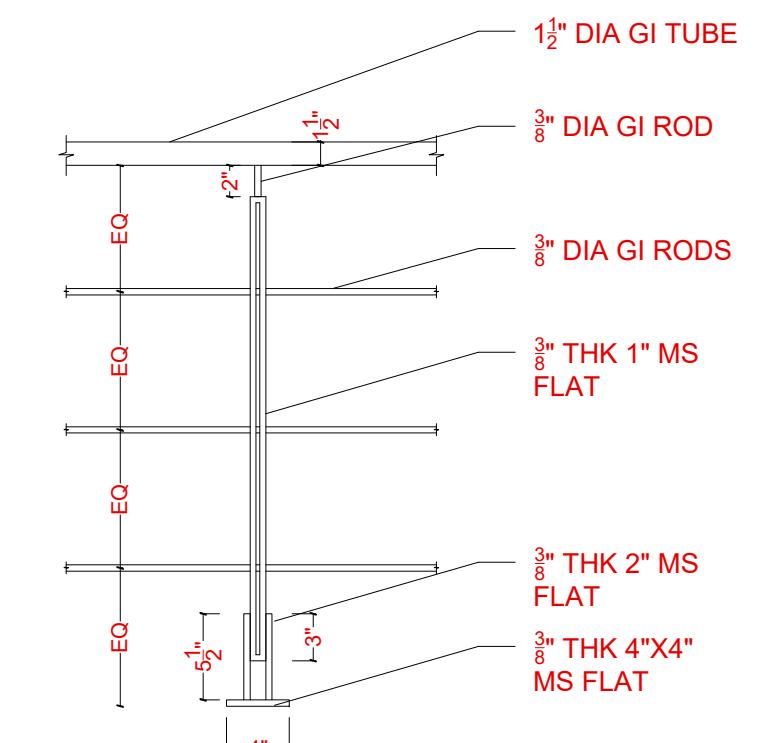

BALUSTRADE ELEVATION

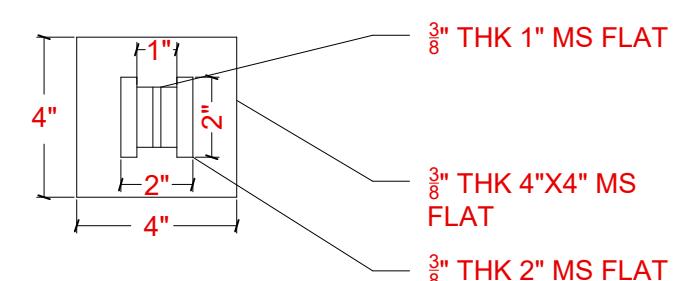

BALUSTRADE PLAN

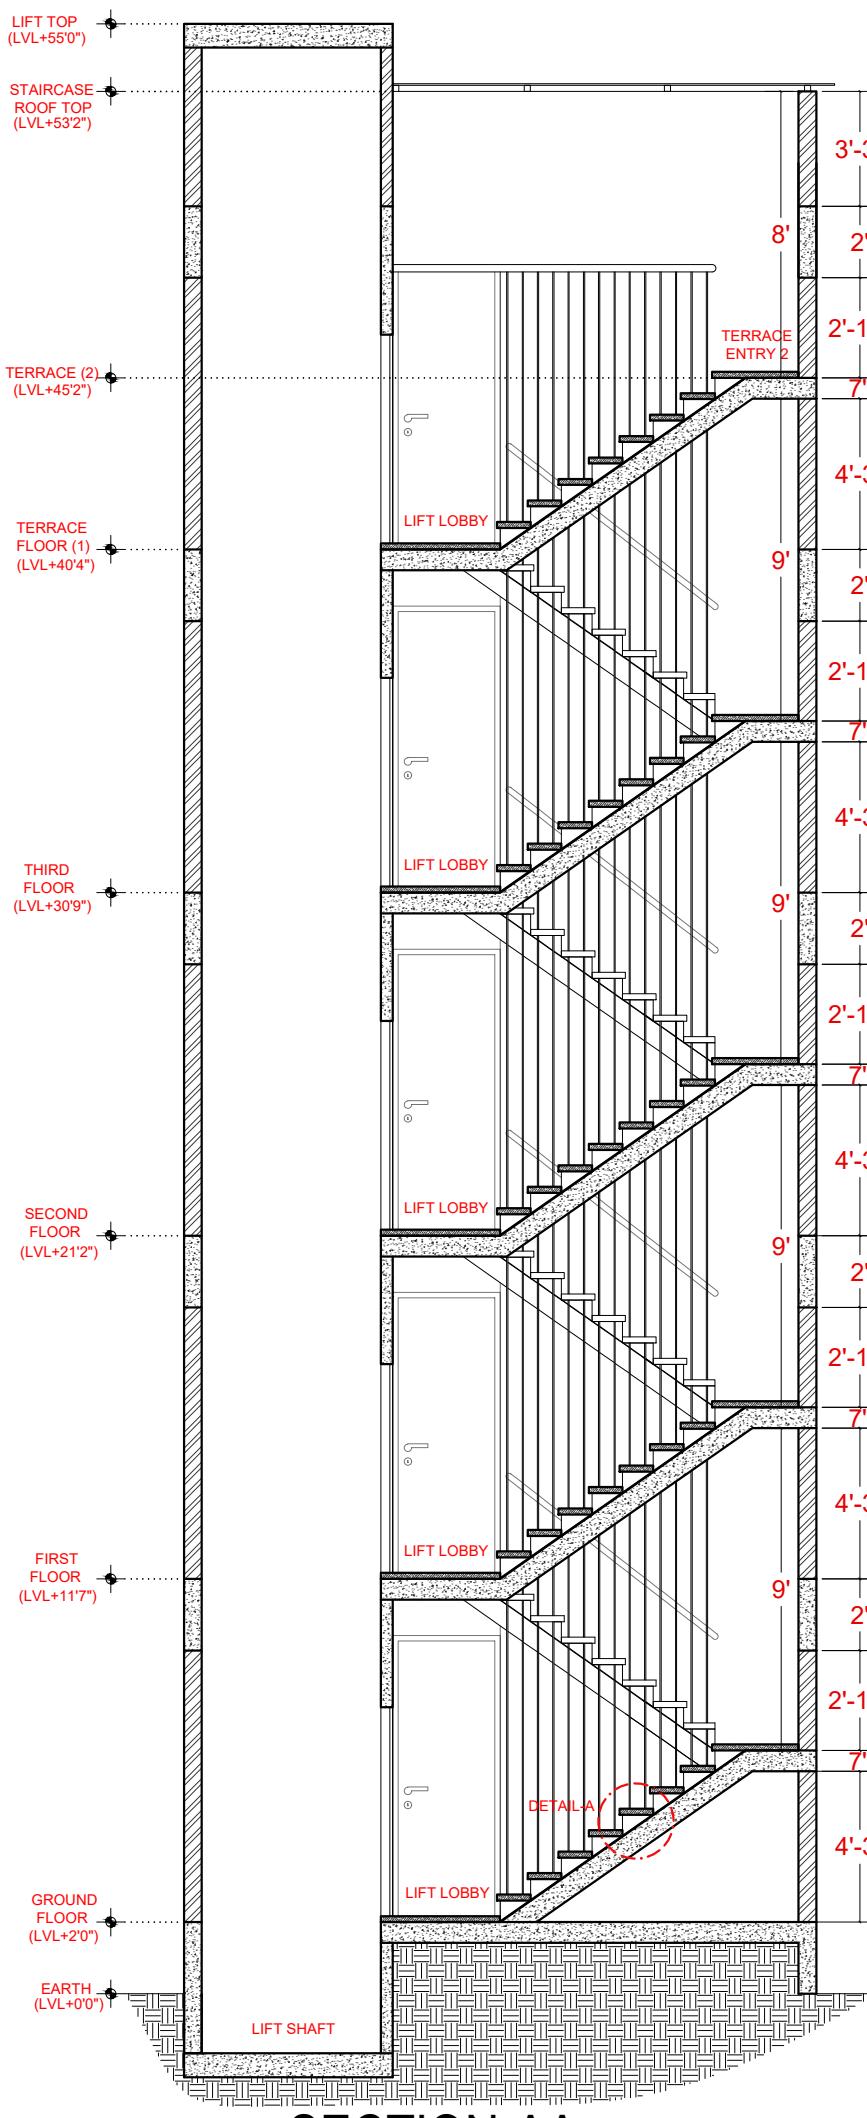

SECTION-AA

STAIRCASE PLAN

DETAIL-A

D. U. N. E

design unfiltered; a process never ending
54/2, 4th cross, Link road, Malleshwaram, Bangalore 560-003
designadune@gmail.com +91 23469351

PROJEC

PROPOSED RESIDENCE FOR GANGALAS

DRAWING TITLE

WORKING DRAWING

R.C.C SINGLE STRINGER STAIRCASE DETAILS

DATE 02-10-2023

SCALE

NOT IN SCALE


PRINT ON

DRAWN BY JISHNU.K

NOTE

PROJECT CODE

DRAWING NUMBER

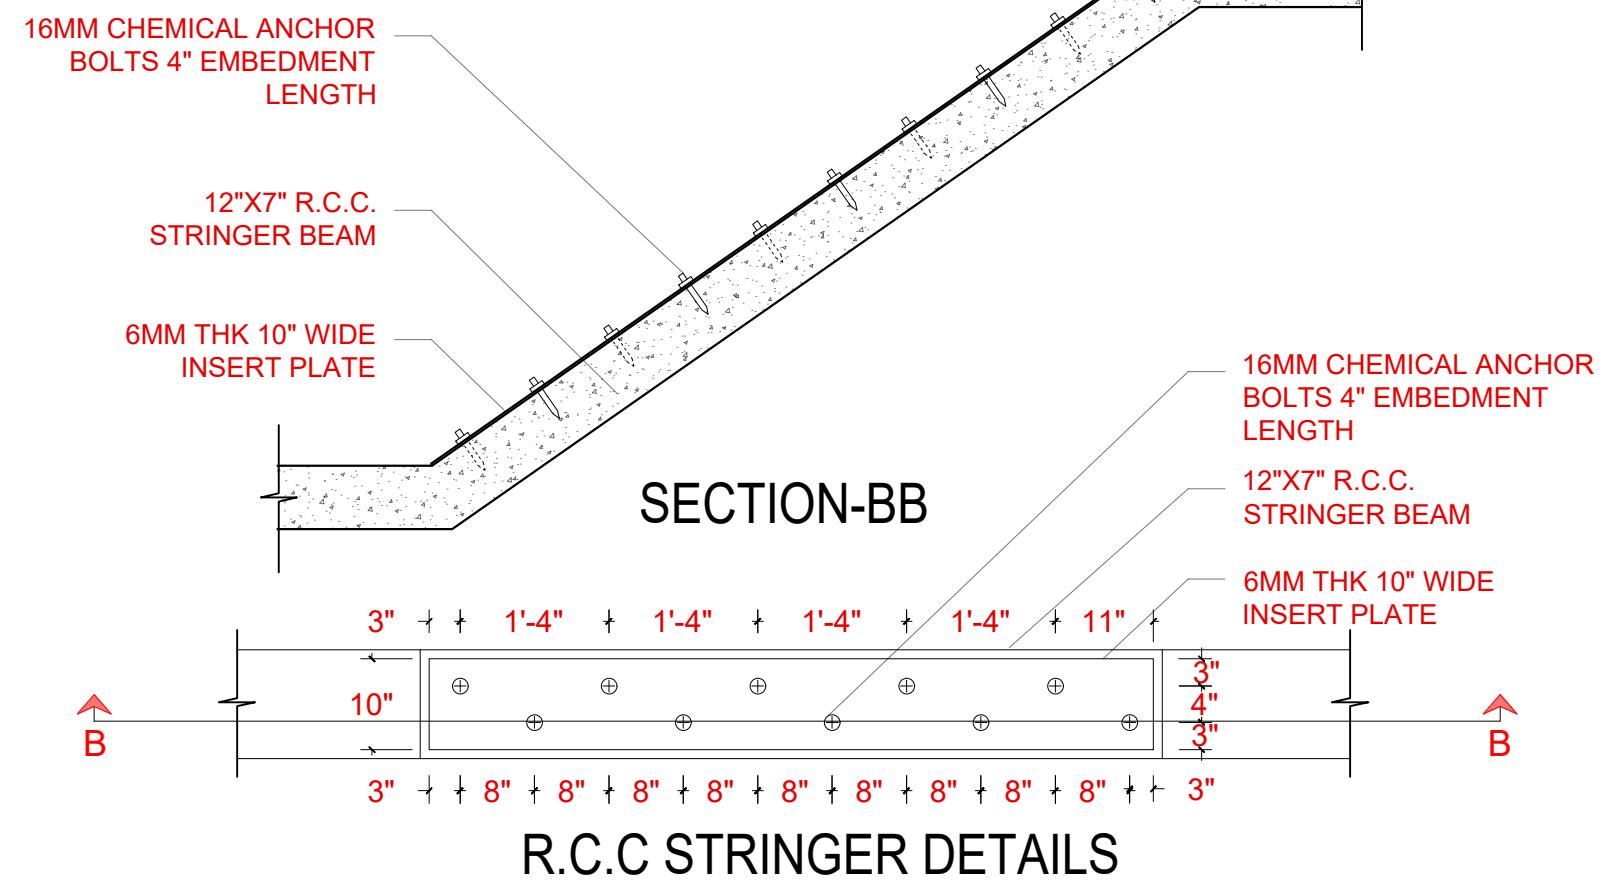

SECTION-C

ISOMETRIC VIEW

SECTION-CC

12M

3"

0"

3"

2" THK TIMBER

6MM PLATE BENT TO SHAPE

6MM PLATE WELDED TO 10" WIDE 6MM THK INSERT PLATE

12"X 7" EXISTING R.C.C STRINGER BEAM

The diagram illustrates a cross-section of a boat's deck structure. A horizontal beam at the top is supported by vertical posts. A diagonal brace extends from the bottom left towards the center. A label '10MM DIA SS ROPE' points to a line running vertically through the center of the structure. Another label '12MM DIA HOLE' points to a circular opening in one of the vertical supports.

2" THK TIMBER

10" WIDE 6MM THK
INSERT PLATE

CHEMICAL ANCHOR
DEPTH 4"

12"X 7" EXISTING
R.C.C STRINGER
BEAM

6MM PLATE BENT
TO SHAPE

D. U. N. E

design unfiltered; a process never ending
54/2, 4th cross, Link road, Malleshwaram, Bangalore 560-003
designadune@gmail.com +91 23469351

PROJECT

PROPOSED RESIDENCE
FOR DIVYA & RAMESH

DRAWING TITLE

WORKING DRAWING

DRAWING TITLE

SINGLE STRINGER
STAIRCASE DETAILS

DATE 06 - 01 - 2023

SCALE NOT IN SCALE

PRINT ON A3

DRAWN BY JISHNU.K

CHECKED BY THEERTHAK


NOTE

PROJECT CODE RDR



DRAWING NUMBER WD-001

REVISION NUMBER 0


N

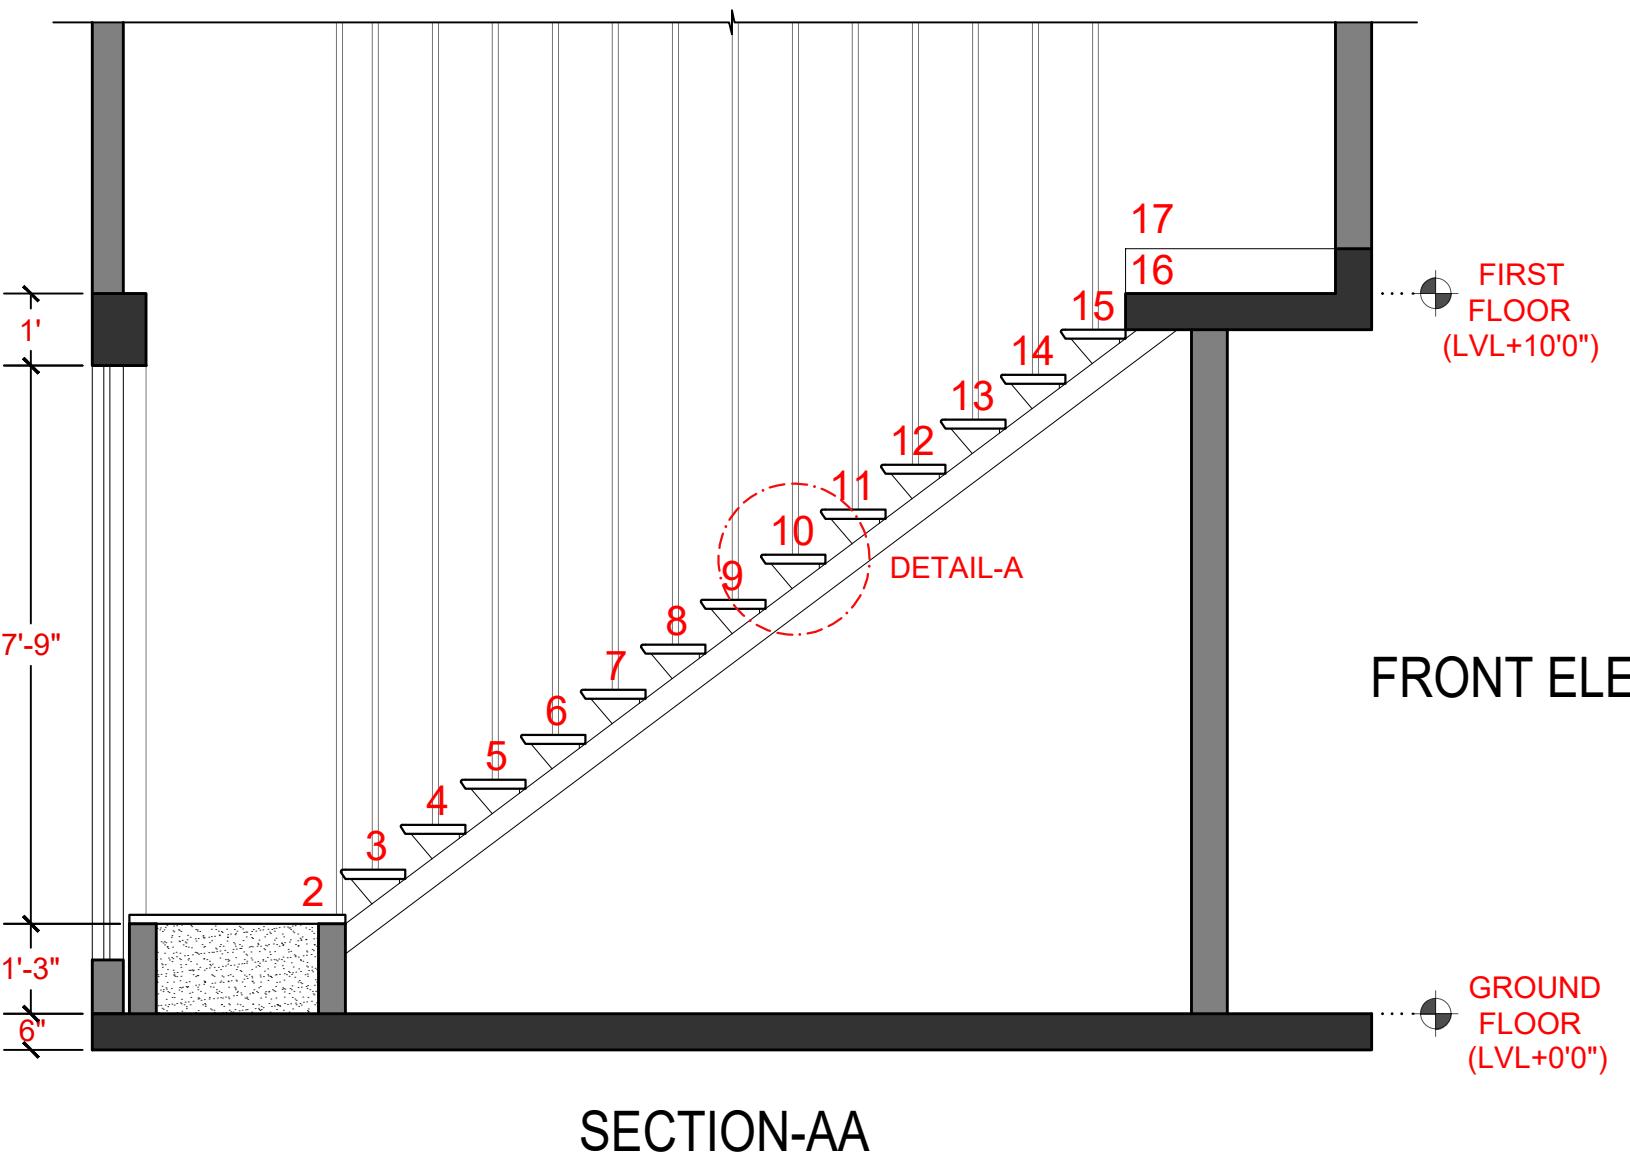


FRONT ELEVATION

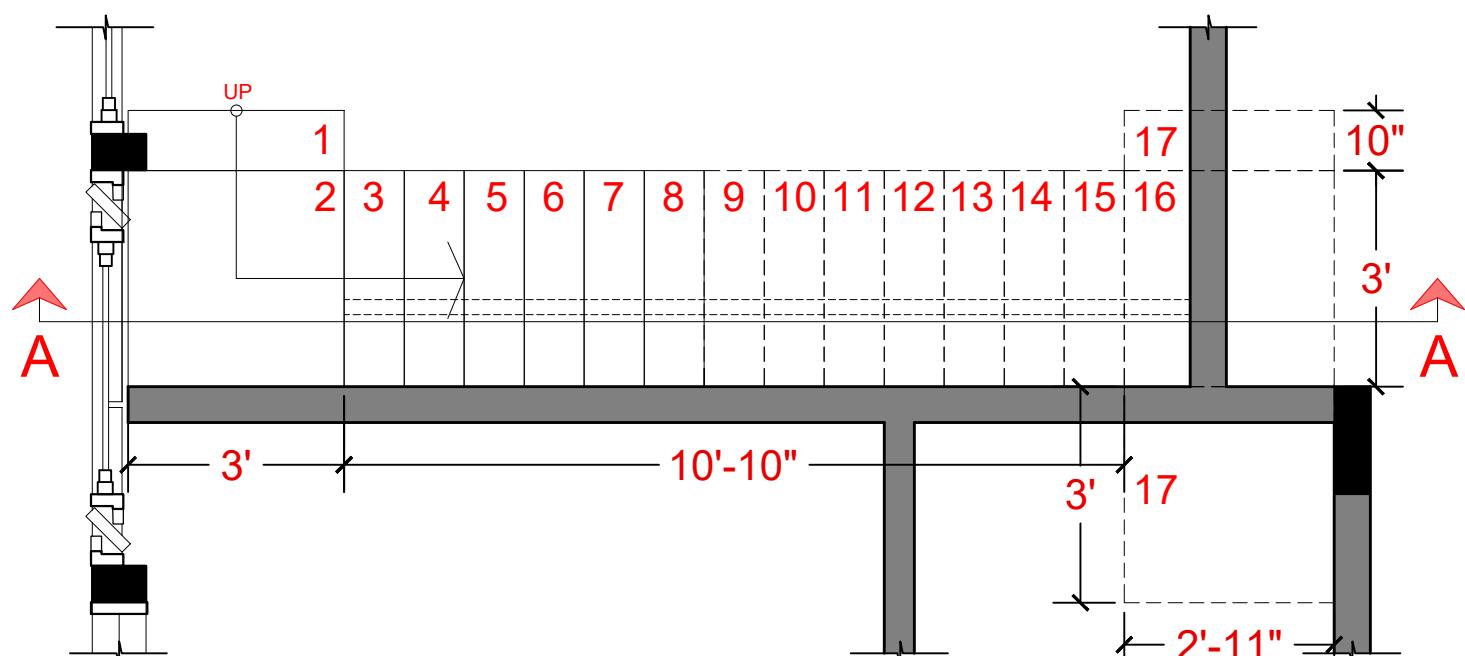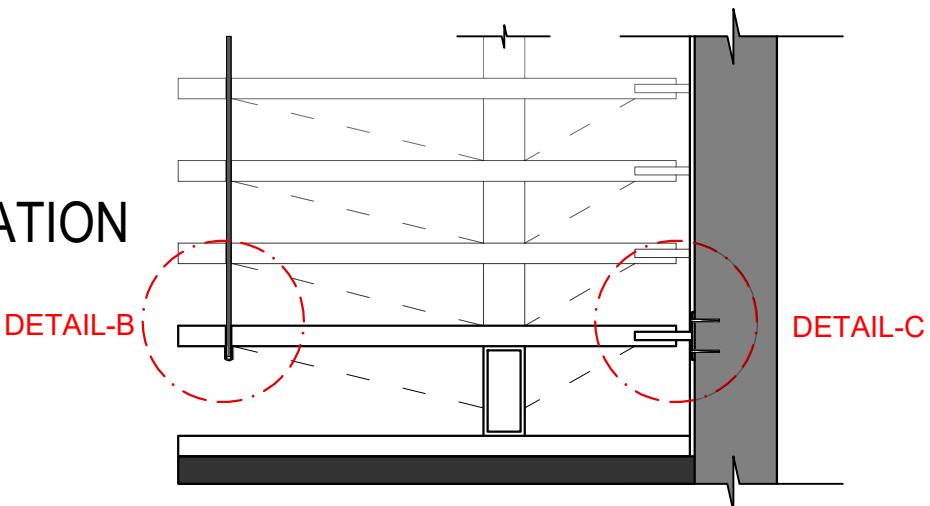


STAIRCASE PLAN

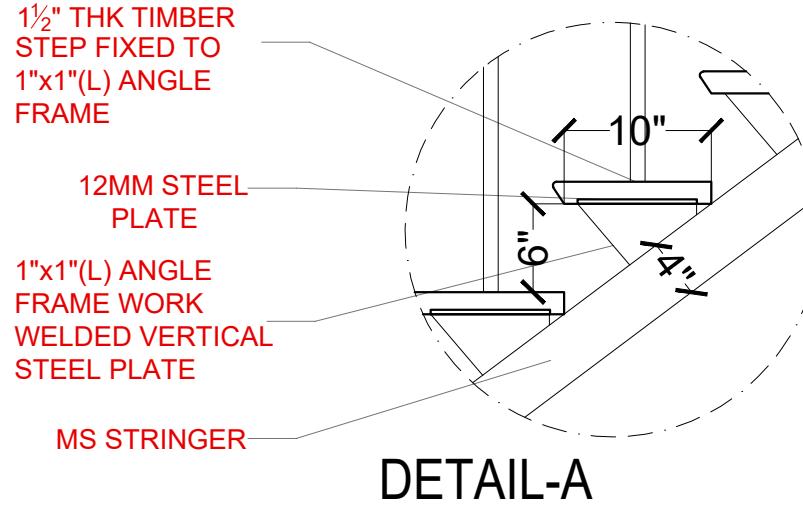

DETAIL-A

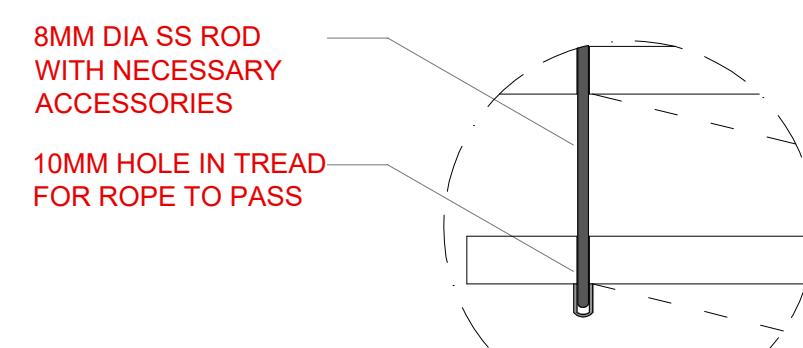

DETAIL-B

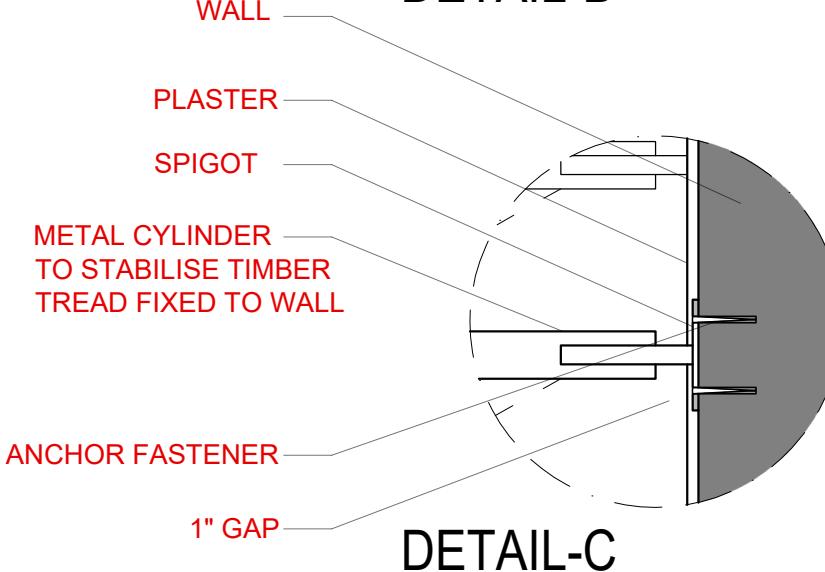

DETAIL-C

D. U. N. E

design unfiltered, a process never ending
54/2, 4th cross, Link road, Malleshwaram, Bangalore 560-003
designadune@gmail.com +91 23469351

PROJECT

PROPOSED RESIDENCE
FOR DIVYA & RAMESH

DRAWING TITLE

WORKING DRAWING

DRAWING TITLE

ELEVATION JAALI
DETAILS

DATE 05 - 01 - 2023

SCALE $\frac{1}{8}$ " = 1'0"

PRINT ON A3

DRAWN BY JISHNU.K



CHECKED BY THEERTHAK

NOTE

PROJECT CODE RDR

DRAWING NUMBER WD-001

REVISION NUMBER 0

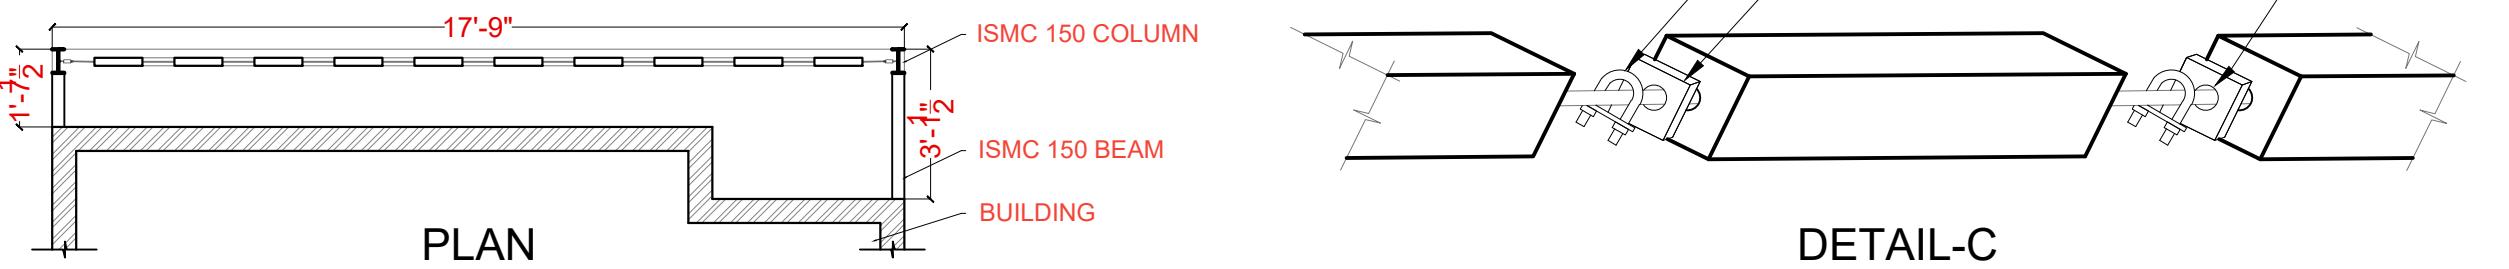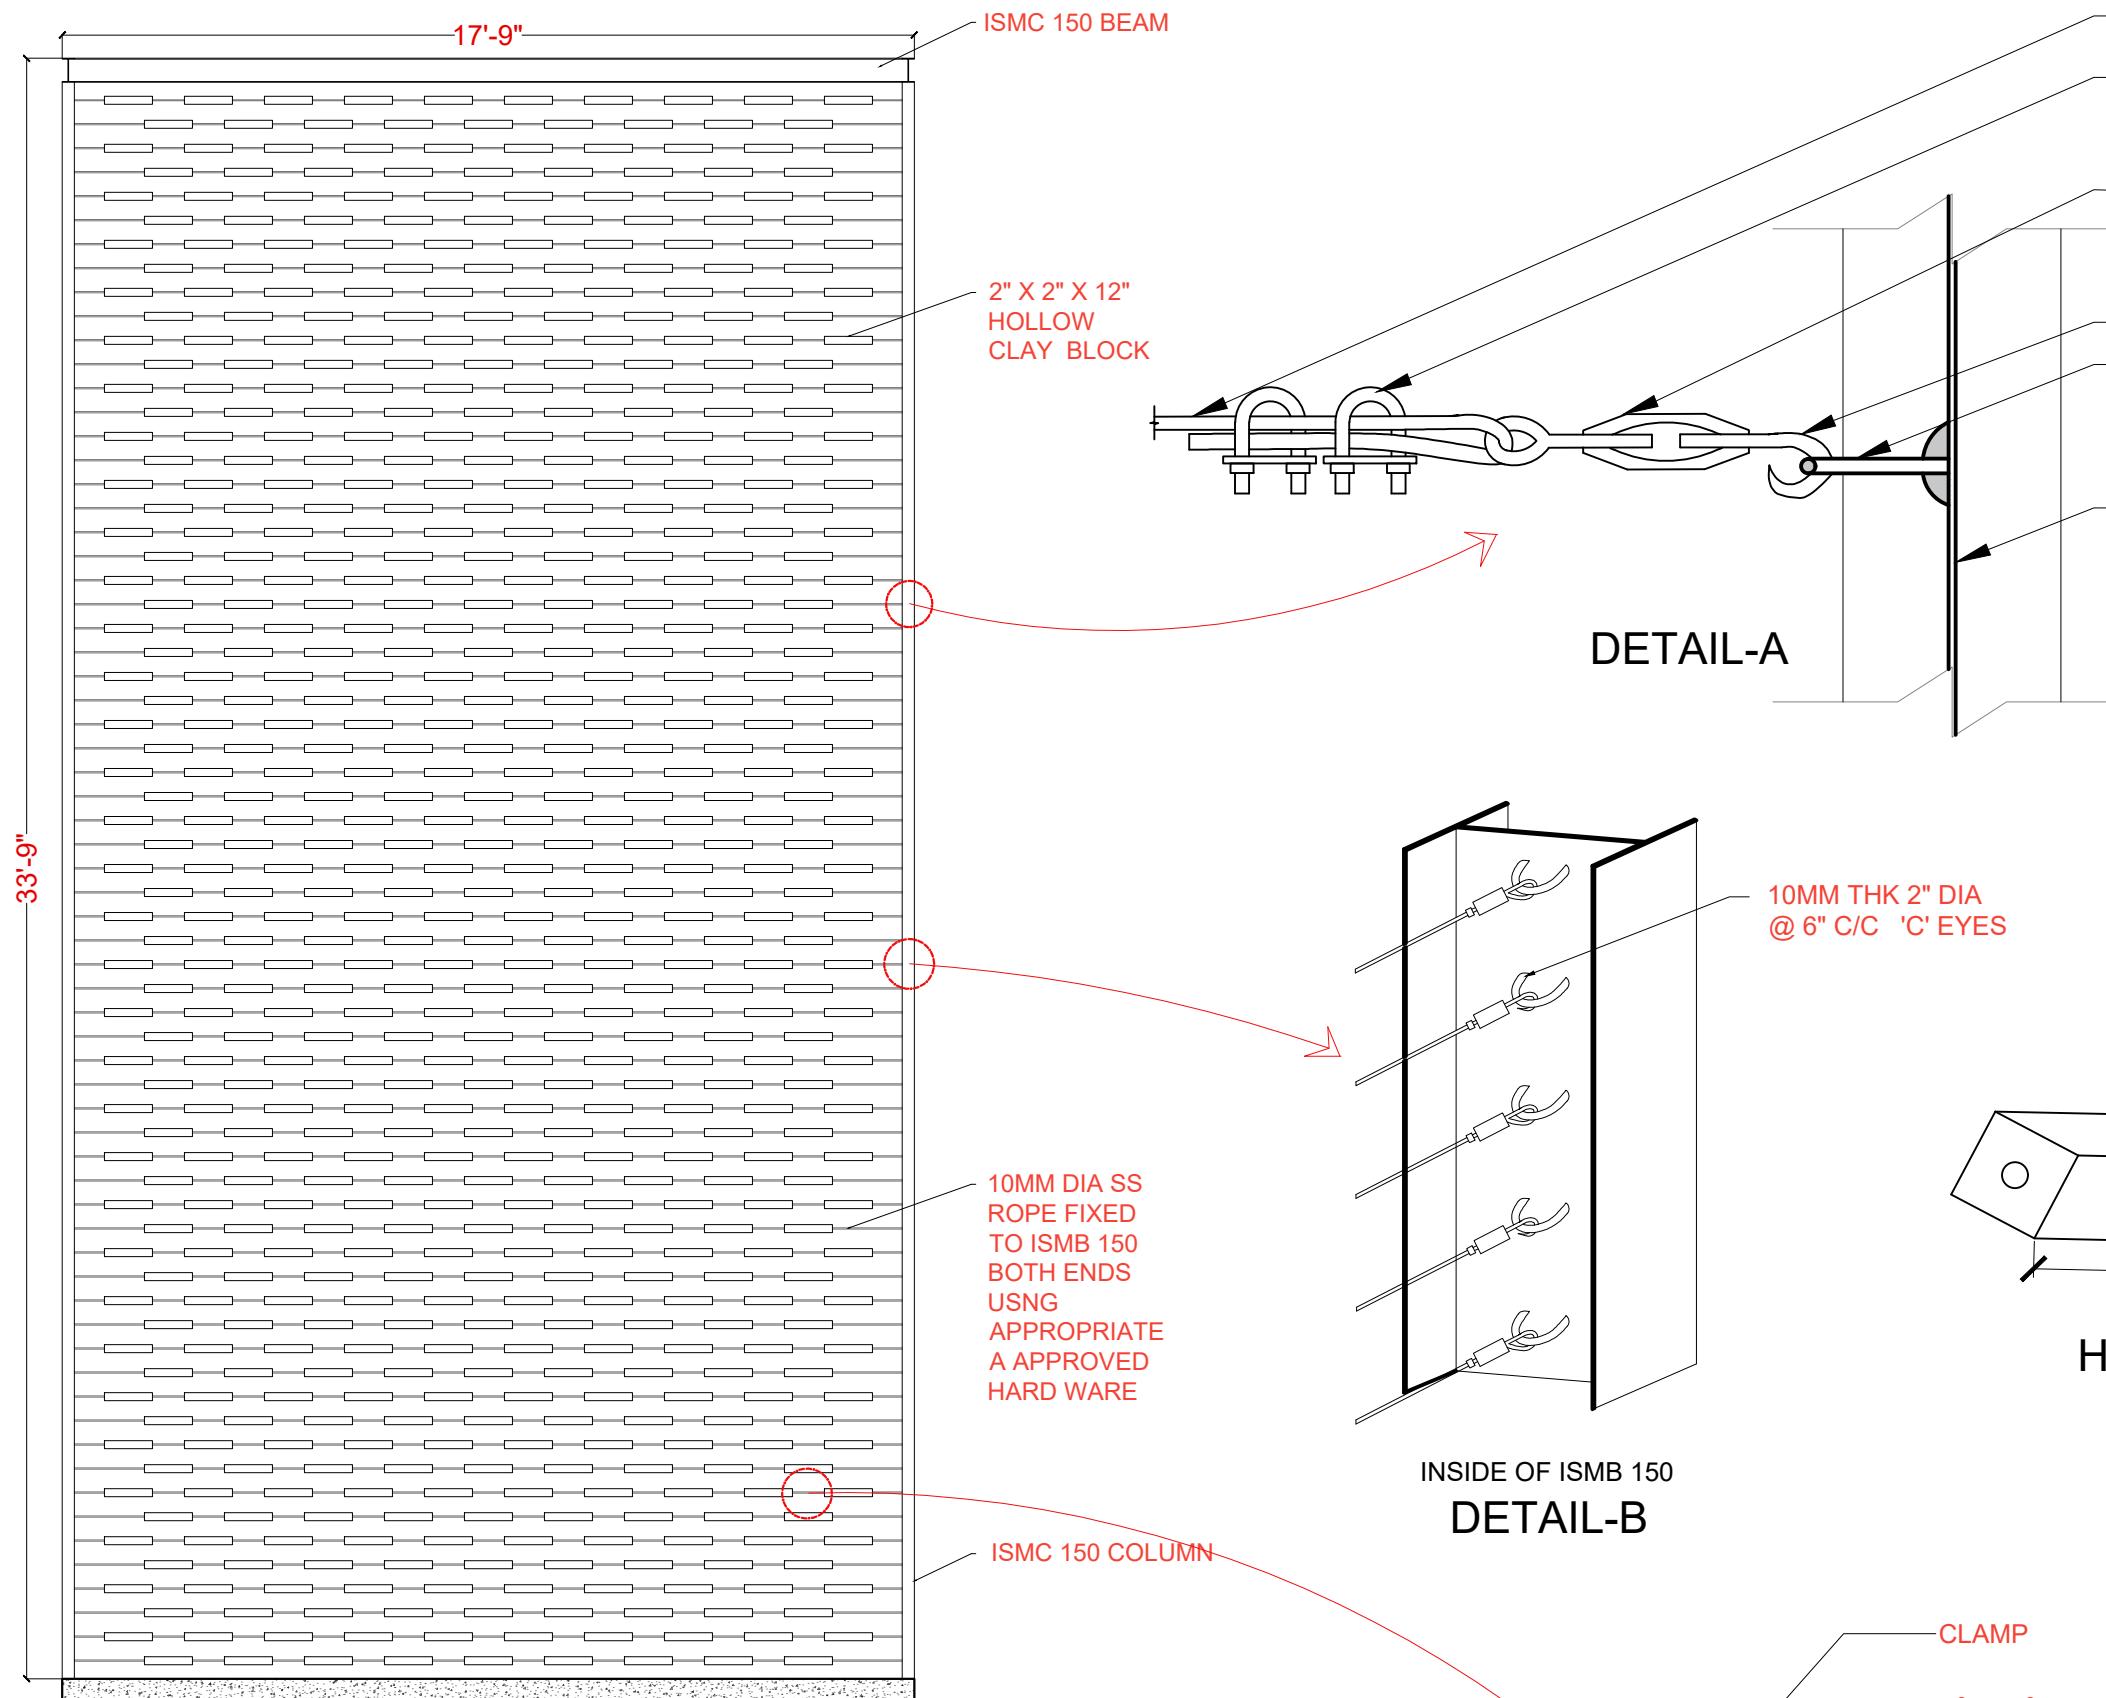

D. U. N. E

design unfiltered, a process never ending
54/2, 4th cross, Link road, Malleshwaram, Bangalore 560-003
designdune@gmail.com +91 23469351

PROJECT

JYOTHY COLLAGE

DRAWING TITLE

WORKING DRAWING

DRAWING TITLE

STEEL ELEVATION DETAILS

DATE 16 - 11 - 2022

SCALE NOT IN SCALE

PRINT ON A3

DRAWN BY JISHNU.K


CHECKED BY THEERTHAK

NOTE


PROJECT CODE JYOTHY

DRAWING NUMBER WD-002


REVISION NUMBER 0

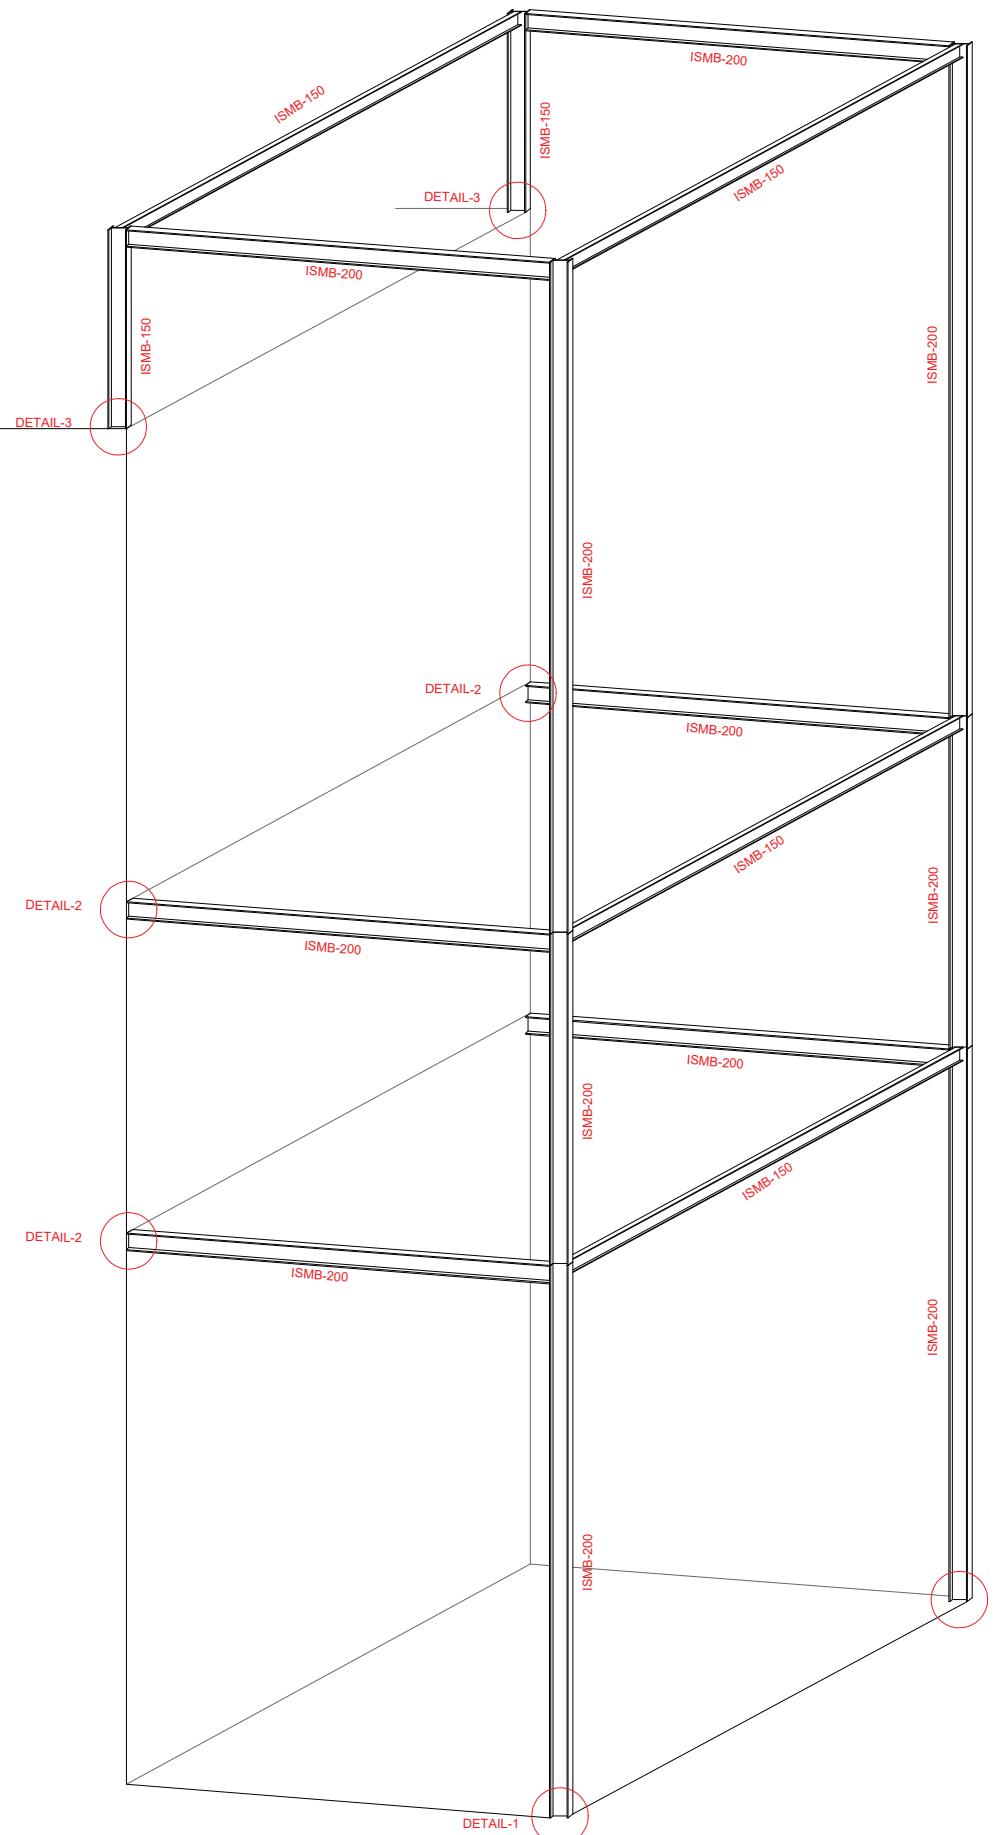


FRONT ELEVATION ISOMETRIC VIEW

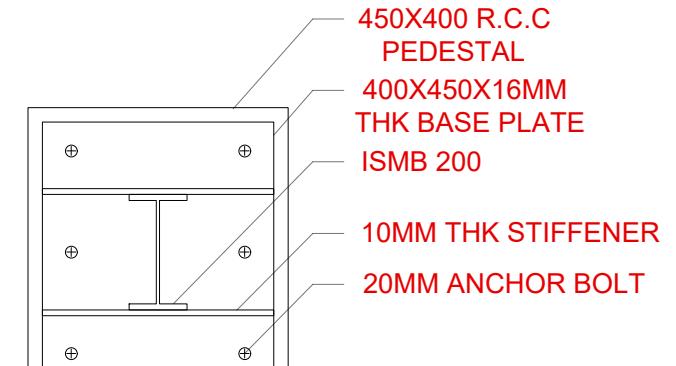


DETAIL-A

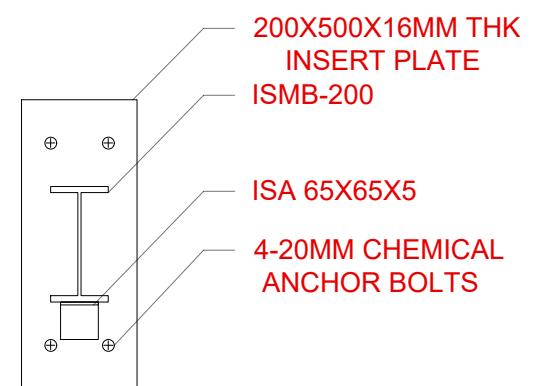


DETAIL-B

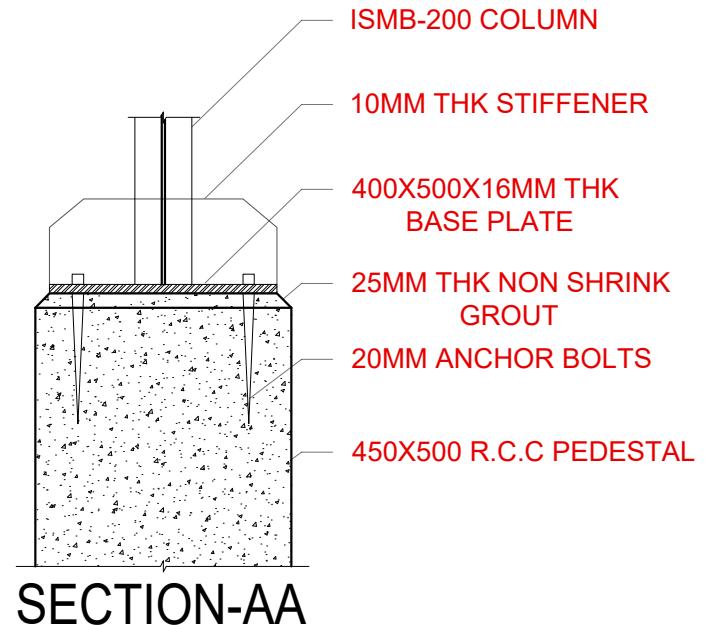


SECTION-AA

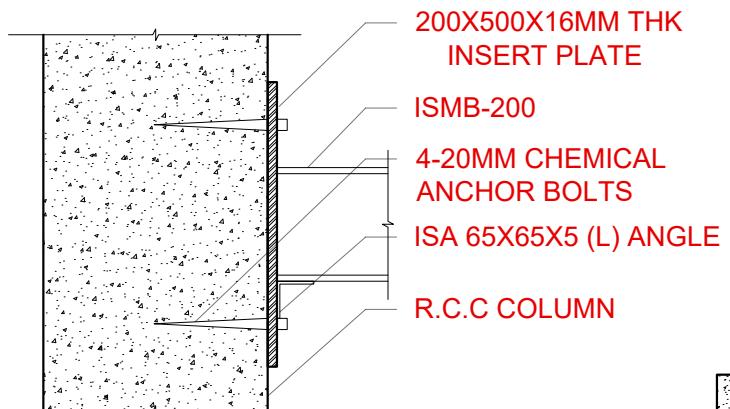


SECTION-BB

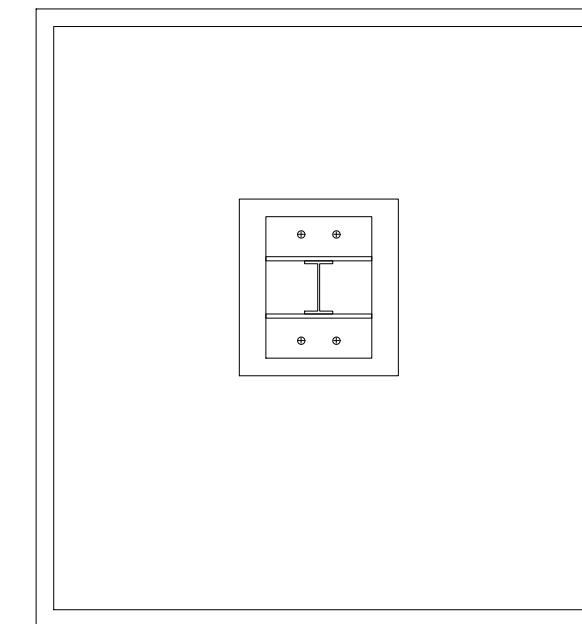

PEDESTAL PLAN

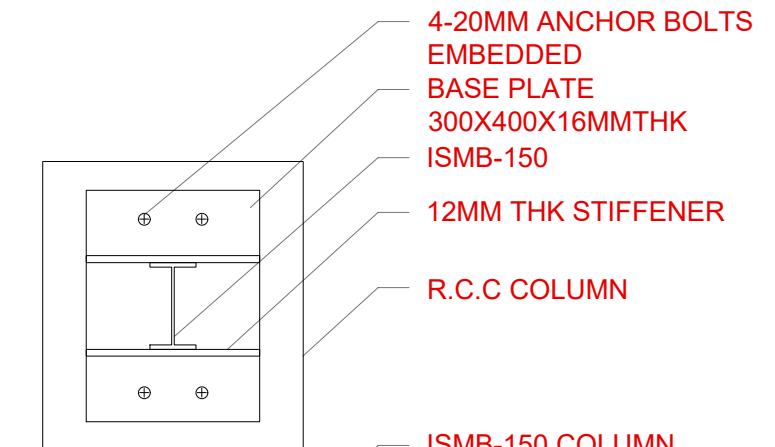

DETAIL-C

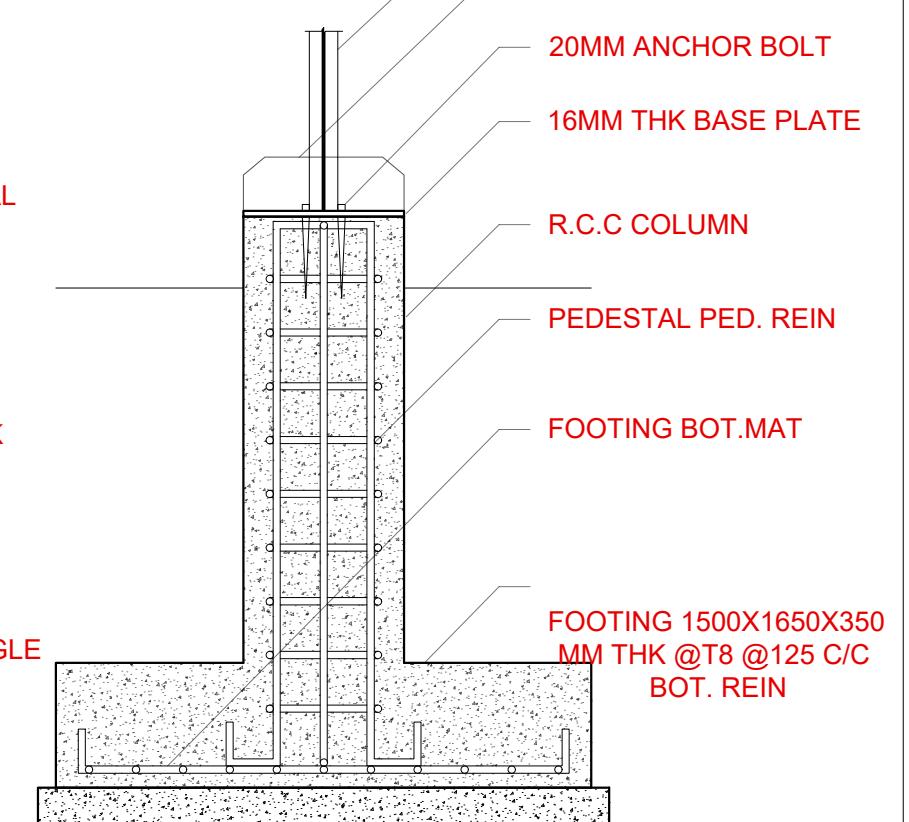

SECTION-CC

D. U. N. E

design unfiltered; a process never ending
54/2, 4th cross, Link road, Malleshwaram, Bangalore 560-003
designadune@gmail.com +91 23469351

PROJECT

PROPOSED RESIDENCE
FOR SATHYA & ABHILASH

DRAWING TITLE

WORKING DRAWING

DRAWING TITLE

DECK DETAILS

DATE 16 - 11 - 2022

SCALE NOT IN SCALE

PRINT ON A3

DRAWN BY JISHNU.K

CHECKED BY THEERTHAK



NOTE

DECK AREA = 341 SQFT

PROJECT CODE SAR@S

DRAWING NUMBER WD-002

REVISION NUMBER 0

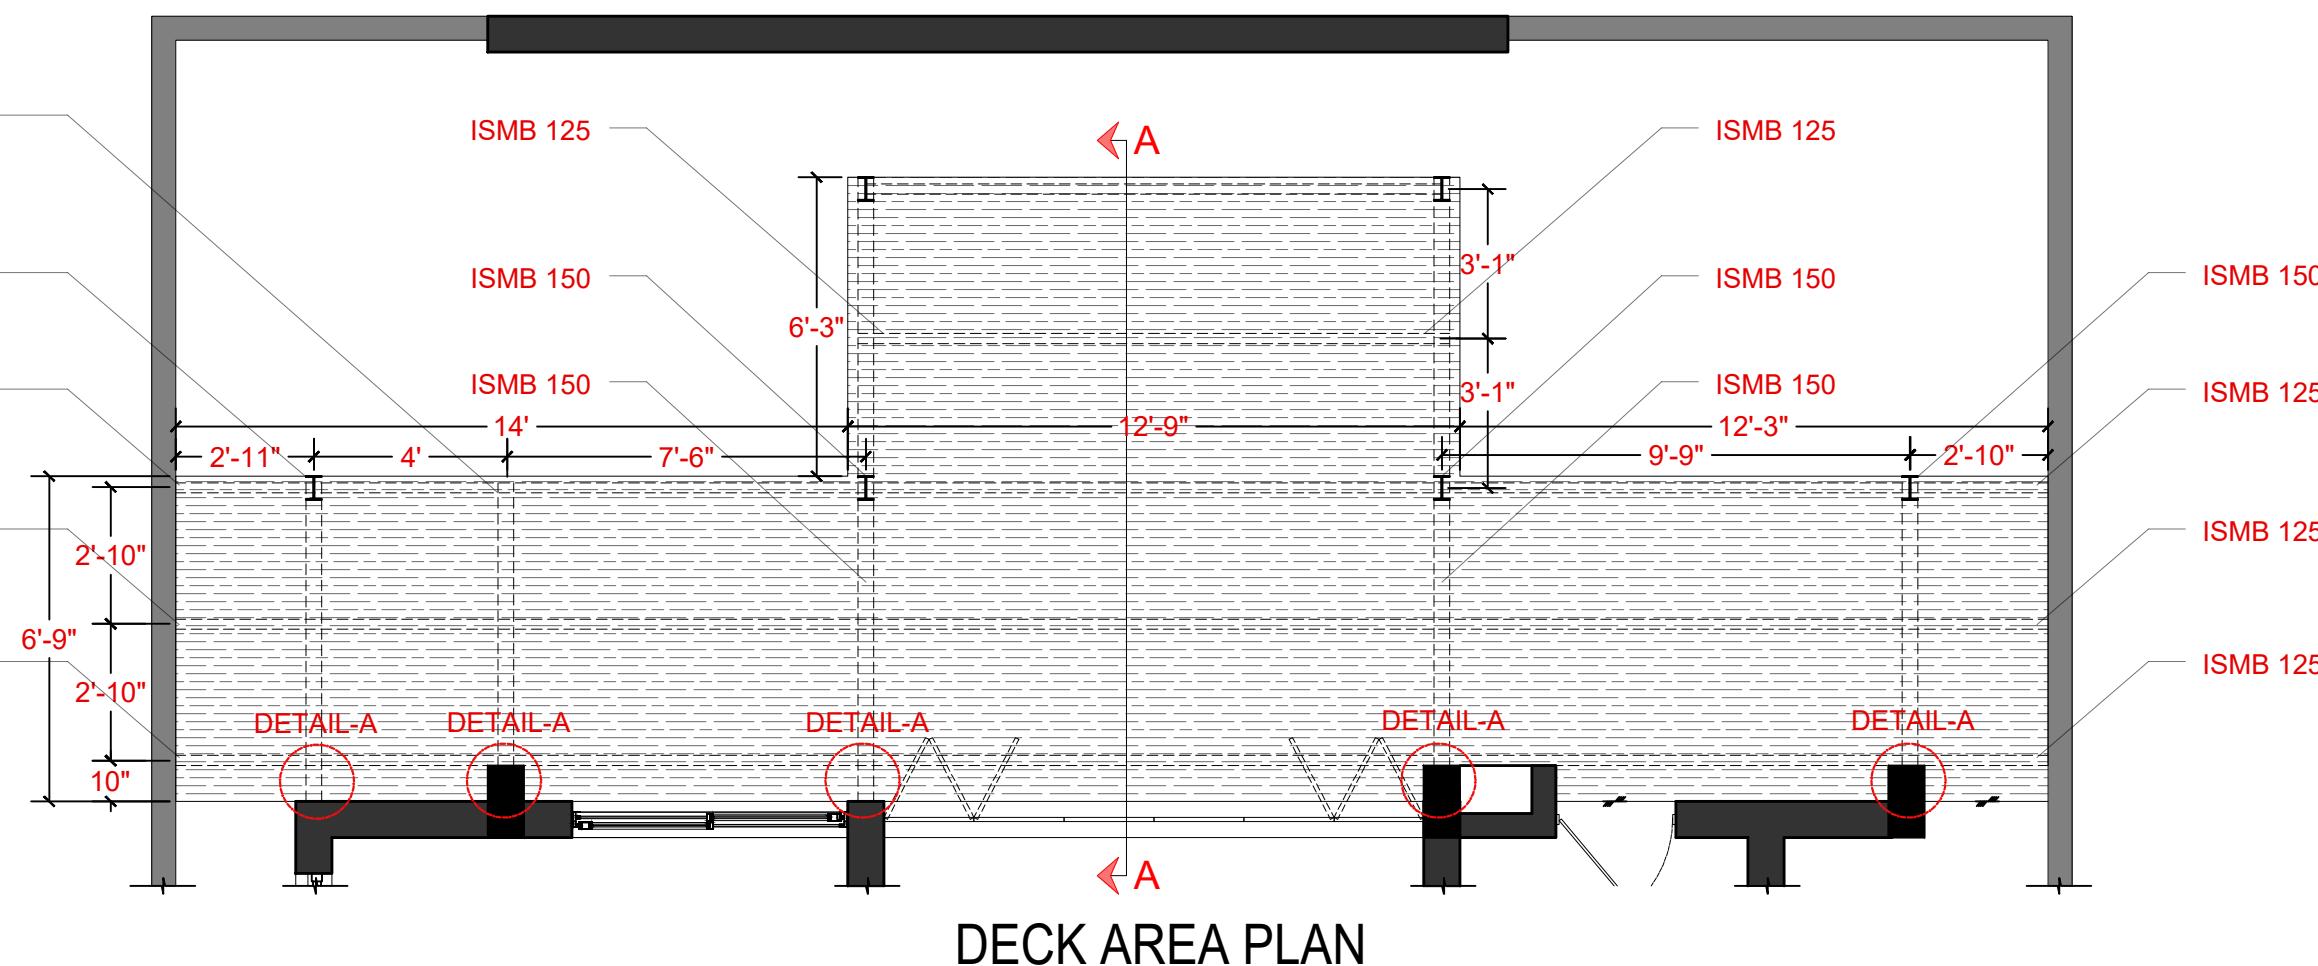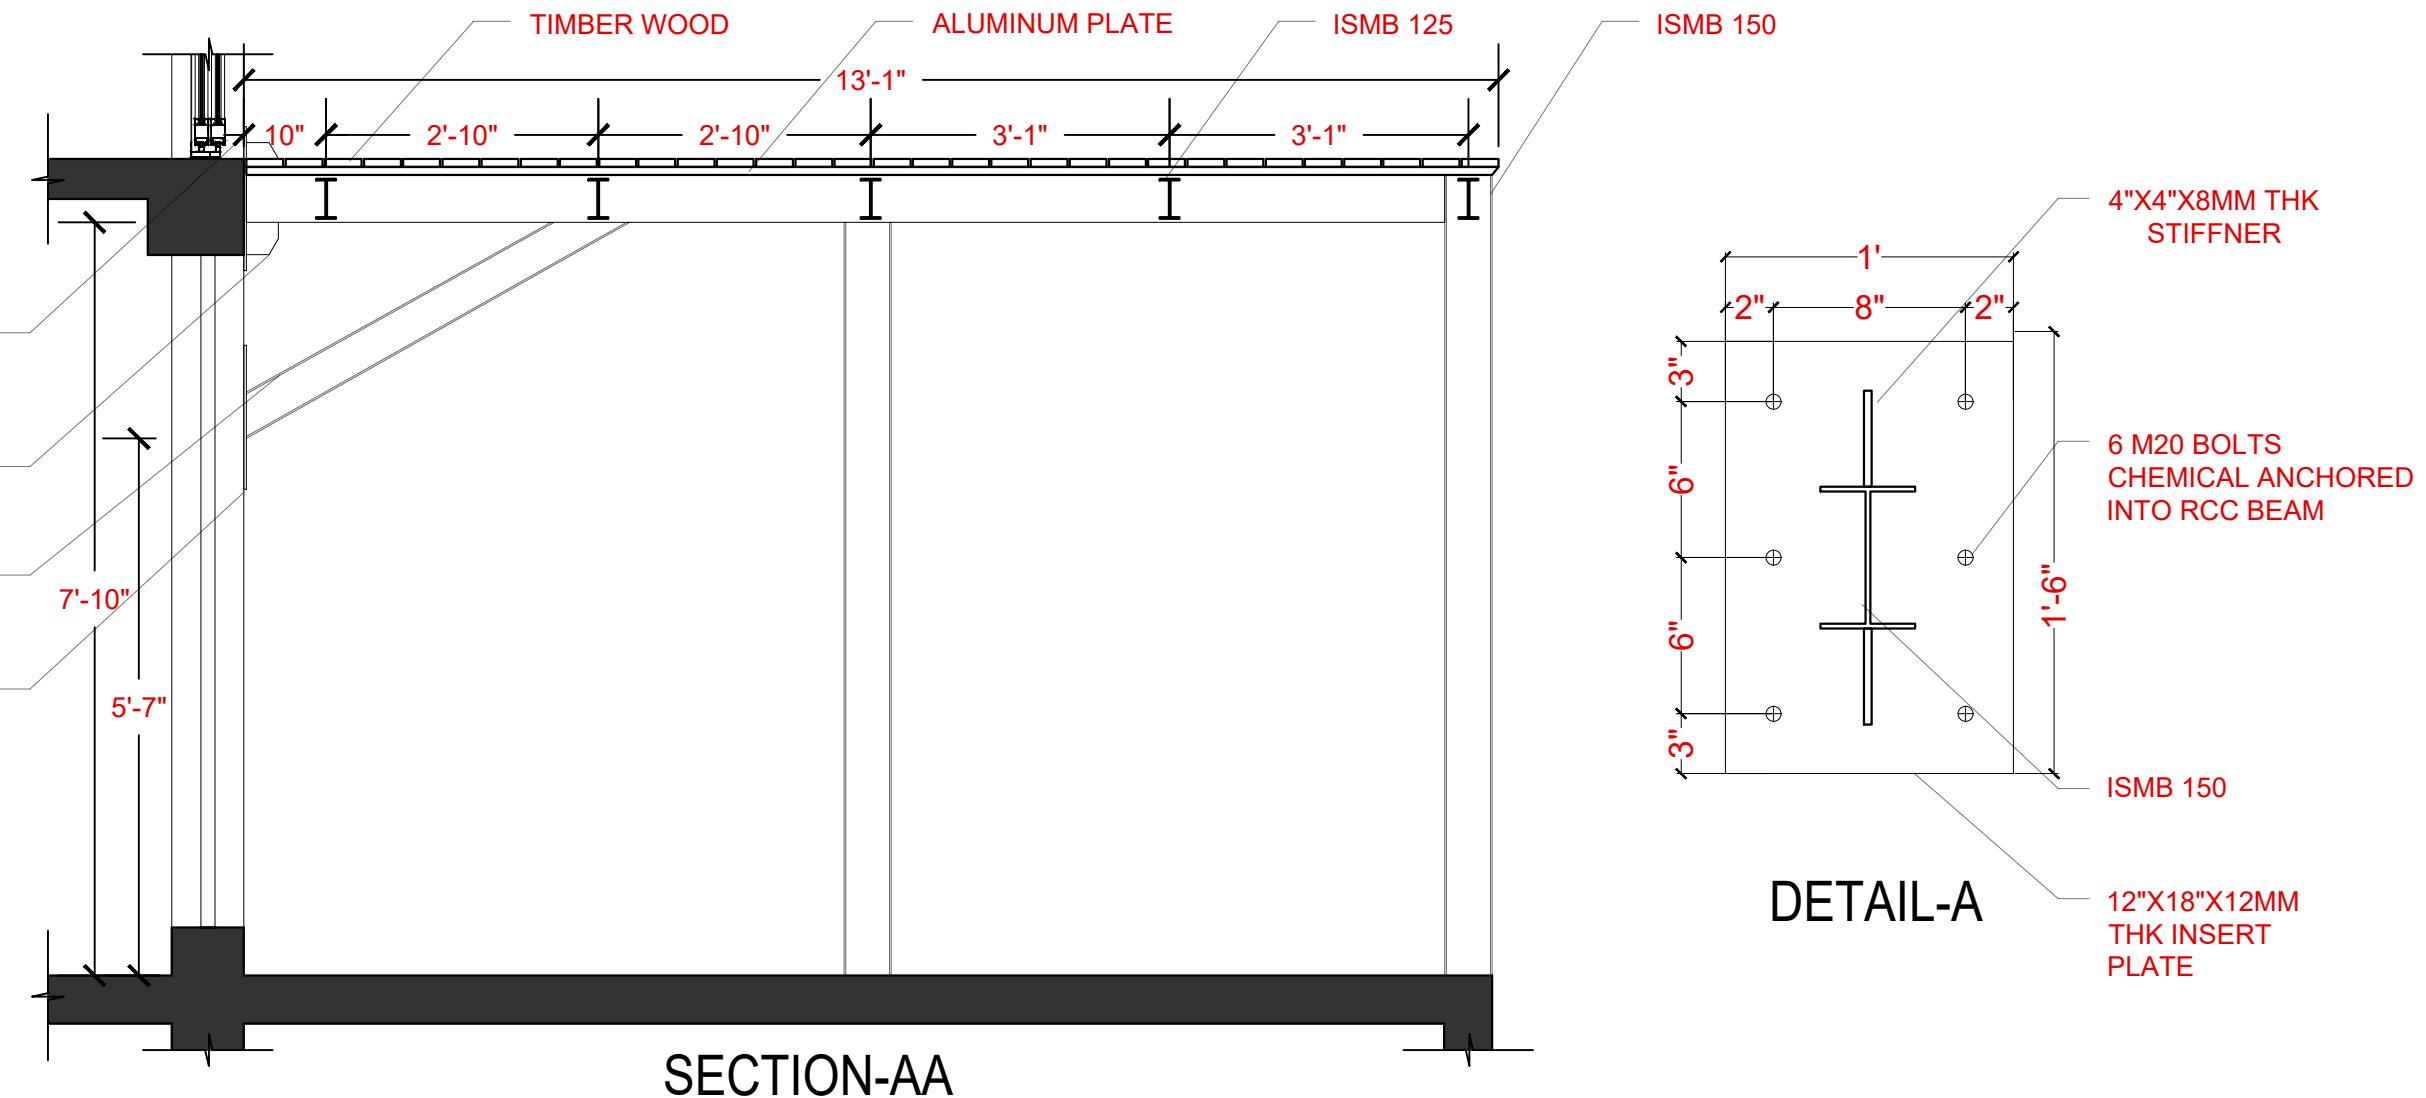

D. U. N. E

design unfiltered; a process never ending
54/2, 4th cross, Link road, Malleshwaram, Bangalore 560-003
designadune@gmail.com +91 23469351

PROJECT

PROPOSED RESIDENCE
FOR SATHYA & ABHILASH

DRAWING TITLE

WORKING DRAWING

DRAWING TITLE

SKYLIGHT &
GLASS AWNING DETAILS

DATE 16 - 11 - 2022

SCALE NOT IN SCALE

PRINT ON A3

DRAWN BY JISHNU.K






CHECKED BY THEERTHAK

NOTE

PROJECT CODE SAR@S

DRAWING NUMBER WD-002

REVISION NUMBER 0

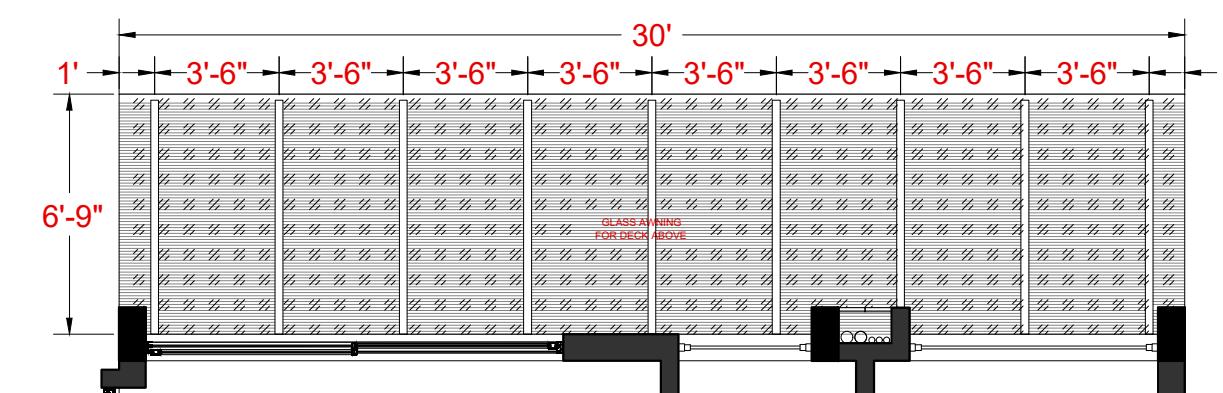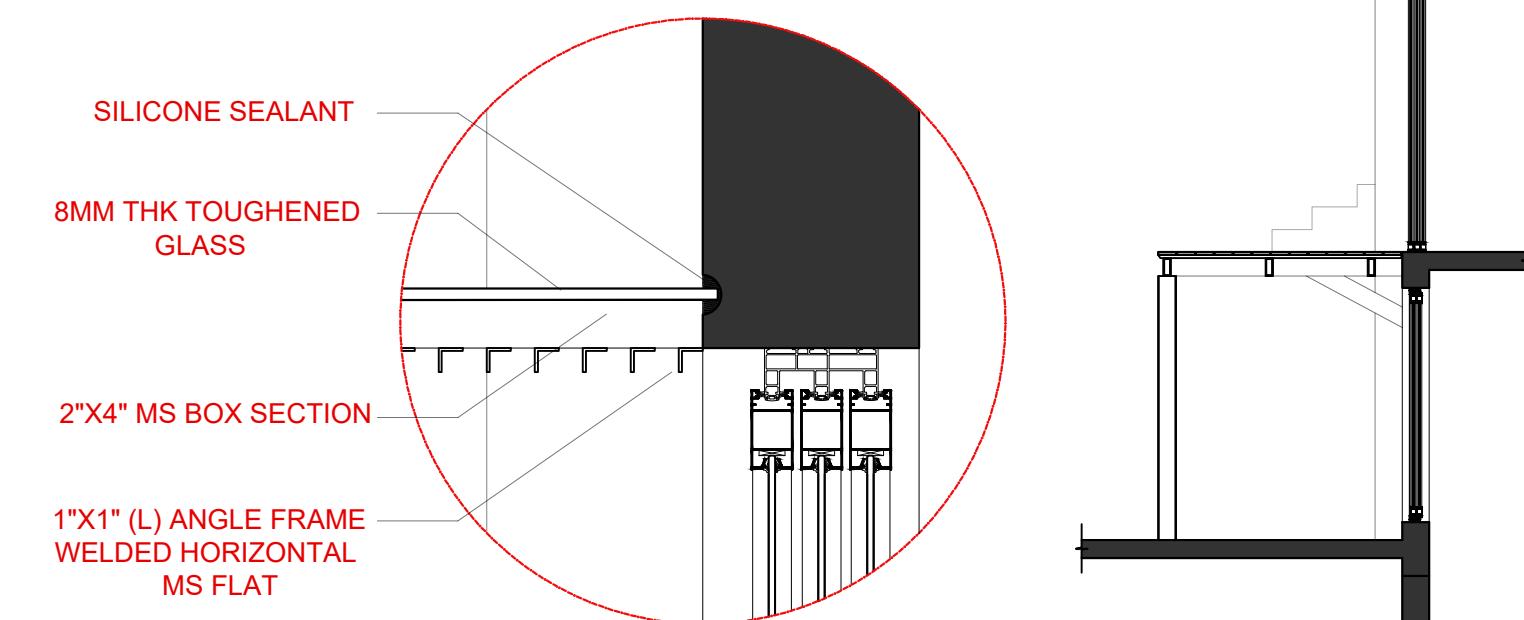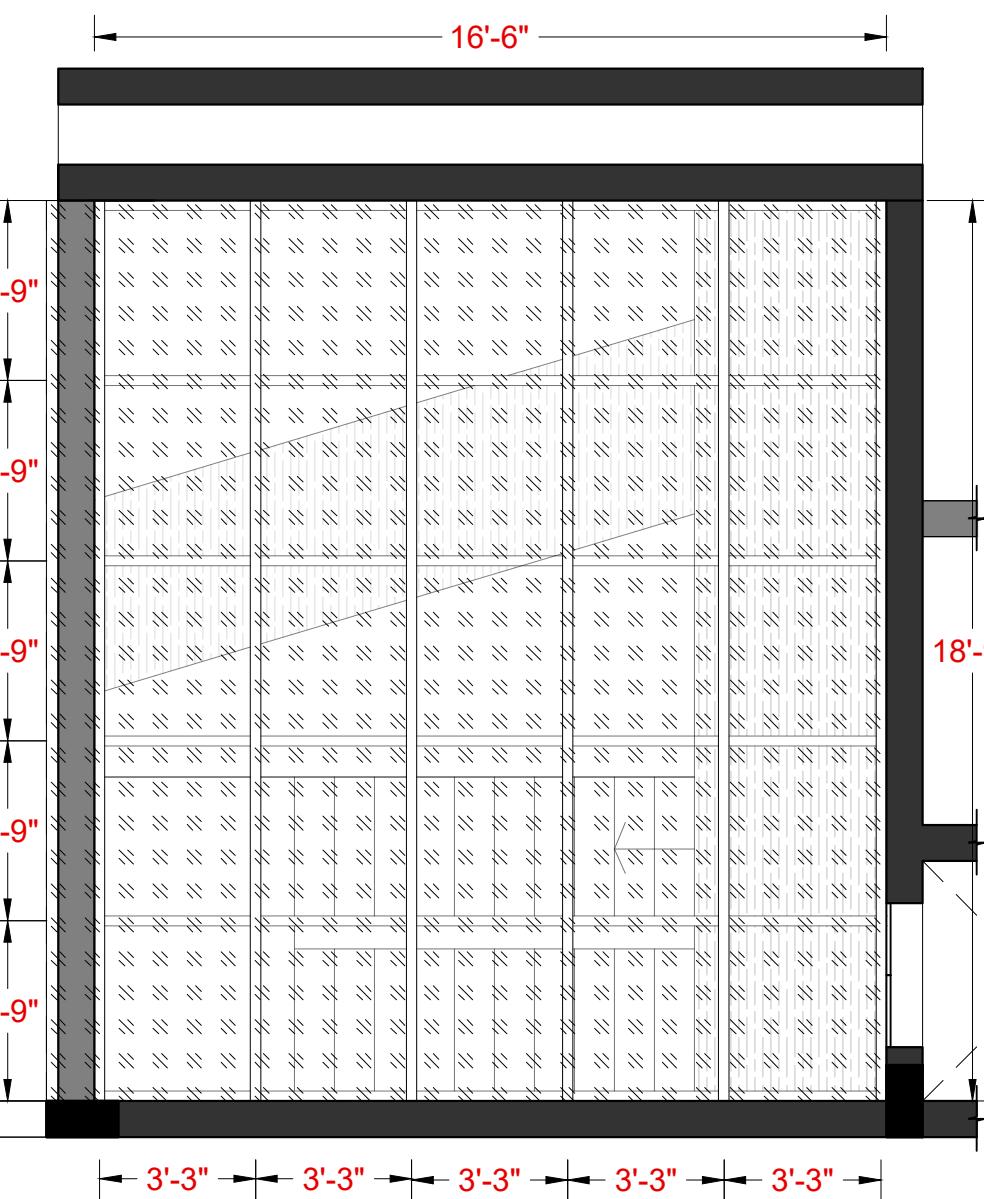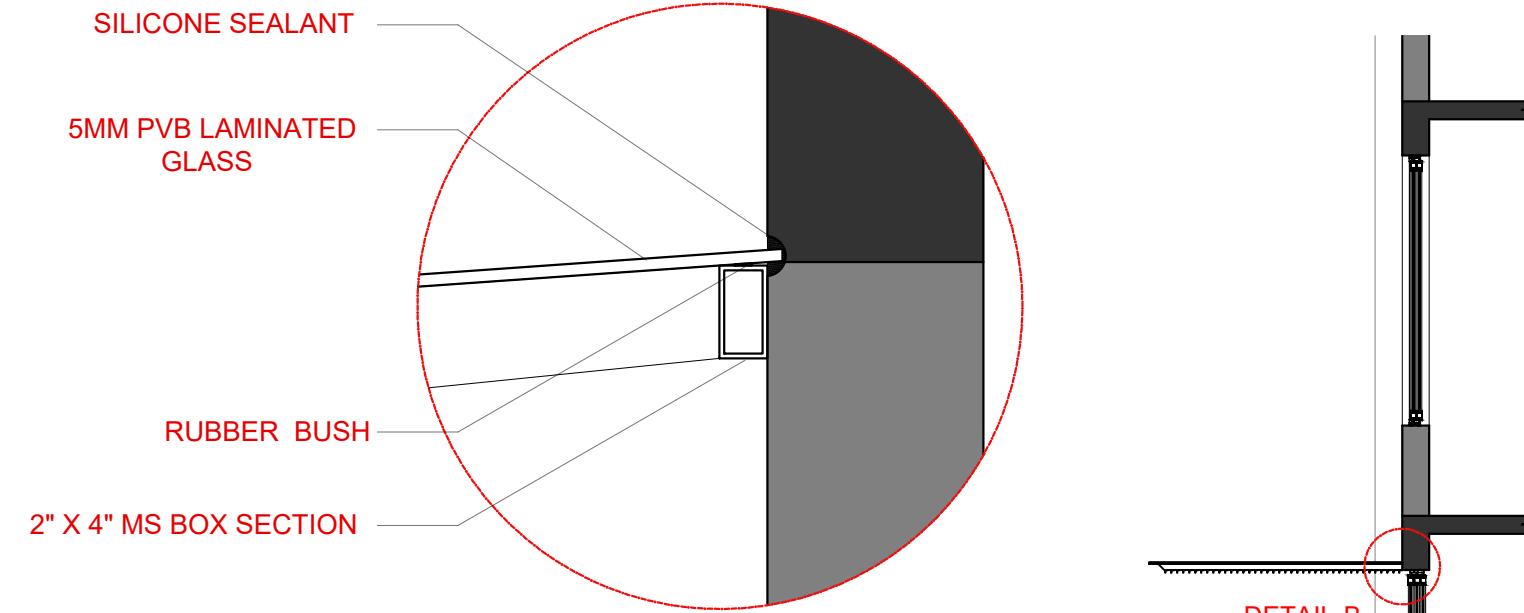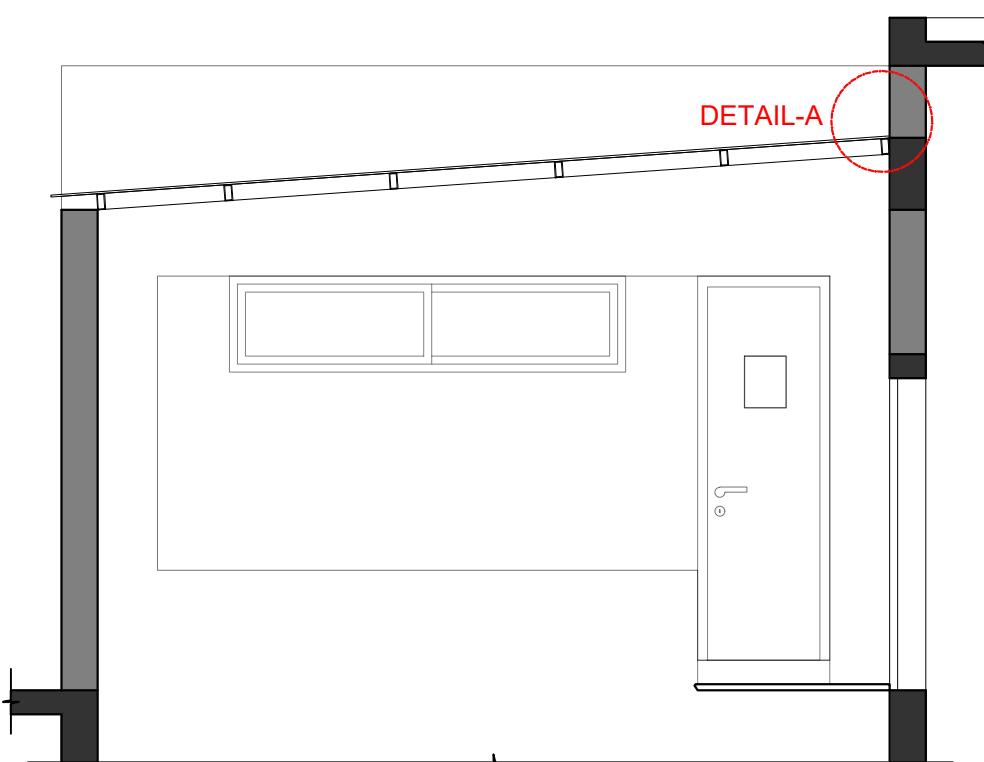

TERRACE PLAN

AWNING PLAN

D. U. N. E

design unfiltered; a process never ending
54/2, 4th cross, Link road, Malleshwaram, Bangalore 560-003
designadune@gmail.com +91 23469351

PROJECT

PROPOSED RESIDENCE
FOR SUHAS & PRIYA

DRAWING TITLE

WORKING DRAWING

DRAWING TITLE

SKYLIGHT DETAILS

DATE 06 - 01 - 2023

SCALE NOT IN SCALE

PRINT ON A3

DRAWN BY JISHNU.K

CHECKED BY THEERTHAK

NOTE

PROJECT CODE






SPAR

DRAWING NUMBER


WD-003

REVISION NUMBER


0

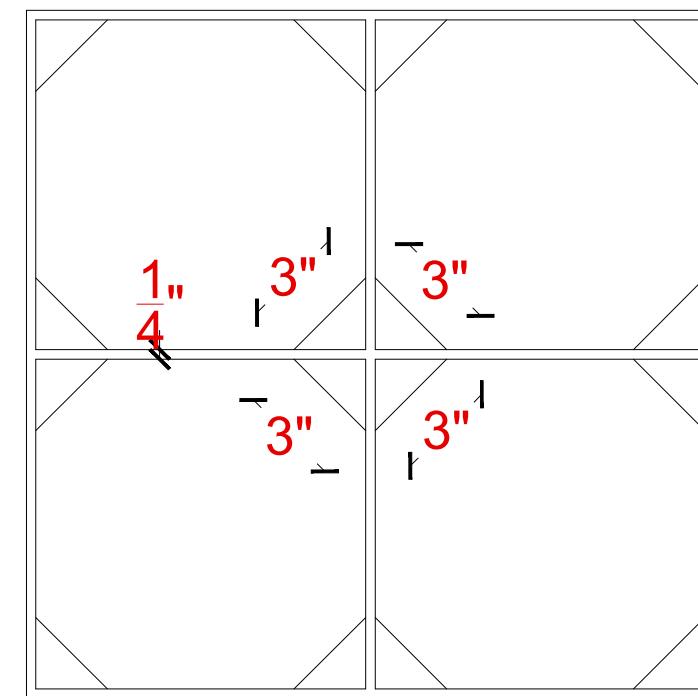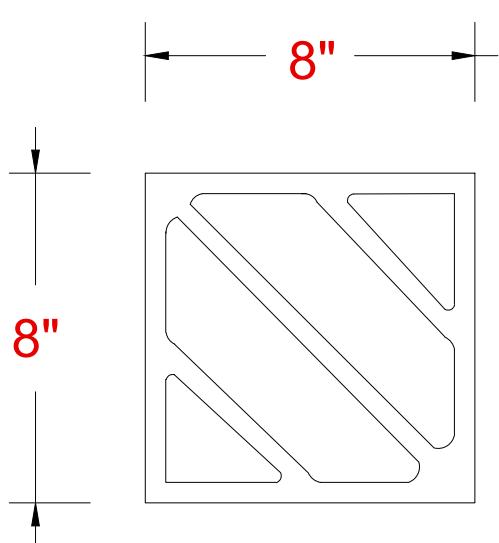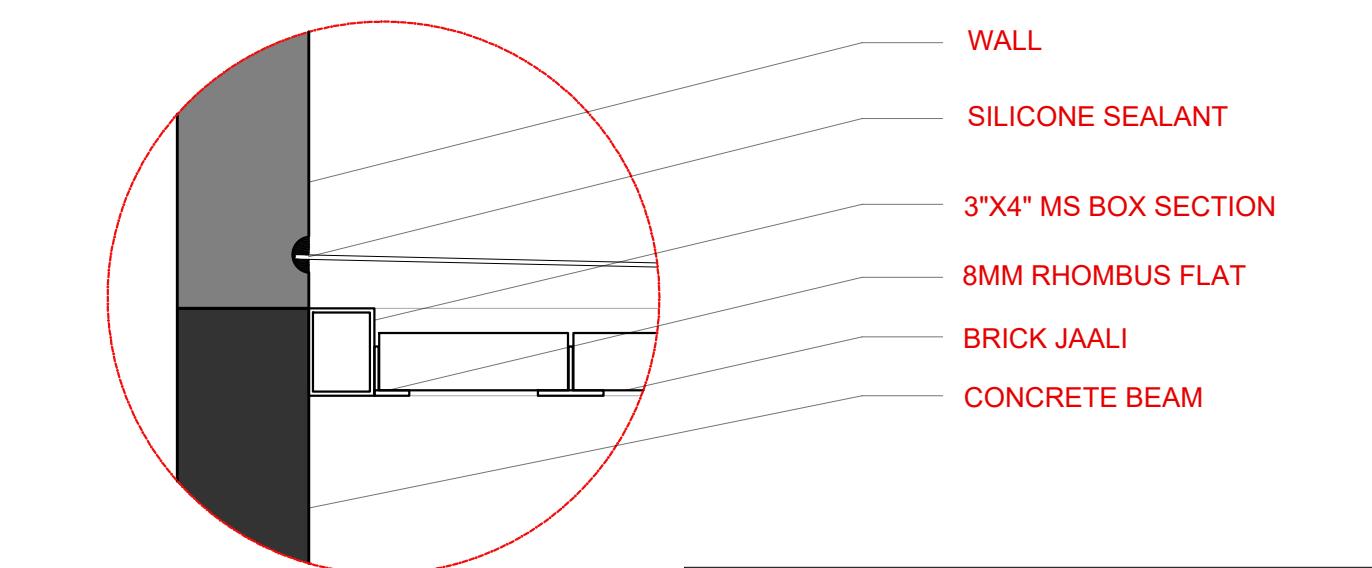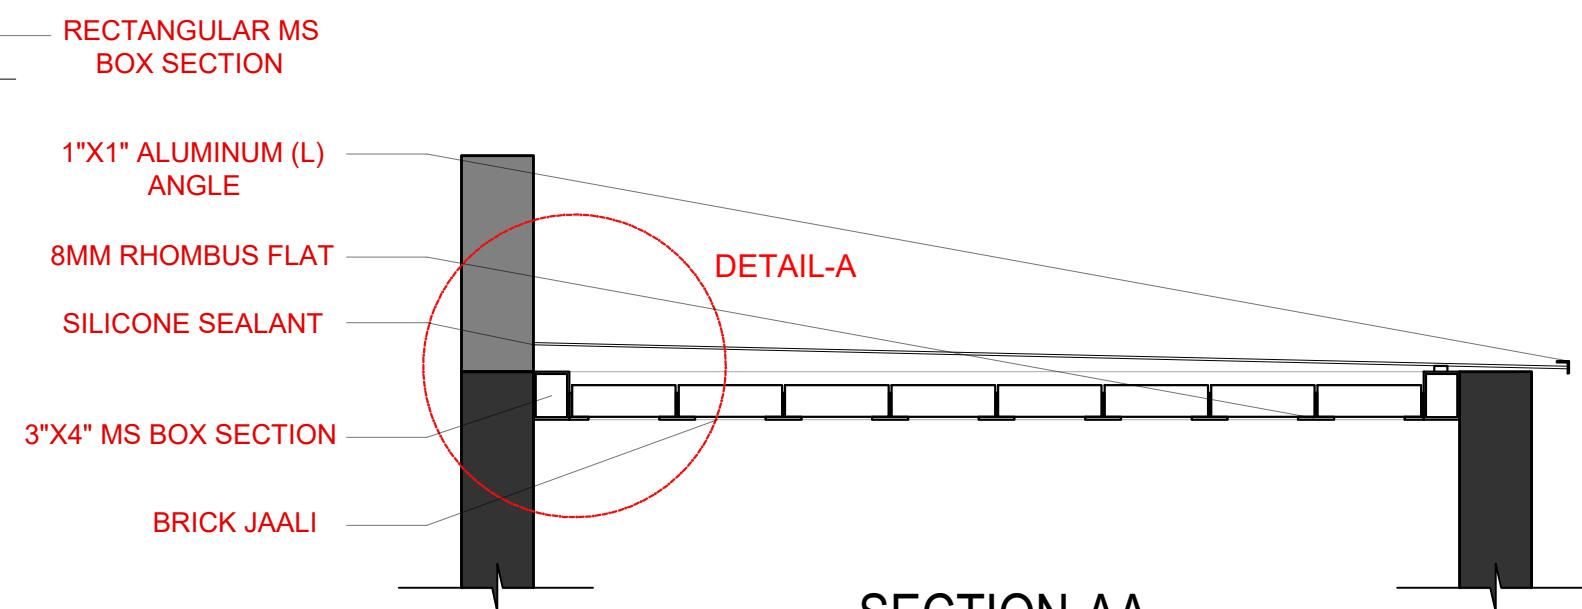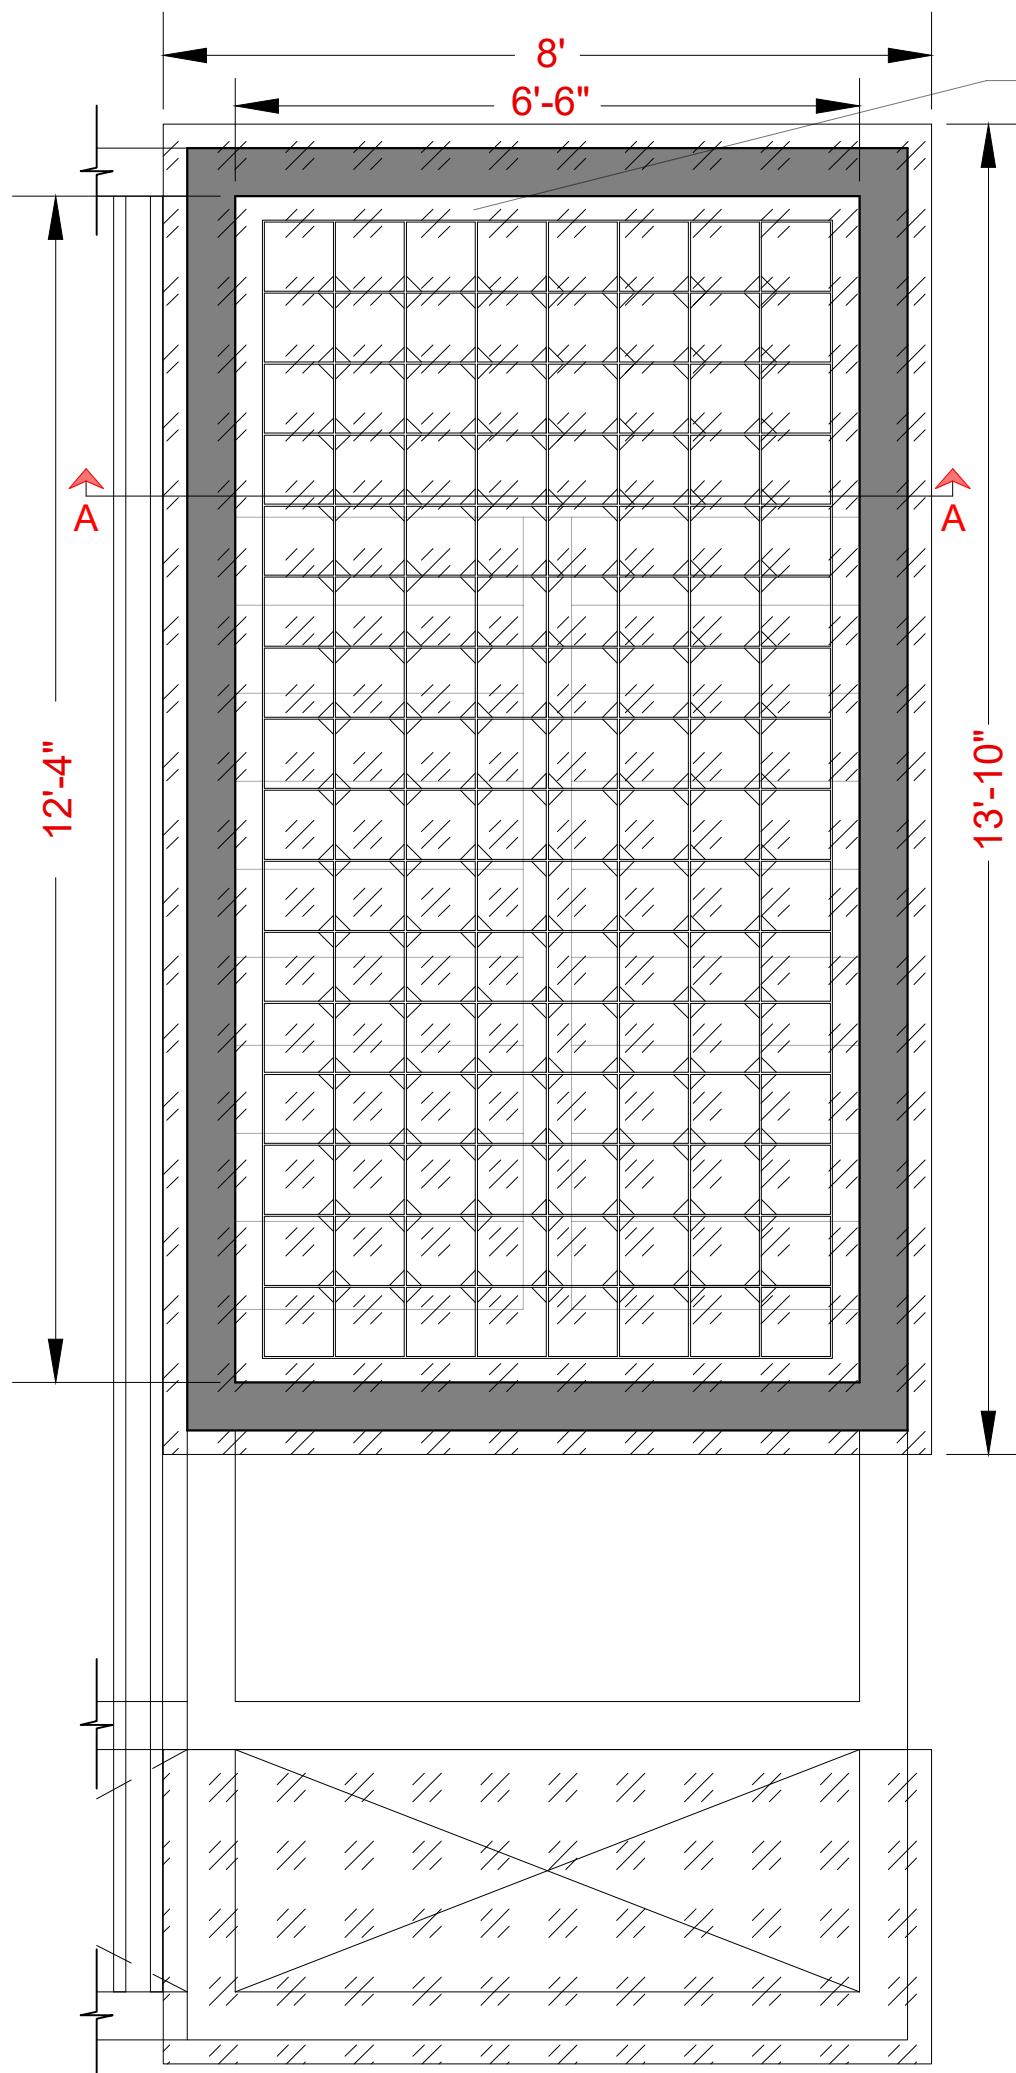


ISOMETRIC VIEWS

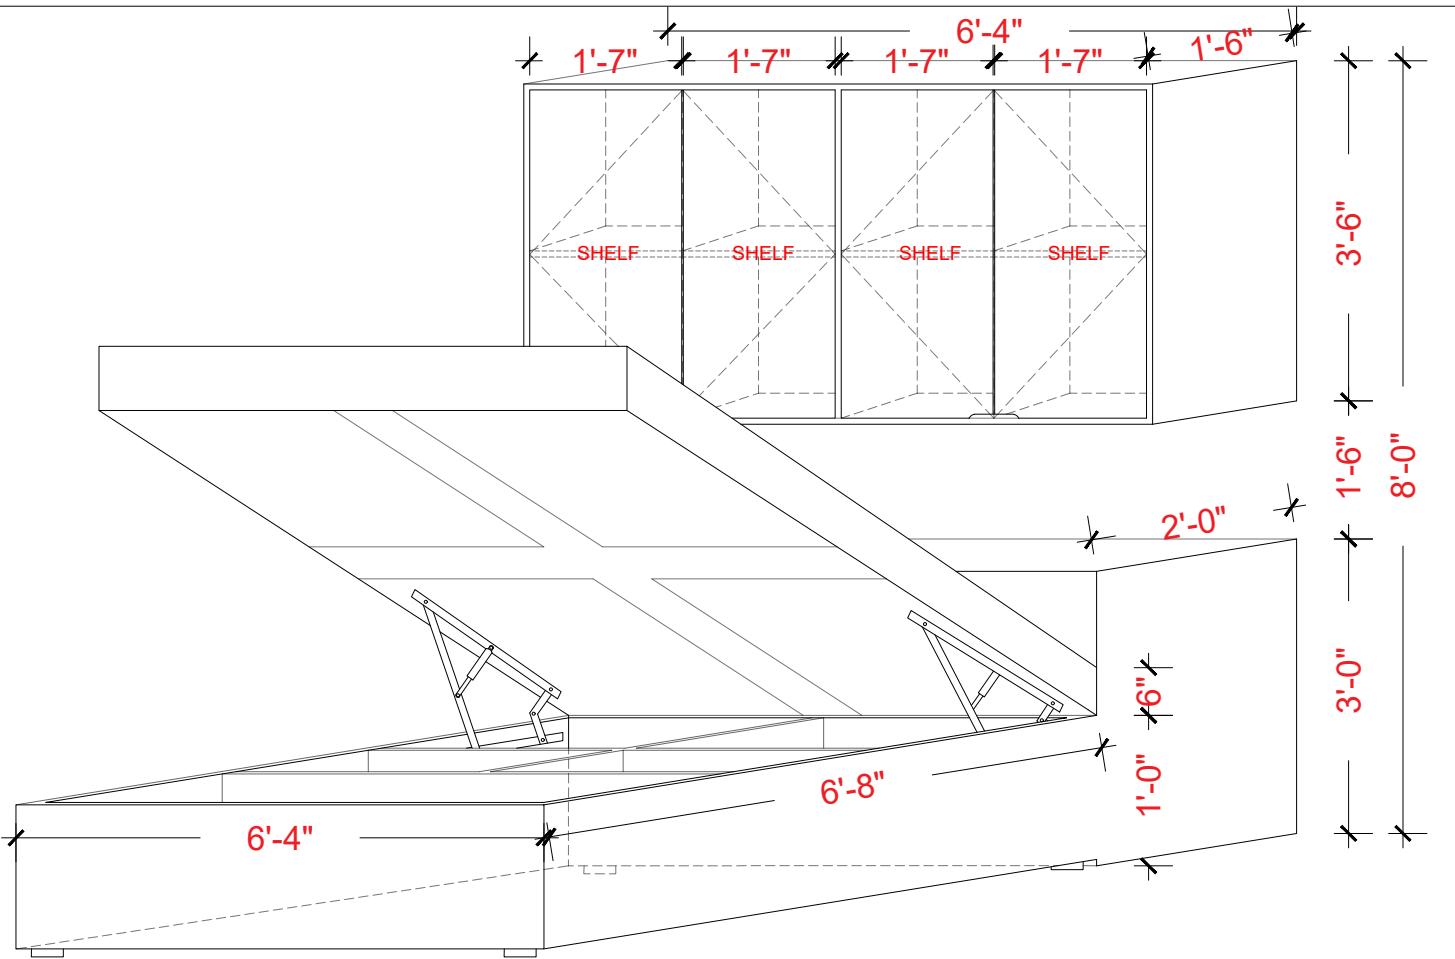


HYDRAULIC BED ELEVATION

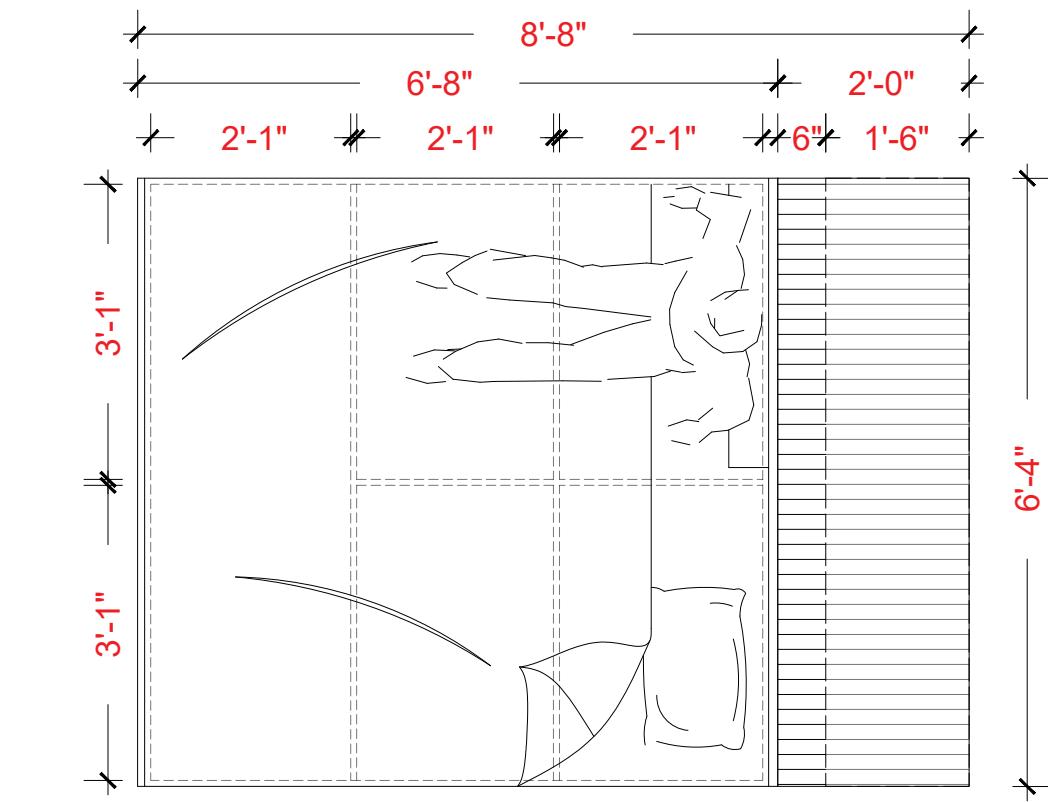


HYDRAULIC BED PLAN

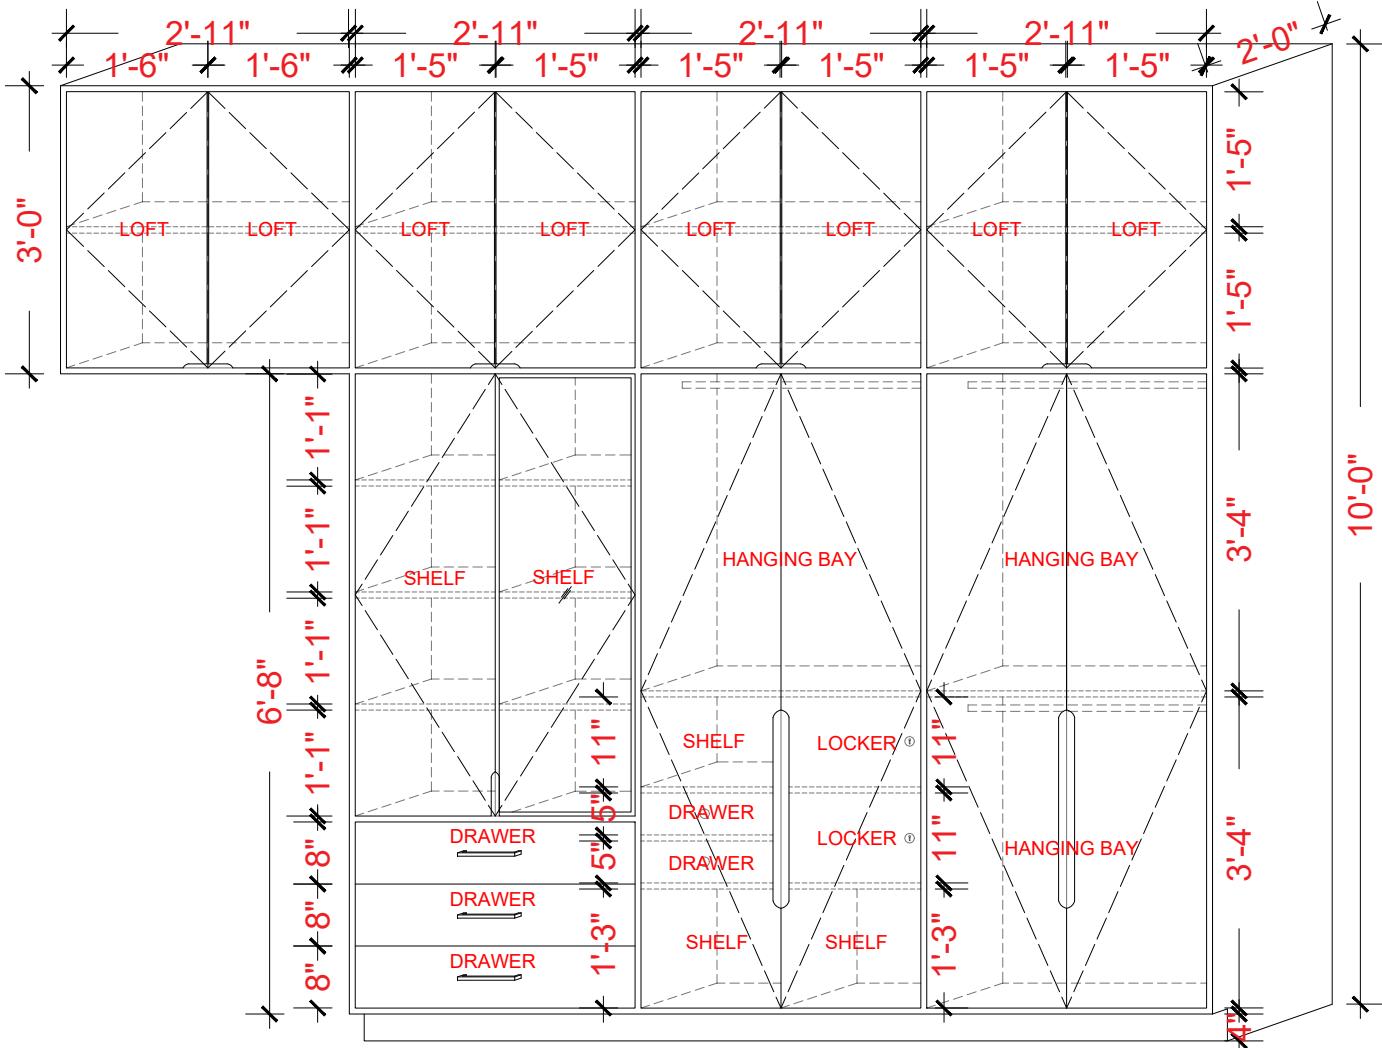


CUPBOARD ELEVATION

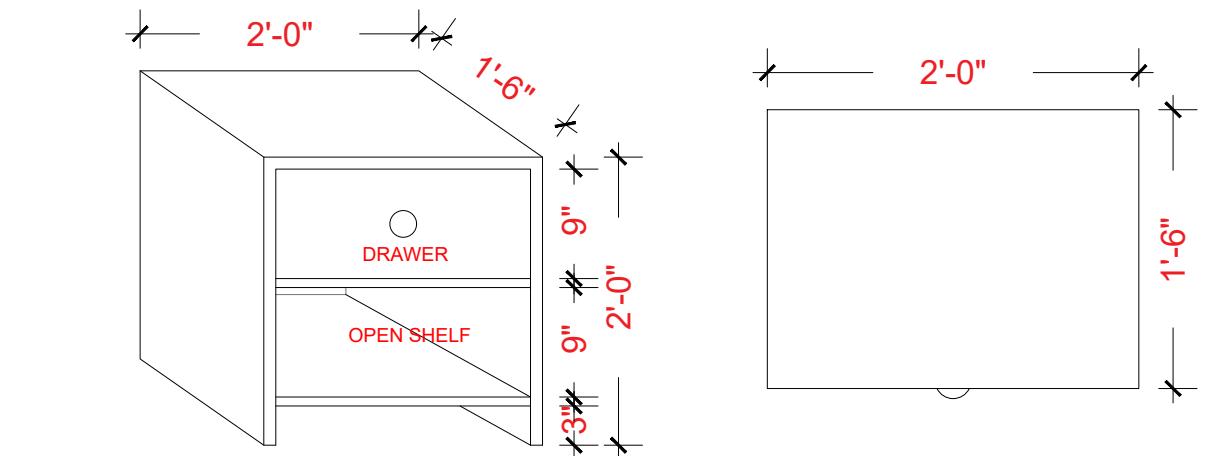

BED SIDE TABLE

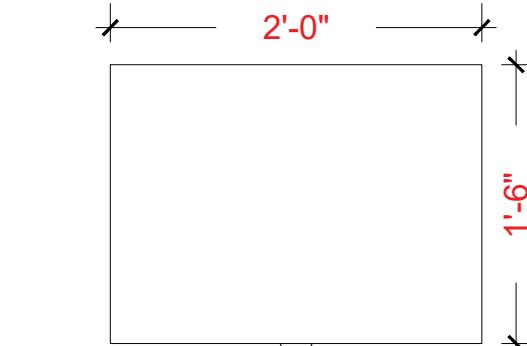

BED SIDE TABLE PLAN

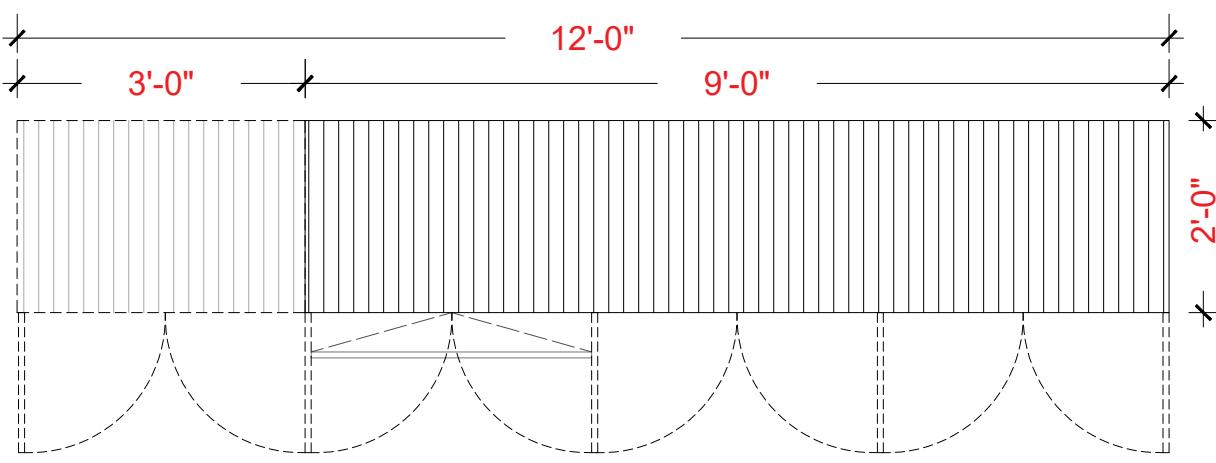

CUPBOARD PLAN

D. U. N. E

design unfiltered; a process never ending
54/2, 4th cross, Link road, Malleshwaram, Bangalore 560-003
designadune@gmail.com +91 23469351

PROJE

PROPOSED RESIDENCE FOR RAHUL & ROHITH

DRAWING TITLE

WORKING DRAWING

DRAWING TITLE

FURNITURE DRAWINGS

DATE 16 - 11 - 2022

SCALE NOT IN SCALE

PRINT ON

DRAWN BY JISHNU.K

CHECKED BY THEERTHAK

NOTE

PROJECT CODE

RRR

DRAWING NUMBER

REVISION NUMBER

0

N

D. U. N. E

design unfiltered; a process never ending
54/2, 4th cross, Link road, Malleshwaram, Bangalore 560-003
designadune@gmail.com +91 23469351

PROJECT

PROPOSED RESIDENCE
FOR RAHUL & ROHITH

DRAWING TITLE

WORKING DRAWING

DRAWING TITLE

FURNITURE DRAWINGS

DATE 16 - 11 - 2022

SCALE NOT IN SCALE

PRINT ON A3

DRAWN BY JISHNU.K

CHECKED BY THEERTHAK

NOTE

PROJECT CODE




RRR

DRAWING NUMBER

WD-002

REVISION NUMBER

0

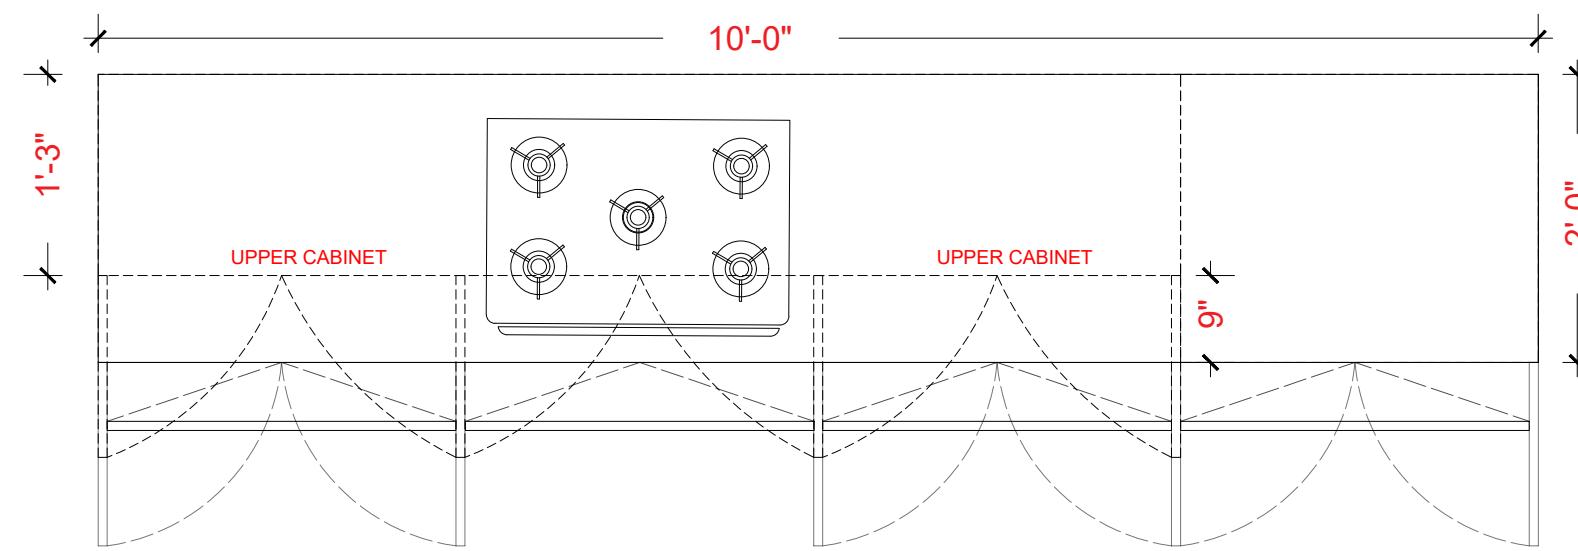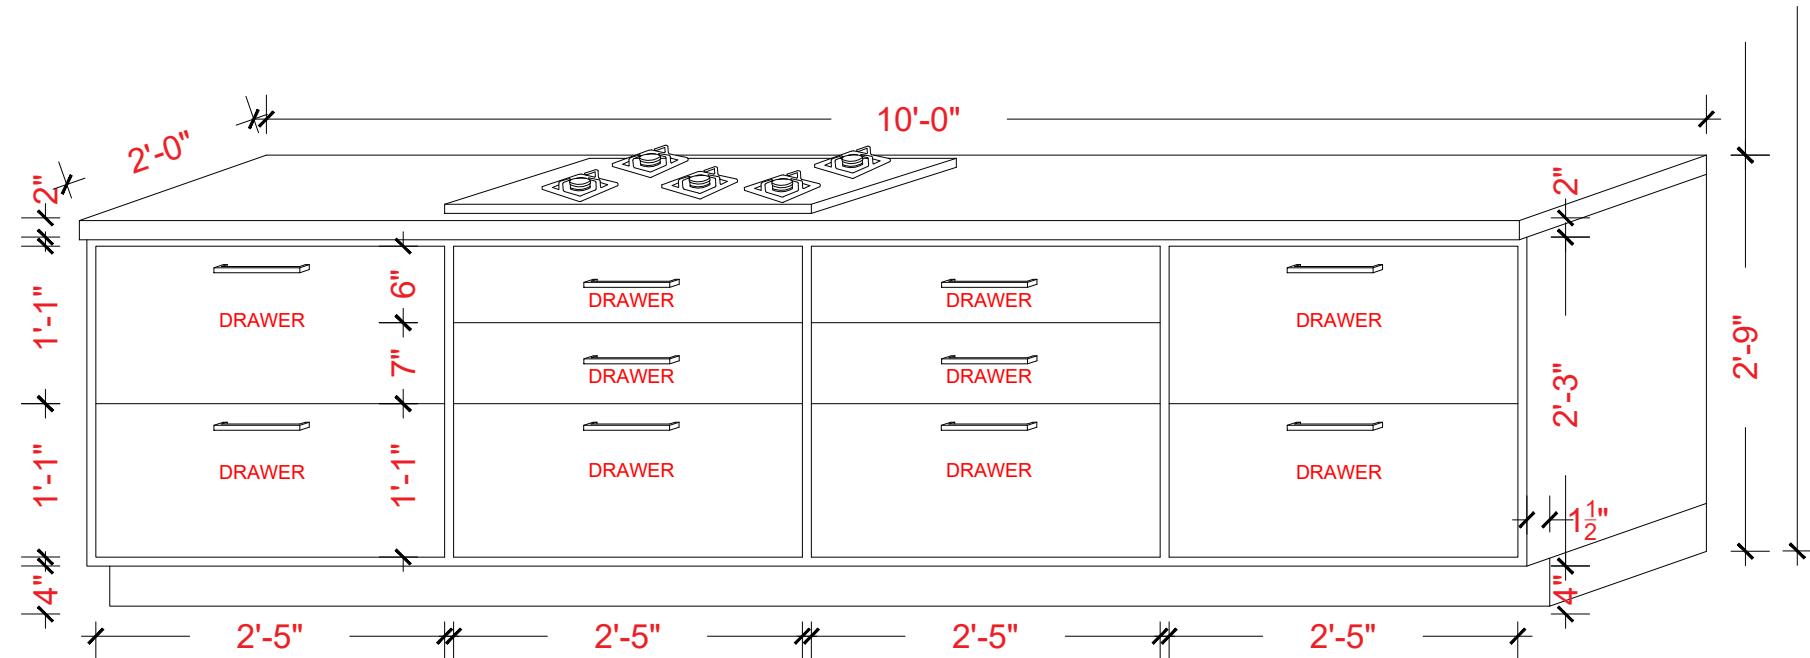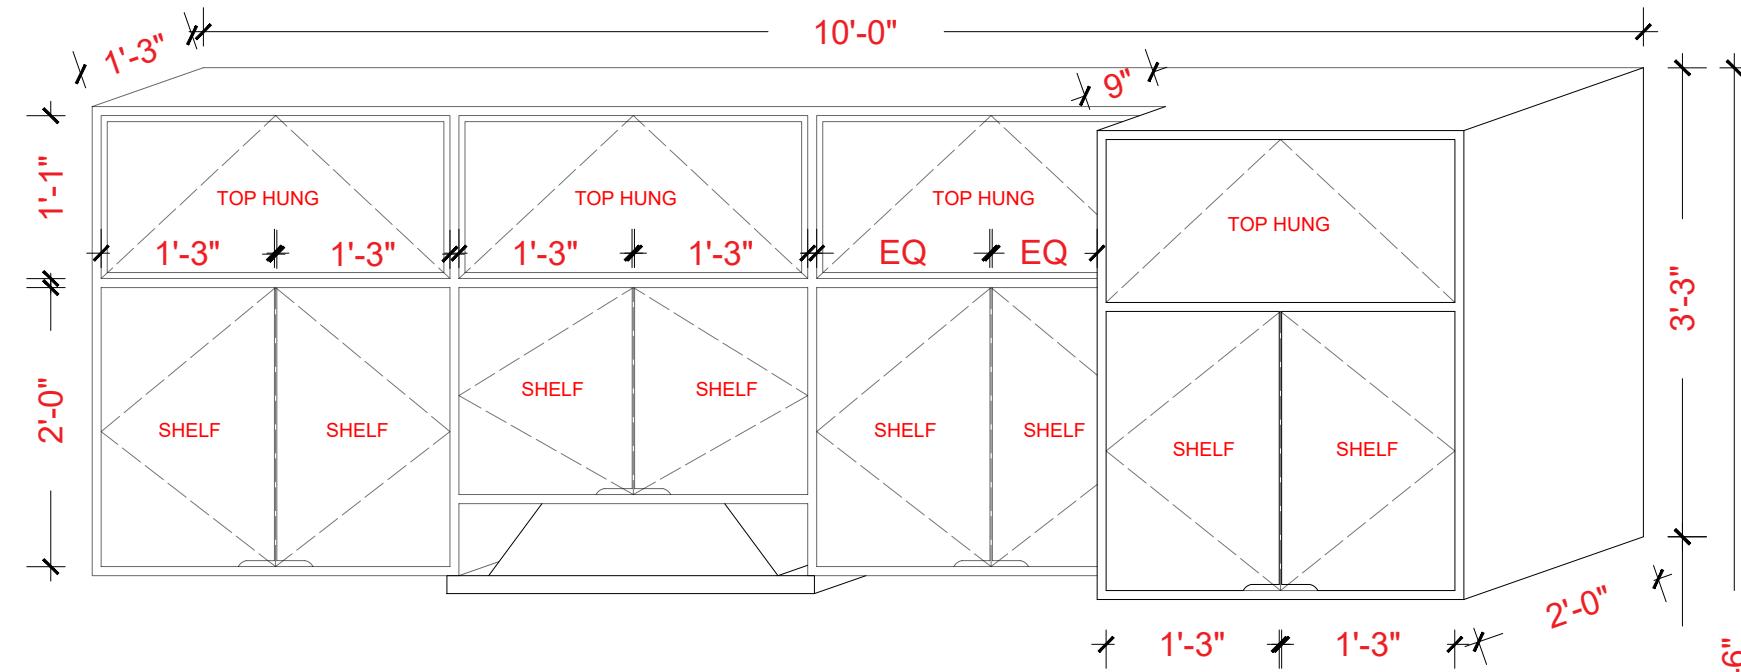

D. U. N. E

design unfiltered; a process never ending
54/2, 4th cross, Link road, Malleshwaram, Bangalore 560-003
designadune@gmail.com +91 23469351

PROJECT

PROPOSED RESIDENCE
FOR RAHUL & ROHITH

DRAWING TITLE

WORKING DRAWING

DRAWING TITLE

FURNITURE DRAWINGS

DATE 16 - 11 - 2022

SCALE NOT IN SCALE

PRINT ON A3

DRAWN BY JISHNU.K


CHECKED BY THEERTHAK

NOTE


PROJECT CODE RRR

DRAWING NUMBER WD-002


REVISION NUMBER 0

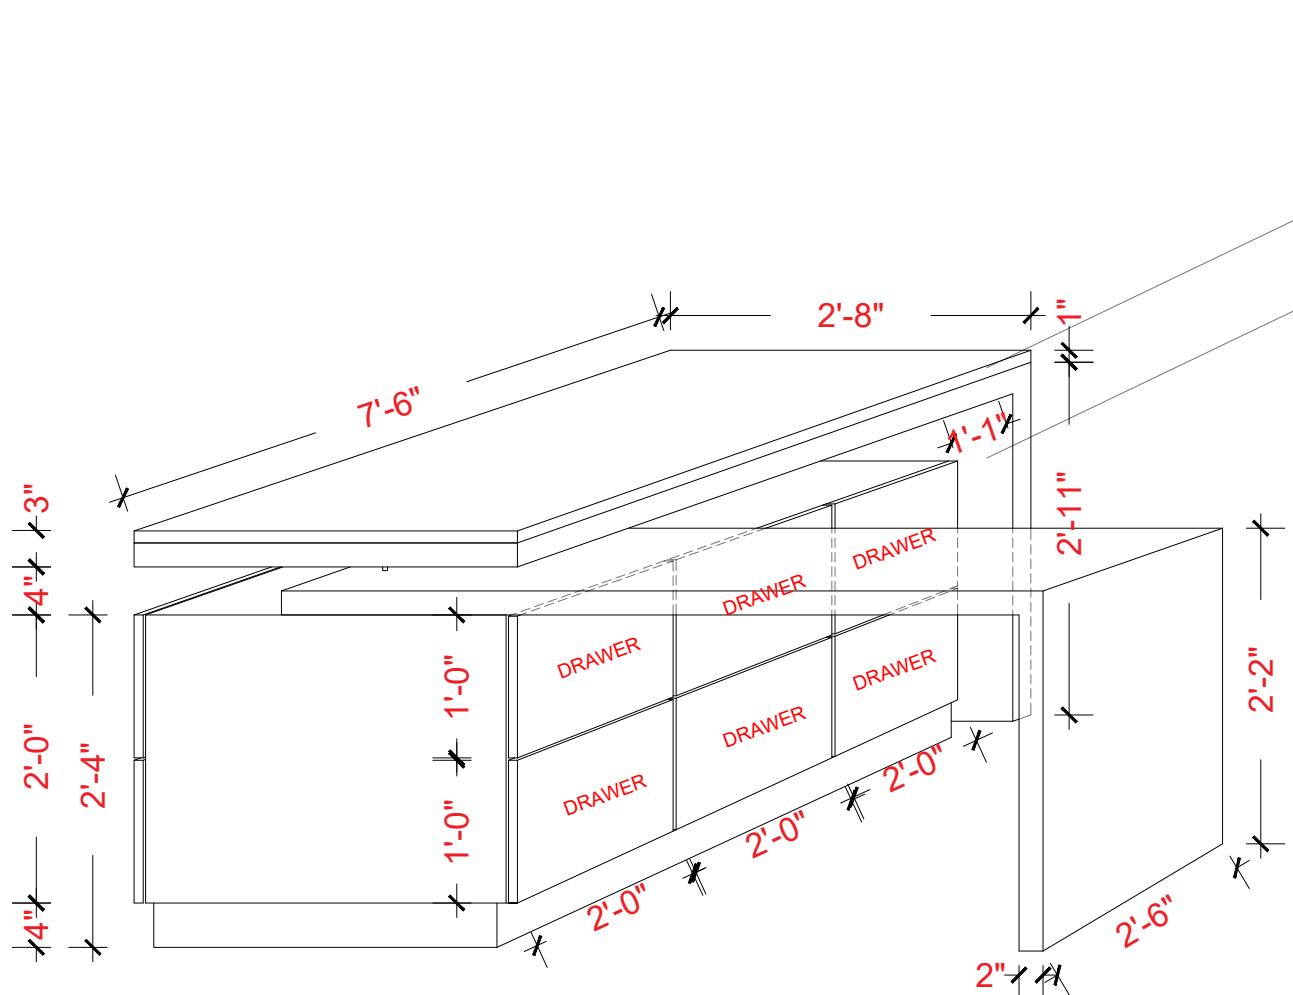


DINING TABLE ISOMETRIC VIEW

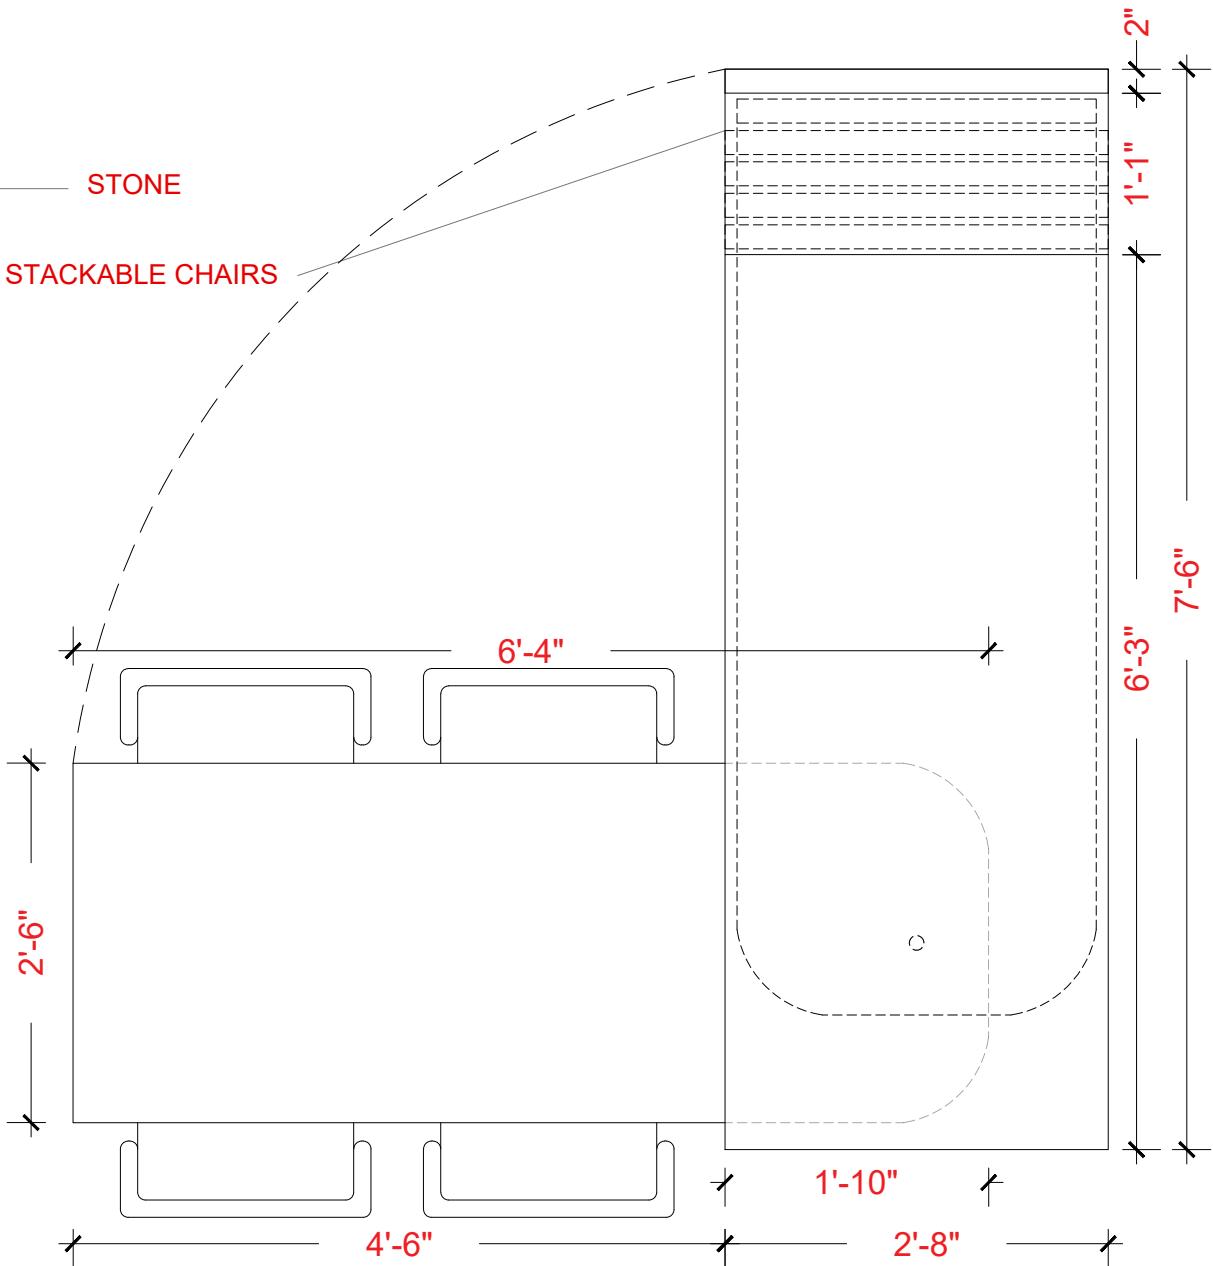

DINING TABLE PLAN

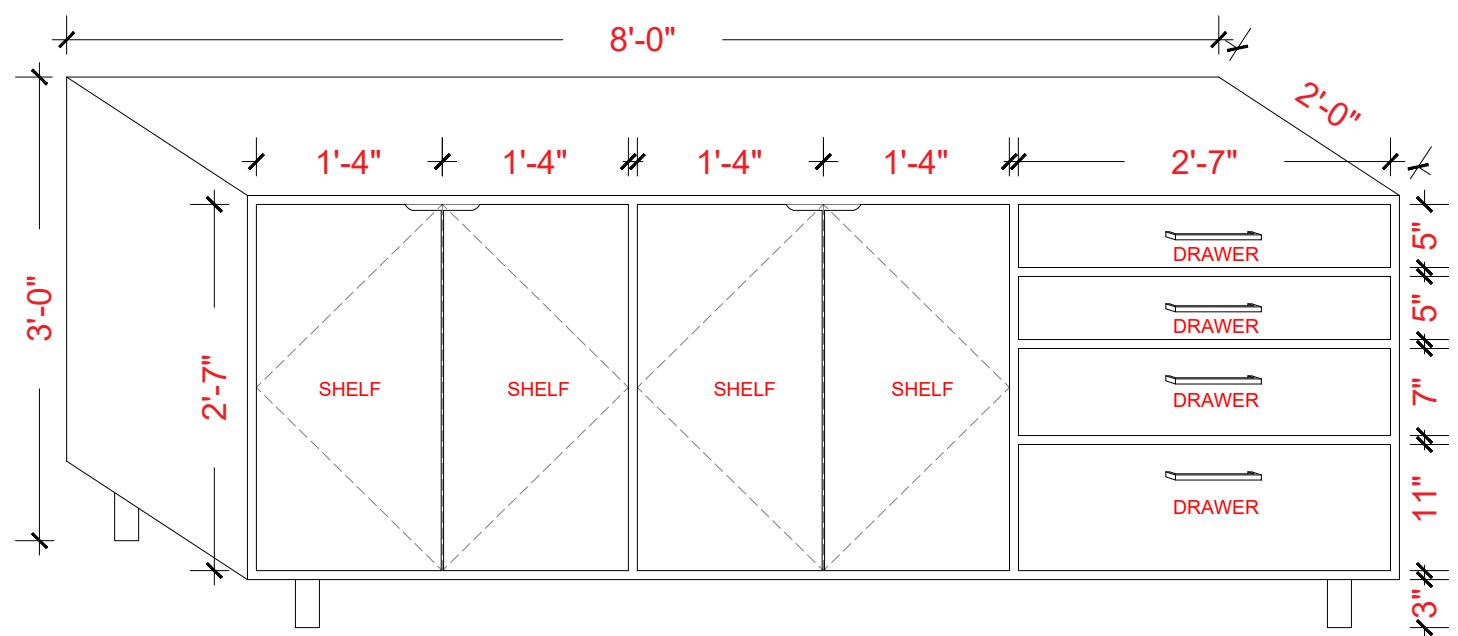

CONSOLE TABLE ISOMETRIC VIEW

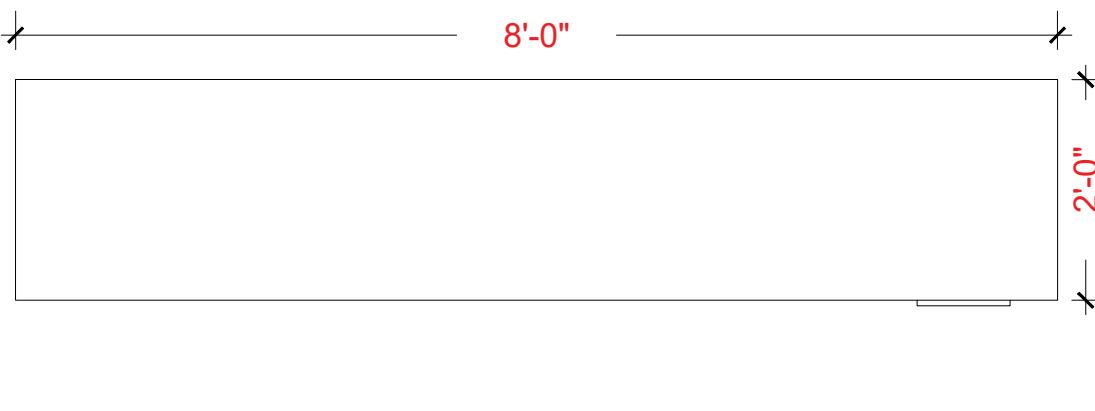

CONSOLE TABLE PLAN

D. U. N. E

design unfiltered; a process never ending
54/2, 4th cross, Link road, Malleshwaram, Bangalore 560-003
designadune@gmail.com +91 23469351

PROJECT

PROPOSED RESIDENCE
FOR RAHUL & ROHITH

DRAWING TITLE

WORKING DRAWING

DRAWING TITLE

FURNITURE DRAWINGS

DATE 16 - 11 - 2022

SCALE NOT IN SCALE

PRINT ON A3

DRAWN BY JISHNU.K


CHECKED BY THEERTHAK

NOTE


PROJECT CODE RRR

DRAWING NUMBER WD-002


REVISION NUMBER 0

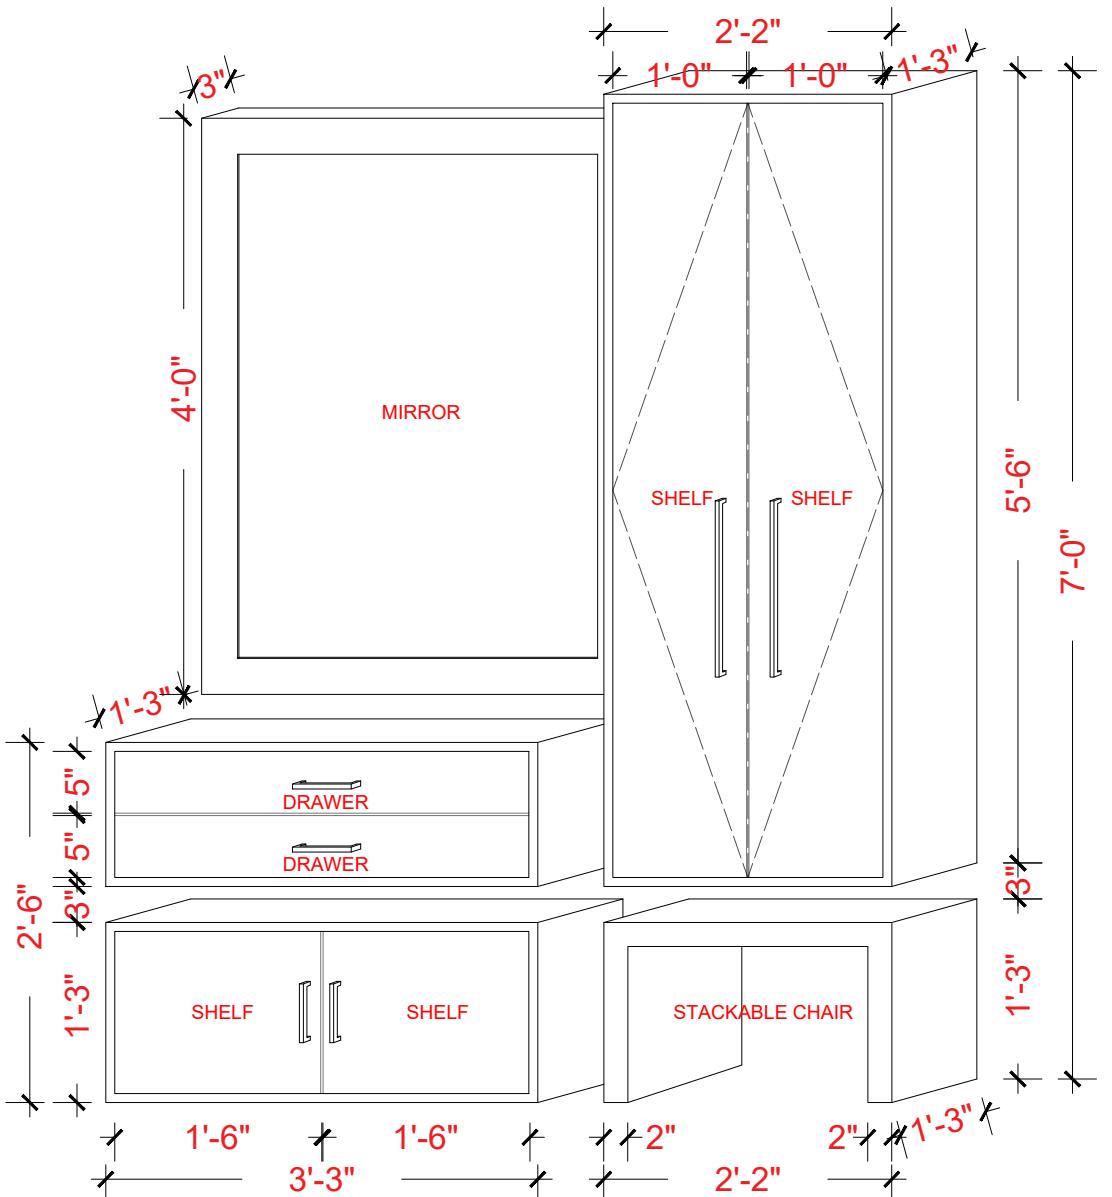



DRESSING TABLE ELEVATION

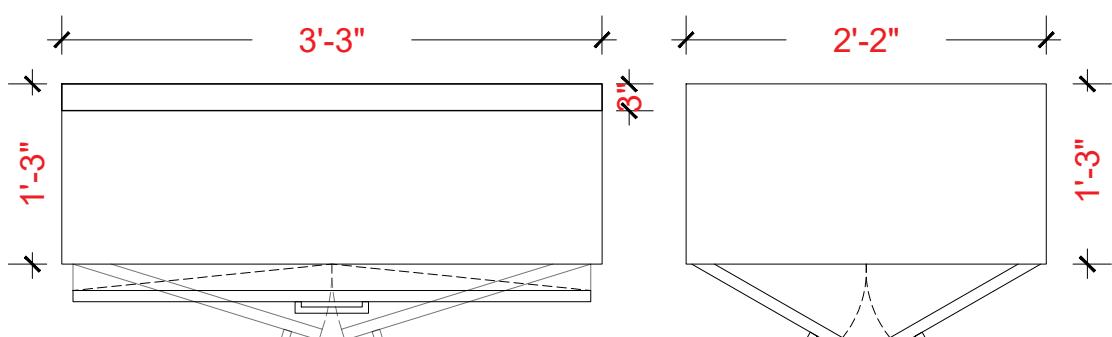

DRESSING TABLE PLAN

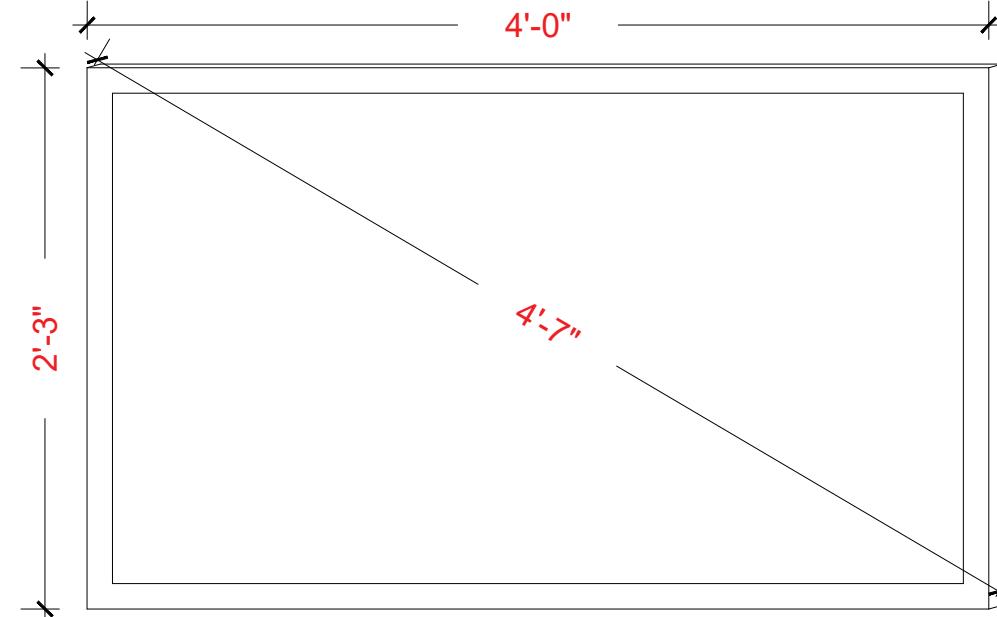

TV UNIT CONSOLE ELEVATION

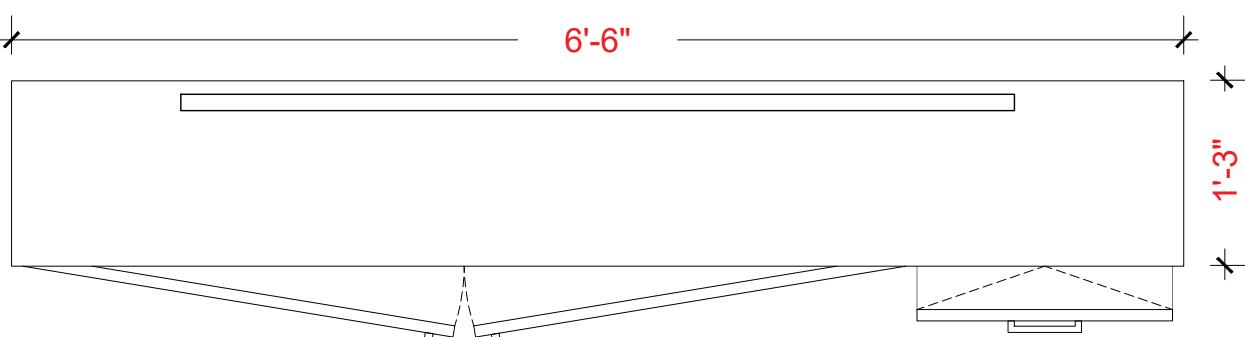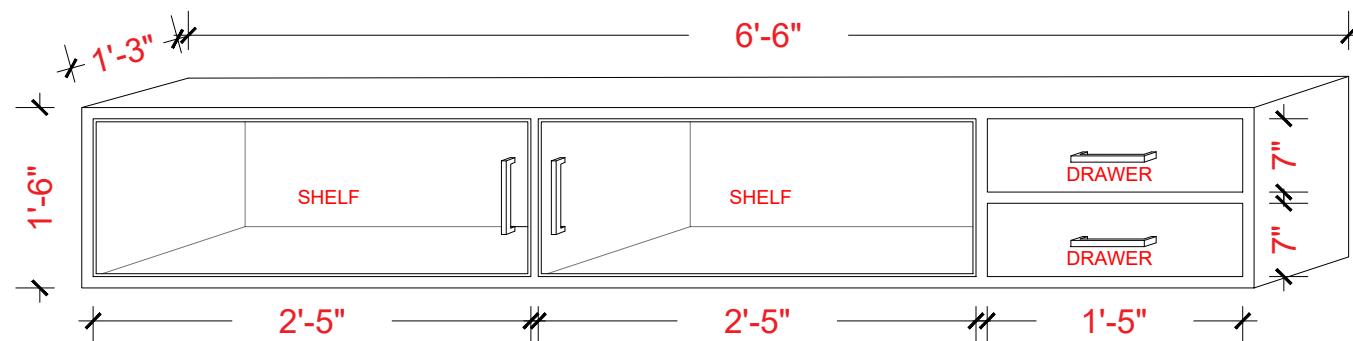

TV UNIT CONSOLE PLAN

3 D MODELS

D. U. N. E

design unfiltered; a process never ending

54/2, 4th cross, Link road, Malleshwaram, Bangalore 560-003
designadune@gmail.com +91 23469351

PROJECT

RENOVATION PROJECT
OF VASUKALLINGAL

DRAWING TITLE

WORKING DRAWING

DRAWING TITLE

EXTERIOR DESIGN

DATE 01 - 02 - 2025

SCALE NOT IN SCALE

PRINT ON A3

DRAWN BY JISHNU.K

CHECKED BY THEERTHAK

NOTE

PROJECT CODE

KLV

DRAWING NUMBER

WD-002

REVISION NUMBER

0



D. U. N. E

design unfiltered; a process never ending
54/2, 4th cross, Link road, Malleshwaram, Bangalore 560-003
designadune@gmail.com +91 23469351

PROJECT

RENOVATION PROJECT
OF VASUKALLINGAL

DRAWING TITLE

WORKING DRAWING

DRAWING TITLE

EXTERIOR DESIGN

DATE 01 - 02 - 2025

SCALE NOT IN SCALE

PRINT ON A3

DRAWN BY JISHNU.K

CHECKED BY THEERTHAK

NOTE

PROJECT CODE

KLV

DRAWING NUMBER

WD-002

REVISION NUMBER

0



D. U. N. E

design unfiltered; a process never ending
54/2, 4th cross, Link road, Malleshwaram, Bangalore 560-003
designadune@gmail.com +91 23469351

PROJECT

RENOVATION PROJECT
OF VASUKALLINGAL

DRAWING TITLE

WORKING DRAWING

DRAWING TITLE

INTERIOR DESIGN

DATE 01 - 02 - 2025

SCALE NOT IN SCALE

PRINT ON A3

DRAWN BY JISHNU.K

CHECKED BY THEERTHAK

NOTE

PROJECT CODE

KLV

DRAWING NUMBER

WD-002

REVISION NUMBER

0



PRESENTATION SHEET

D. U. N. E

design unfiltered; a process never ending
54/2, 4th cross, Link road, Malleeshwaram, Bangalore 560-003
designadune@gmail.com +91 23469351

PROJECT

PROPOSED RESIDENCE
FOR JAIN & FAMILY

DRAWING TITLE

WORKING DRAWING

DRAWING TITLE

PRESENTATION SHEET

DATE 29 - 05 - 2025

SCALE $\frac{1}{8}$ " = 1'0"

PRINT ON A3

DRAWN BY JISHNU.K

CHECKED BY THEERTHAK



NOTE

PROJECT CODE JRS

DRAWING NUMBER WD-002

REVISION NUMBER 0

N

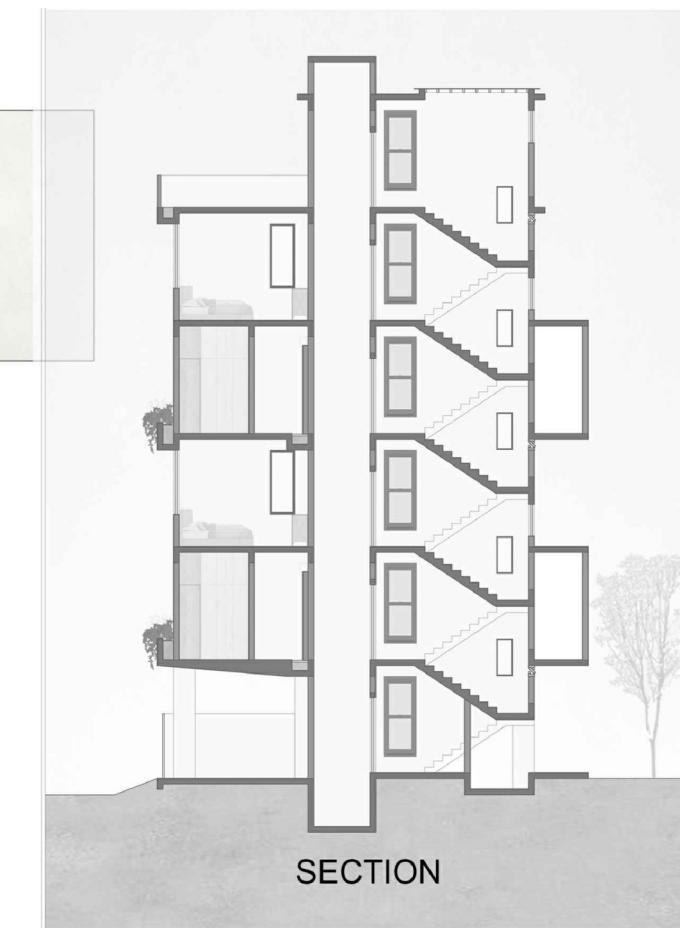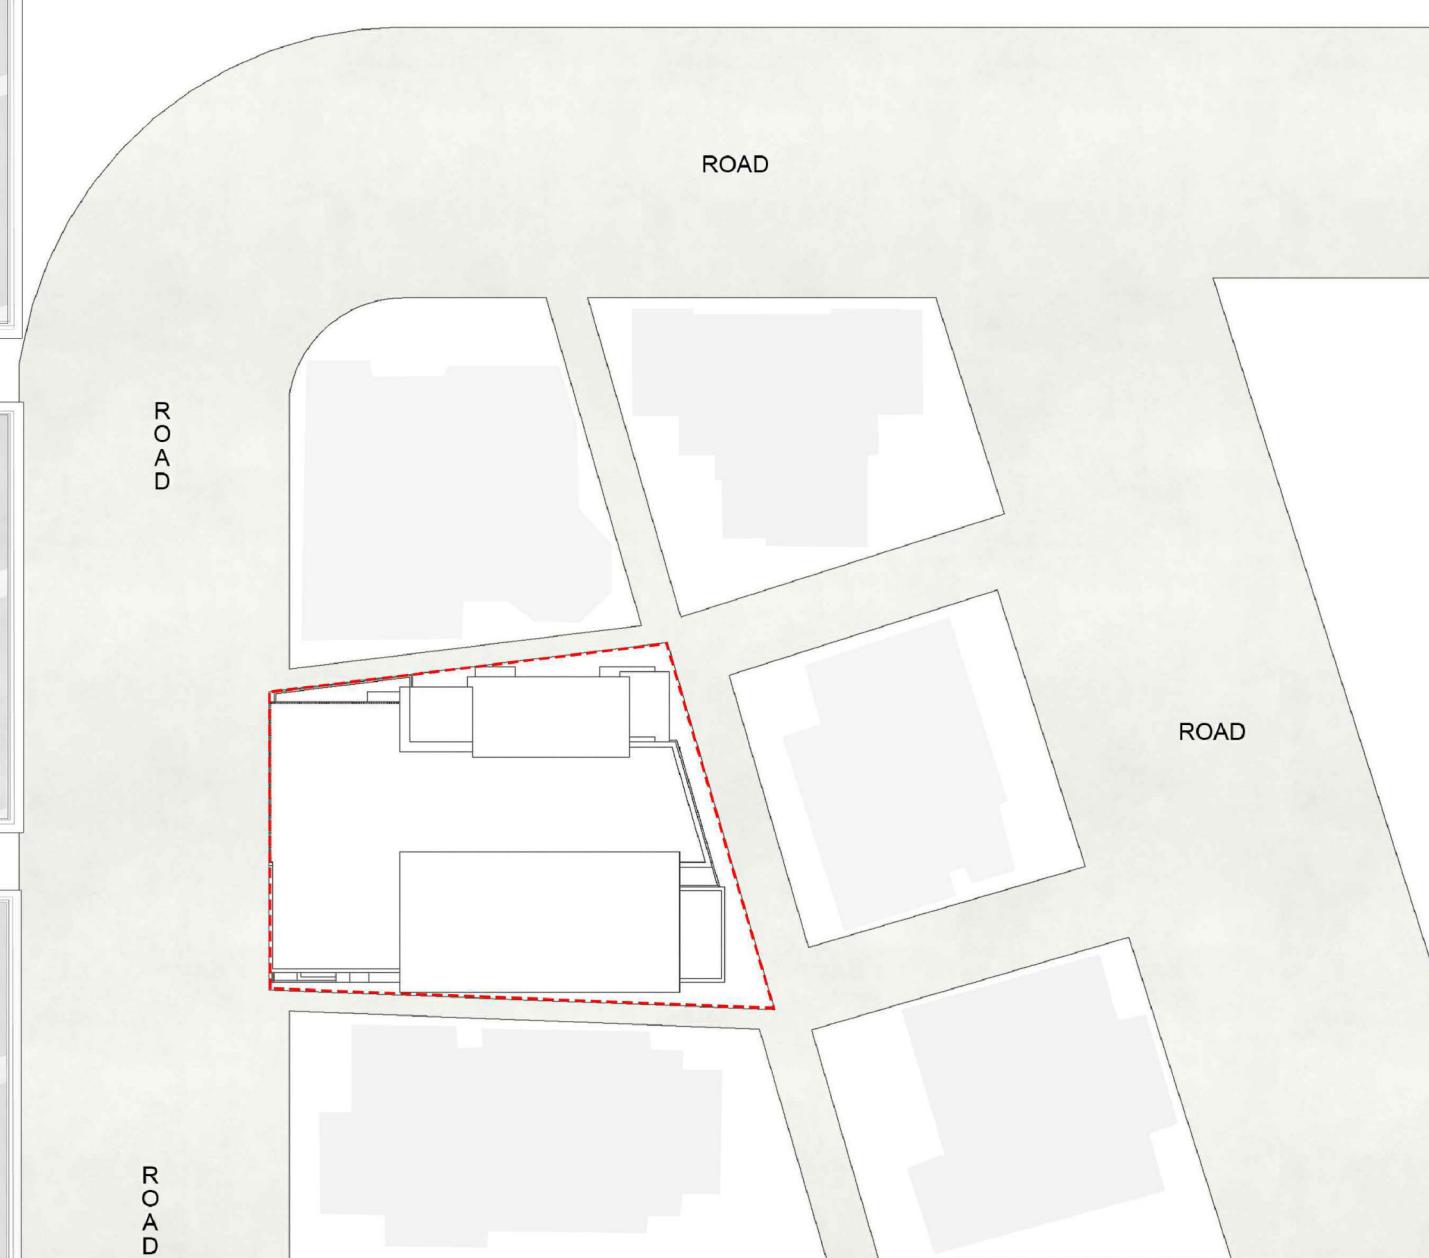

FOURTH FLOOR

TERRACE FLOOR

THANK YOU

+91 8073100366

jishnukallingal449@gmial.com